


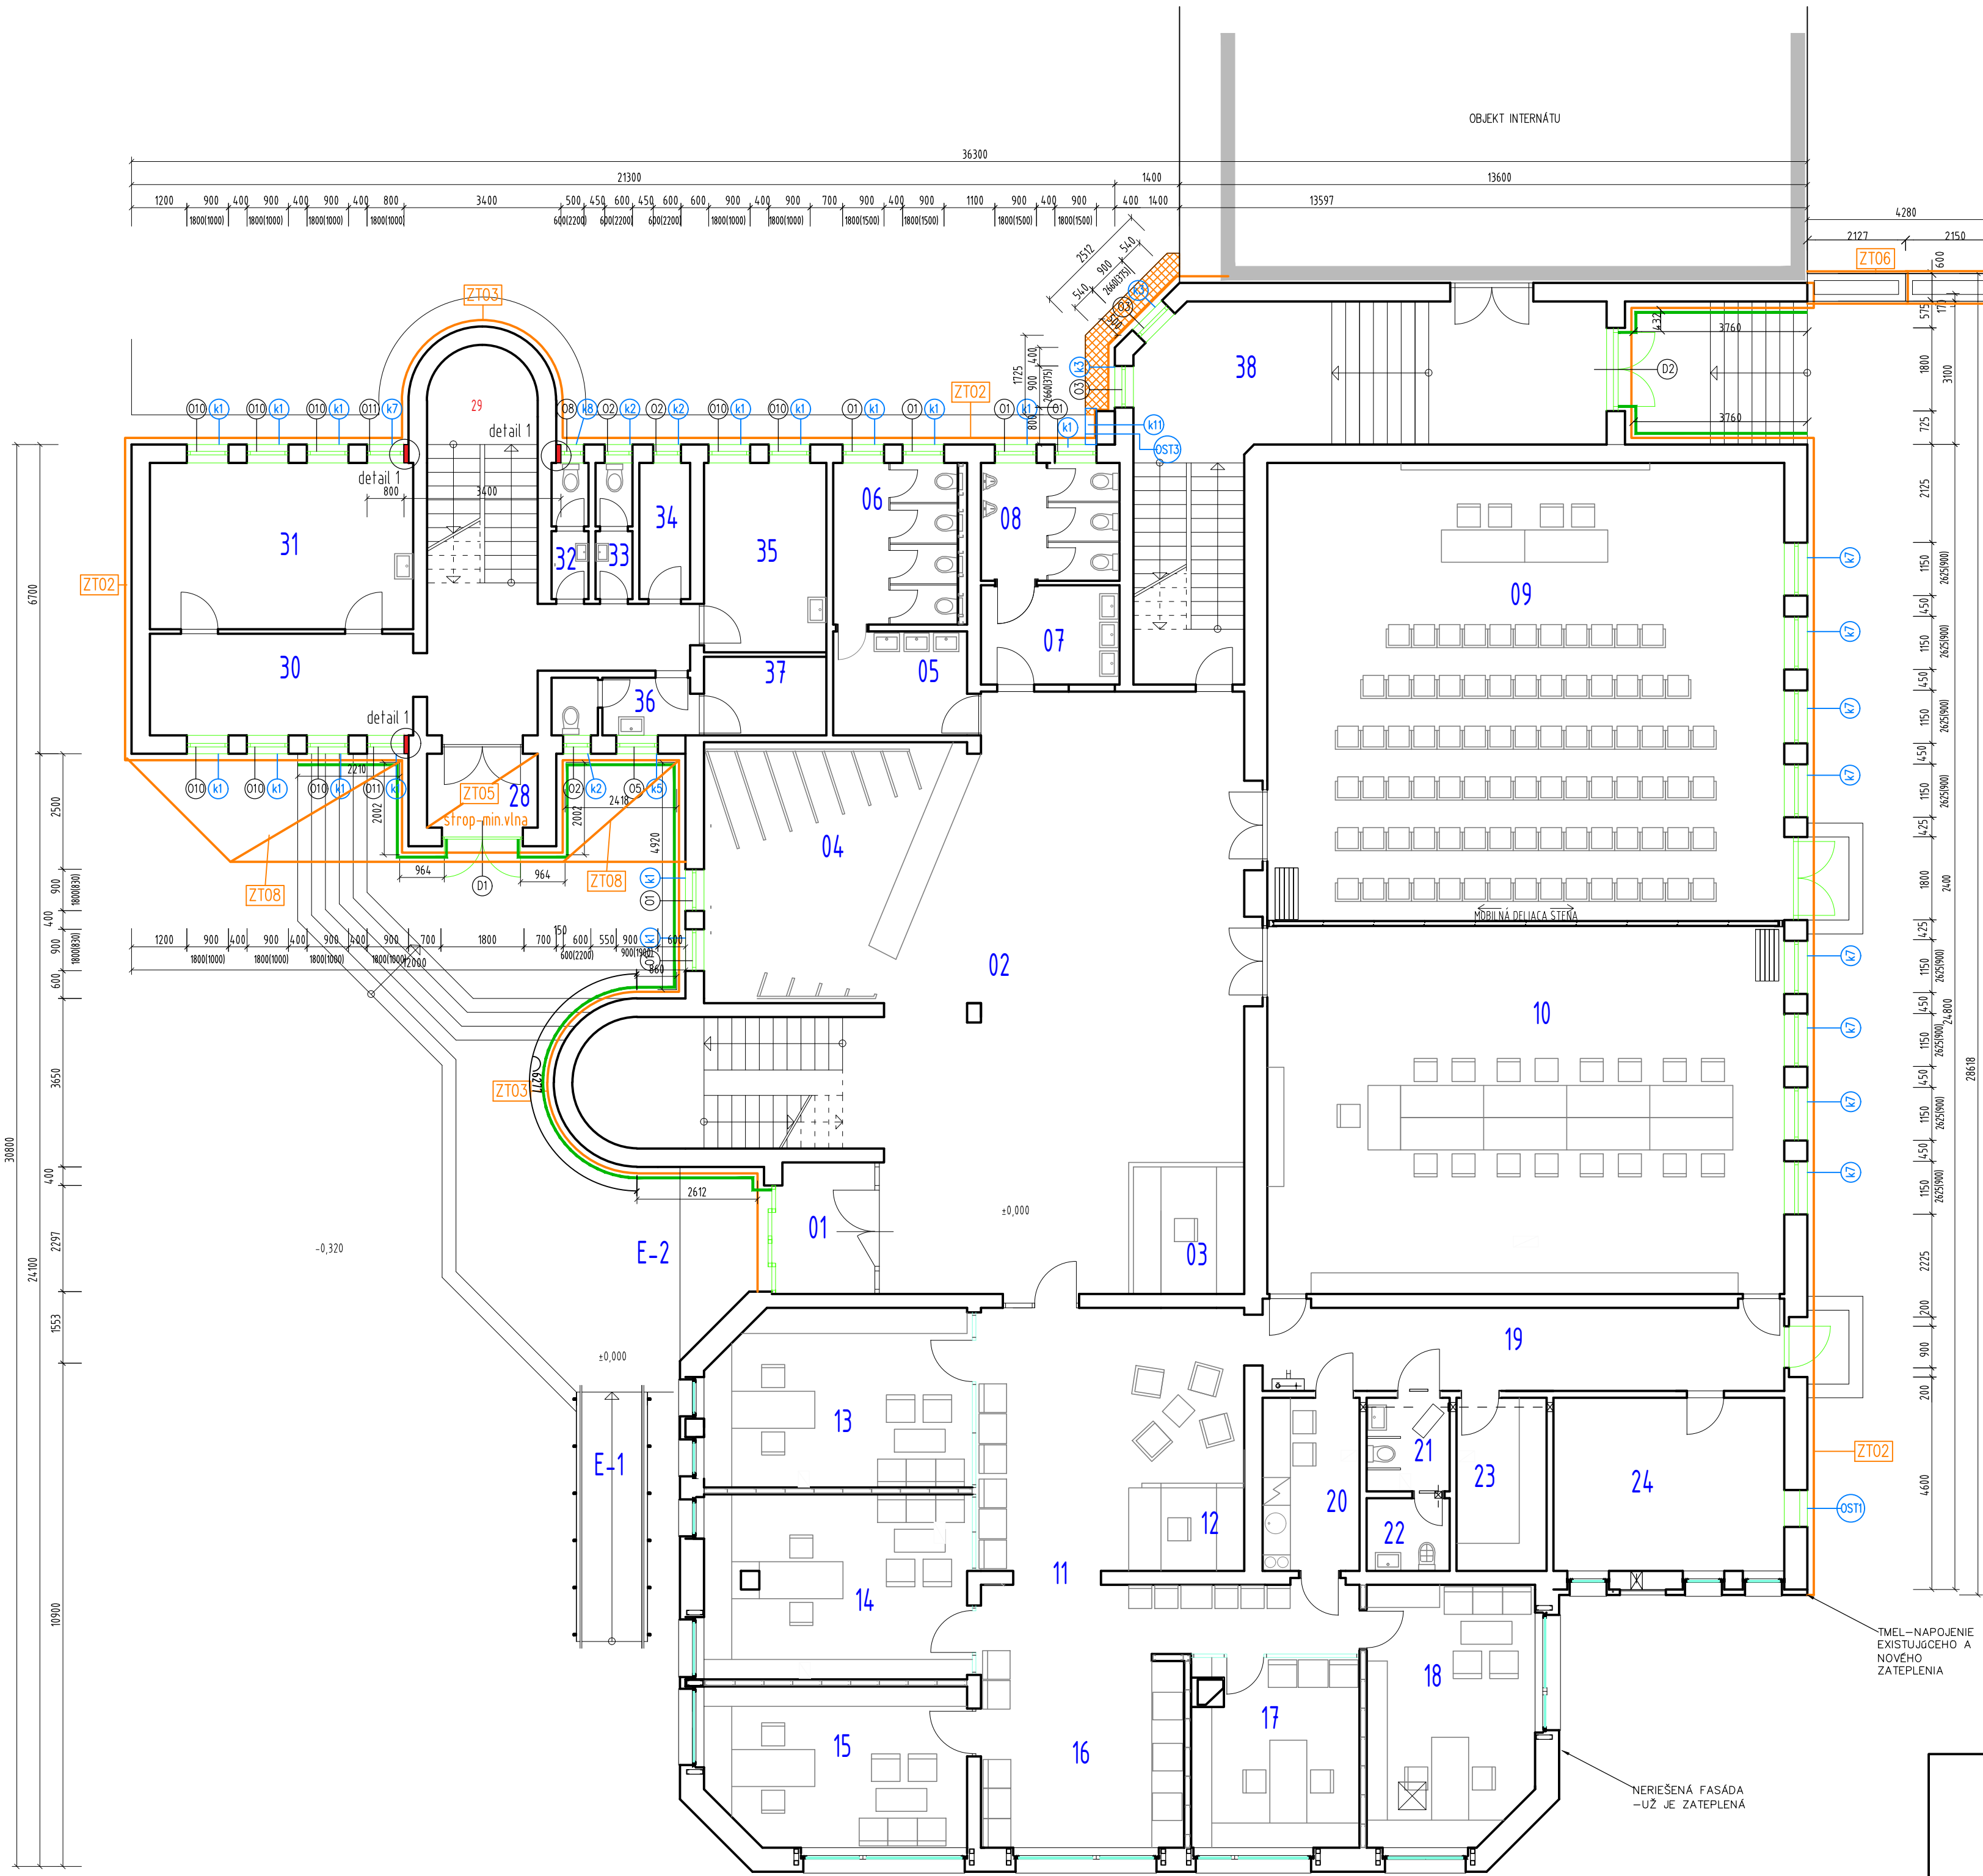

LEGENDA MESTNOSTÍ 1NP

Č. M.	ÚČEL MESTNOSTI	PLOCHA (m2)
E-1	RAMPA	8,32
E-2	VSTUPNÁ PLOCHA	35,6
1	ZÁDVERE	6,05
2	FOYER	89,3
3	RECEPCIA	6,6
4	ŠATŇA	27,86
5	PREDSEŇ WC ŽENY	6,52
6	WC ŽENY	9,38
7	PREDSEŇ WC MUŽI	6,45
8	WC MUŽI	7,19
9	KONFERENČNÁ SÁLA	111,16
10	KONFERENČNÁ SÁLA - ŠTUDENTSKÝ PARLAMENT	89,31
11	HALA	51,92
12	INFORMÁCIE	4,5
13	MANAŽÉR	21,38
14	KONZULTÁCIE	23,04
15	KONZULTÁCIE	19,14
16	KOPIRKY	7,85

Č. M.	ÚČEL MESTNOSTI	PLOCHA (m2)
17	KONZULTÁCIE	14,67
18	KANCELÁRIA	28,0
19	CHODBA	28,24
20	KUCHYNKA	7,87
21	WC ŽŤP	3,65
22	UPRATOVANIE	2,84
23	SKLAD	7,31
24	STROJOVNÁ	18,75
28	ZÁDVERE	3,84
29	SCHODISTE + CHODBA	19,66
30	ĎAKÁREN	12,54
31	ZUBNÁ ORDINÁCIA	20,52
32	PREDSEŇ WC MUŽI	2,36
33	PREDSEŇ WC ŽENY	2,36
34	MESTNOST PRE UPRATOVAČKU	3,25
35	DENNÁ MESTNOST	10,86
36	WC ZAMESTNANCI	3,98
37	SKLAD	4,5
38	VSTUP + SCHODISTE	43,6

SCHEMATICKÝ PODORYS S NÁVRHOM ZATEPLENIA

LEGENDA ZATEPLOVANIA:

- ZT01** ZATEPLENIE OBVODOVÉHO PLAŠTA V ÚROVNI SOKLA (V 1.NP) – (0,3M–0,85M NAD ÚROVŇOU TERÉNU):
- LEPIACA MALTA
 - TVRDENÁ NENASIAKAVÁ TEPELNÁ IZOLÁCIA (napr. STYRODUR alt. EXTRUD.POLYSTYRÉN), HR.100mm
 - VÝSTUŽNÁ VRSTVA – MALTA
 - PODKLADNÝ NÁTER
 - TENKOVRSŤOVÁ SILIKÁTOVÁ ROZTIERANÁ OMIETKA
- ZT02** ZATEPLENIE OBVODOVÉHO PLAŠTA V ÚROVNI 1.NP–3.NP:
- LEPIACA MALTA
 - TEPELNÁ IZOLÁCIA: PLATNE Z POLYSTYRÉNU EPS 70F v kombinácii FASADNA MINERÁLNA VLNA– HR.140mm (KOTVENÉ PLASTOVÝMI TANIEROVÝMI HMOZDINKAMI)–DETAILNEJSIE VIÐ výkr.č.06– POHLADY–FIGURY
 - VÝSTUŽNÁ VRSTVA – MALTA
 - PODKLADNÝ NÁTER
 - TENKOVRSŤOVÁ SILIKÁTOVÁ ROZTIERANÁ OMIETKA
- ZT03** ZATEPLENIE OBVODOVÉHO PLAŠTA OKOLO SCHODISKA:
- LEPIACA MALTA
 - TEPELNÁ IZOLÁCIA TRIEDY REAKCIE NA OHEŇ ASPOŇ A2–s1, d0 (napr.DOSKY STYRCON alt. MINERÁLNA VLNA), HR.140mm
 - VÝSTUŽNÁ VRSTVA – MALTA
 - PODKLADNÝ NÁTER
 - TENKOVRSŤOVÁ SILIKÁTOVÁ ROZTIERANÁ OMIETKA
- ZT04** ZATEPLENIE OSTENÍ A NADPRAŽIA OKIEN A DVERÍ V ÚROVNI 1.NP–3.NP:
- LEPIACA MALTA
 - TVRDENÁ TEPELNÁ IZOLÁCIA (napr. STYRODUR alt. EXTRUD.POLYSTYRÉN), HR.30mm
 - VÝSTUŽNÁ VRSTVA – MALTA
 - PODKLADNÝ NÁTER
 - TENKOVRSŤOVÁ SILIKÁTOVÁ ROZTIERANÁ OMIETKA
- ZT05** ZATEPLENIE SPODNEJ PLOCHY STROPNÝCH DOSIEK NAD VSTUPOM
- LEPIACA MALTA
 - TEPELNÁ IZOLÁCIA TRIEDY REAKCIE NA OHEŇ ASPOŇ A2–s1, d0 (napr.DOSKY STYRCON alt. MINERÁLNA VLNA), HR.140mm
 - VÝSTUŽNÁ VRSTVA – MALTA
 - PODKLADNÝ NÁTER
 - TENKOVRSŤOVÁ SILIKÁTOVÁ ROZTIERANÁ OMIETKA
- ZT06** ZATEPLENIE OPORNÉHO MŮRIKA:
- LEPIACA MALTA
 - TVRDENÁ TEPELNÁ IZOLÁCIA (napr. STYRODUR alt. EXTRUD.POLYSTYRÉN), HR.30mm
 - VÝSTUŽNÁ VRSTVA – MALTA
 - PODKLADNÝ NÁTER
 - TENKOVRSŤOVÁ SILIKÁTOVÁ ROZTIERANÁ OMIETKA
- ZT07** ZATEPLENIE OSTENÍ A NADPRAŽIA OKIEN A DVERÍ V ÚROVNI 1.NP–3.NP:
- LEPIACA MALTA
 - TVRDENÁ TEPELNÁ IZOLÁCIA (napr.DOSKY STYRCON alt. MINERÁLNA VLNA), HR.30mm
 - VÝSTUŽNÁ VRSTVA – MALTA
 - PODKLADNÝ NÁTER
 - TENKOVRSŤOVÁ SILIKÁTOVÁ ROZTIERANÁ OMIETKA
- ZT08** ZATEPLENIE SPODNEJ PLOCHY STROPNÝCH DOSIEK NAD VYKUROV.PODLAŽÍM
- LEPIACA MALTA
 - TEPELNÁ IZOLÁCIA TRIEDY REAKCIE NA OHEŇ ASPOŇ A2–s1, d0 (napr.DOSKY STYRCON alt. MINERÁLNA VLNA), HR.220mm
 - VÝSTUŽNÁ VRSTVA – MALTA
 - PODKLADNÝ NÁTER
 - TENKOVRSŤOVÁ SILIKÁTOVÁ ROZTIERANÁ OMIETKA

LEGENDA:

- ☐ OKENNÉ A DVERNÉ OTVORY
- ☐ OBVODOVÉ A VNÚTORNÉ KONŠTRUKCIE
- ☐ ZATEPLENIE OBVODOVEJ STENY **ZT02** **ZT03** (viď. legenda zateplovania)
- ☐ ZATEPLENIE OBVODOVEJ STENY – SOKLA **ZT01** (viď. legenda zateplovania)
- ☐ NOVÝ OKAPOVÝ CHODNÍK (štrkový zväz)
- ☐ DOMUROVANIE – YTONG HR.100MM (NOVÉ KONŠTRUKCIE PREKOTVÍT S EXIS. STENOU)
- ☐ KERAMICKÝ SOKLIK V.100mm

UPOZORNENIE:

- REALNÉ ROZMERY PRED REALIZÁCIOU PREMERAŤ A PREKONTROLOVAŤ PRIAMO NA STAVBE !!!
- AK SA VYSKYTNÚ NOVE SKUTOČNOSTI, KTORÉ MAJÚ VPLYV NA REALIZÁCIU STAVBY, PROJEKTANT SI VYHRADZUJE PRÁVO NA ZMENU PROJEKTU POČAS REALIZÁCIE.
- STATIK SI VYHRADZUJE PRÁVO NA ZMENU PROJEKTOVEJ DOKUMENTÁCIE POČAS REALIZÁCIE AJ Z INÝCH VECNÝCH DOVODOV V ZÁJME DOSIAHNUTIA VAŠEJ BEZPEČNOSTI STAVBY.
- KONŠTRUKCIE, KTORÉ NIE SÚ ZAZNAČENÉ VO VÝKRESOVEJ DOKUMENTÁCII SA BLIŽŠIE ŠPECIFIKUJÚ POČAS REALIZÁCIE.
- PRI VÝSTAVBE JE NUTNÉ DODRŽAŤ VŠETKY PREDPISY A ŠPECIFIKÁCIE PODLA NARIADENÍ VÝROBCOV MATERIÁLOV A PRVKOV, KTORÉ NIE SÚ V PROJEKTE BLIŽŠIE ŠPECIFIKOVANÉ.
- PRI NEŠPECIFIKOVANÍ KRITÉRIÍ JE NUTNÉ DODRŽAŤ ZÁKONY, TECHNICKÉ NORMY A PREDPISY, PRIČOM ROZMERY MŮROV SÚ KÓTOVANÉ S VÝROBNÝMI ROZMERMÍ KUSOVÝCH STAVBY.

	ZODP.PROJEKTANT ING. ARCH. R. KOČAIDA	VYPRACOVAL ING. ARCH. R. KOČAIDA	KRESLIL ING. JURA J. PAVLOVÉ	K2 atelier S.r.o. Dlhá 16, 949 01 Nitra, 0908-778 761 0911-778 761	
	STAVEBNÍK: Univerzita Konštantína Filozofa v Nitre, Tr. Andreja Hlinku 1, Nitra, PSČ 949 74, SR				
	AKCIA: Zníženie energetickej náročnosti budovy spoločenskej prístavby ŠD UKF Zobor, Dražovská 2, Nitra K.Ú. Zobor, parc.č. 4594/2				DÁTUM: 10/2018
	VÝKRES: PĎORYS 1NP				STUPEŇ: PROJEKT
					FORMÁT: A4
				MIERKA: 1:100	VÝKRES ČÍSLO: 02