


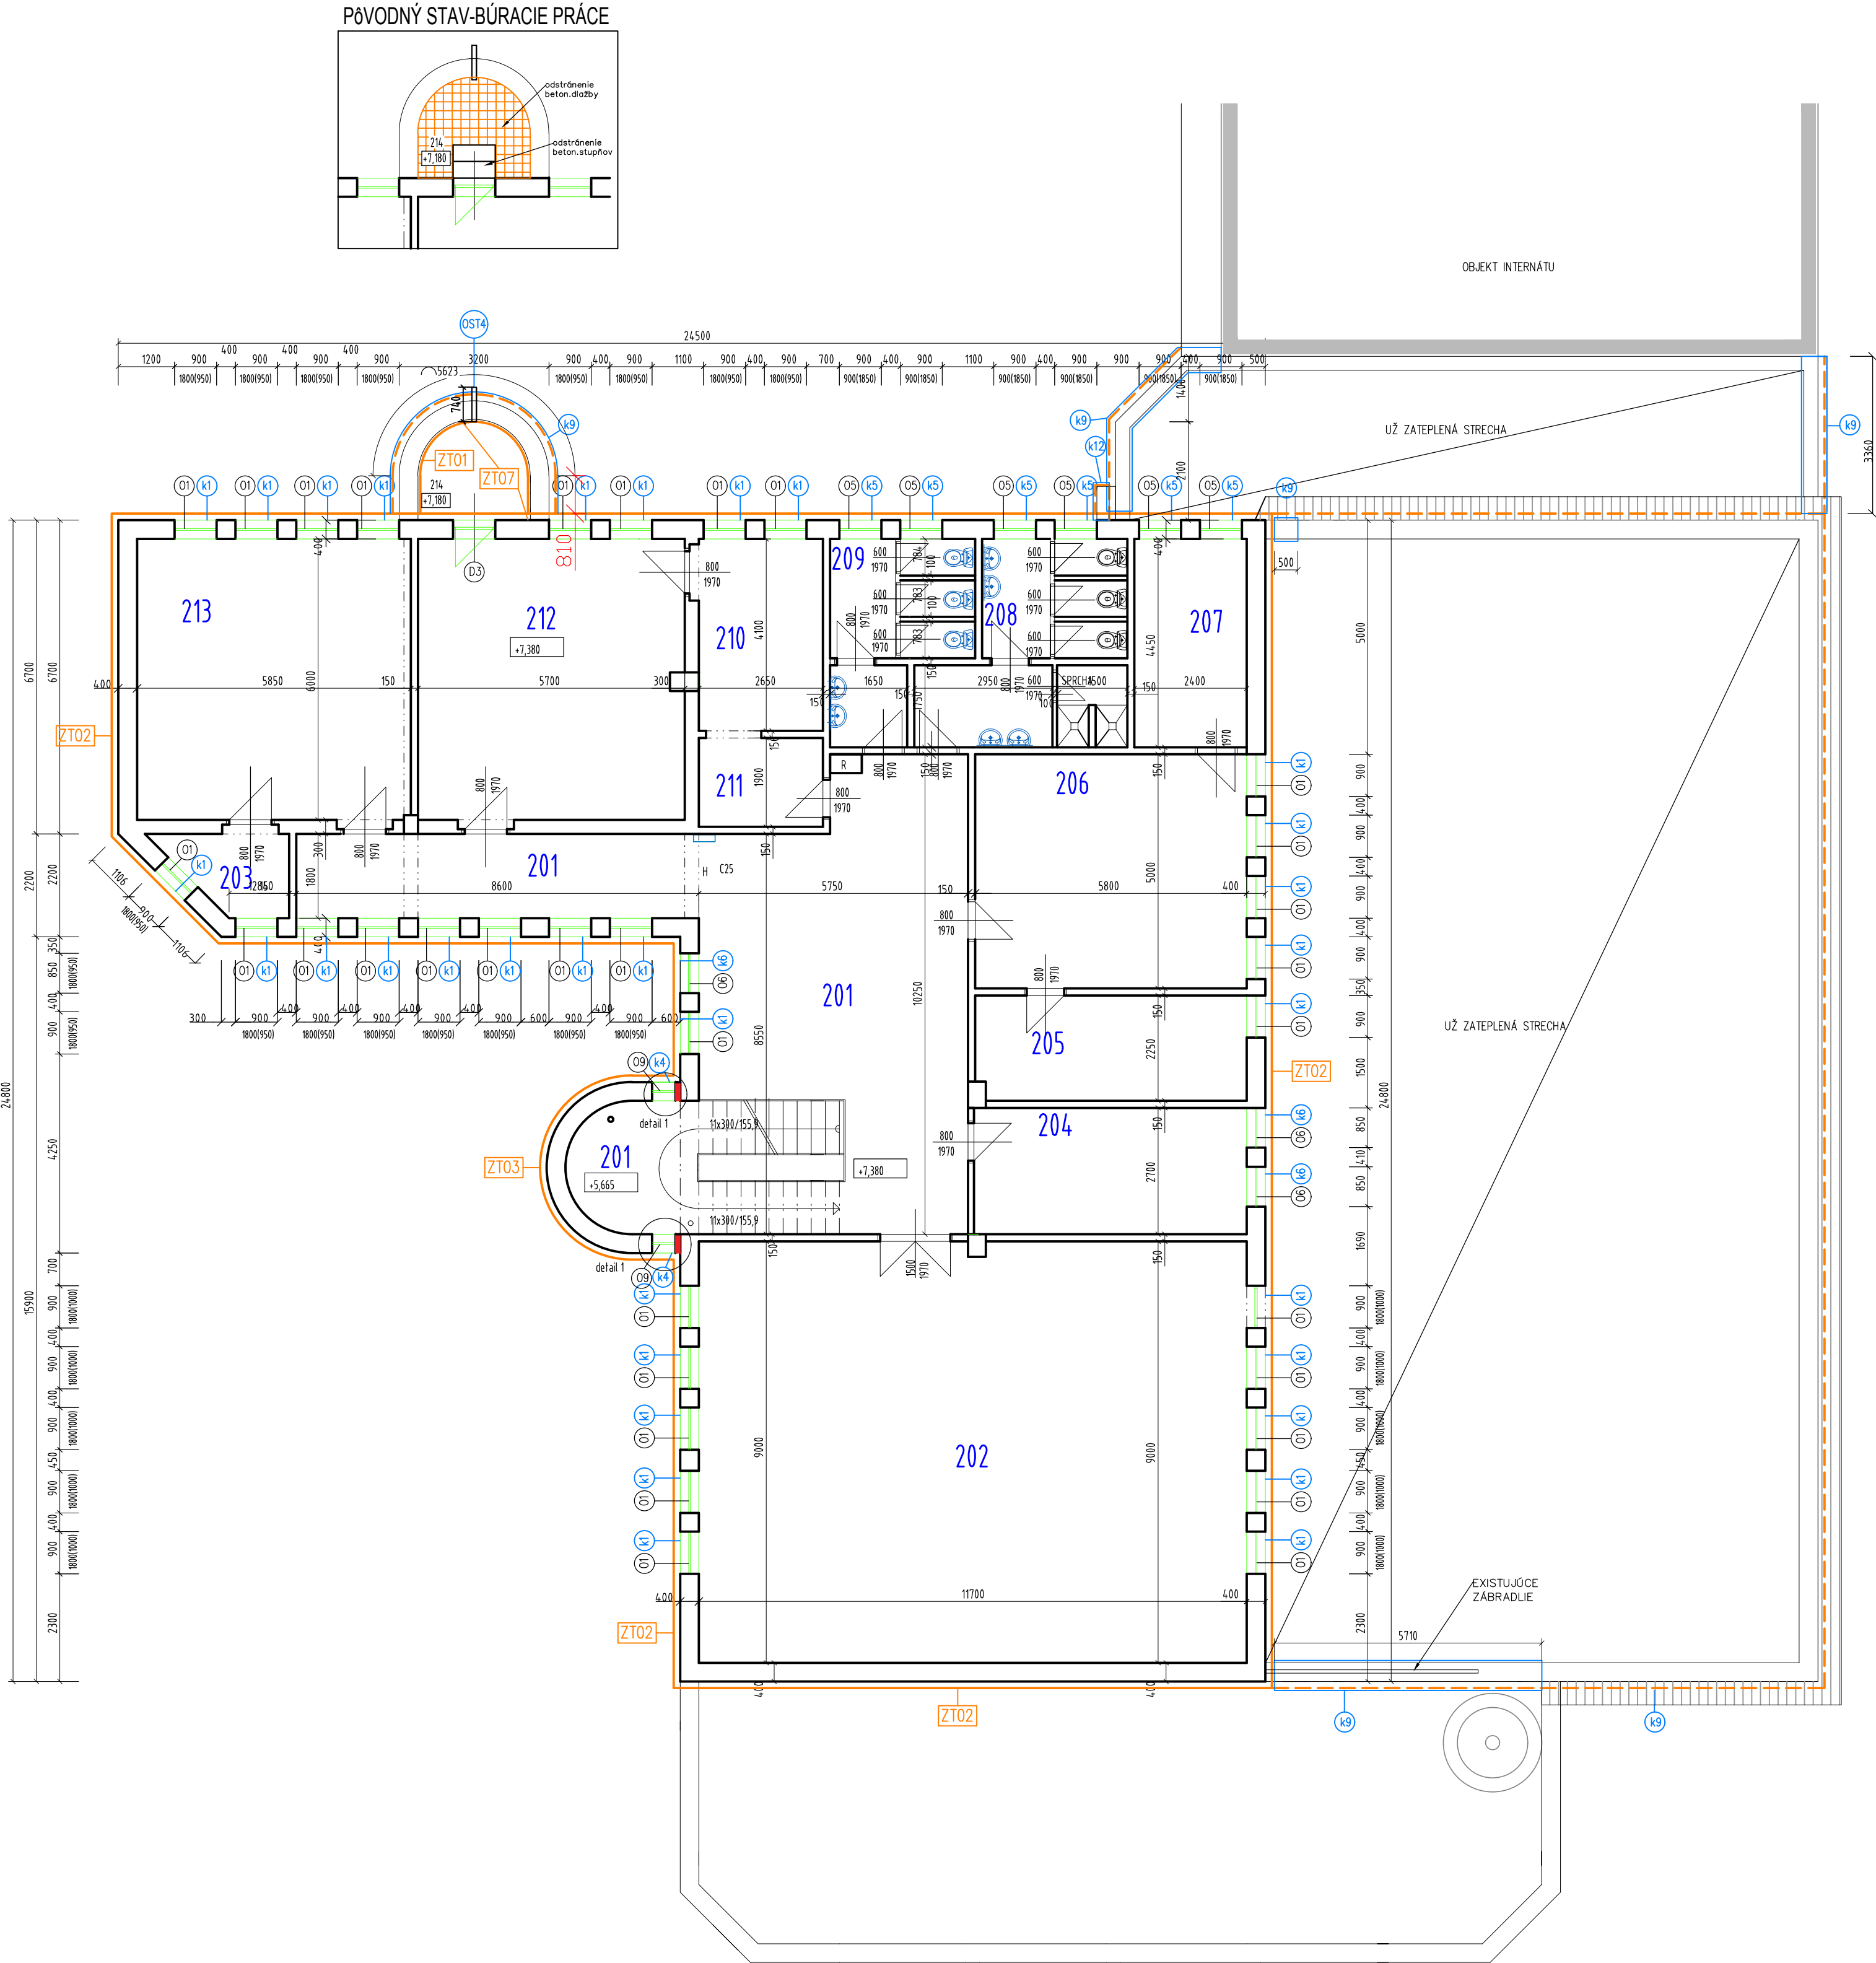

LEGENDA MĚSTNOSTÍ 3.NP		
Č. M.	ÚČEL MĚSTNOSTI	PLOCHA (m2)
201	SCHODIŠTĚ + CHODBA	76,90
202	STUŽOVNÁ	95,39
203	SKLAD	3,93
204	SKLAD	15,73
205	SKLAD	12,96
206	MĚSTNOST PRO MIMOŠKOLSKÉ AKTIVITY ŽÁKŮ	29,01
207	SKLAD	19,68
208	PŘEDSĚN + WC ŽENY	36,33
209	PŘEDSĚN + WC MUŽI	11,04
210	SKLAD	19,87
211	SKLAD PRO UPRÁVČOVÁNÍ	5,04
212	MĚSTNOST PRO MIMOŠKOLSKÉ AKTIVITY ŽÁKŮ	34,20
213	MĚSTNOST PRO MIMOŠKOLSKÉ AKTIVITY ŽÁKŮ	35,10
214	BALKÓN	6,54

LEGENDA ZATEPLOVÁNÍ:

- ZT01** ZATEPLENÍ OBVODOVÉHO PLÁŠŤA V ÚROVNI SOKLA (V 1.NP) – (0,3M–0,85M NAD ÚROVŇOU TERÉNU):
- LEPIACIA MALTA
 - TVRDENÁ NENASIAKAVÁ TEPELNÁ IZOLÁCIA (napr. STYRODUR alt. EXTRUD.POLYSTYRÉN), HR.100mm
 - VÝSTUŽNÁ VRSTVA – MALTA
 - PODKLADNÝ NÁTER
 - TENKOVRSŤOVÁ SILIKÁTOVÁ ROZTIERANÁ OMIETKA
- ZT02** ZATEPLENÍ OBVODOVÉHO PLÁŠŤA V ÚROVNI 1.NP–3.NP:
- LEPIACIA MALTA
 - TEPELNÁ IZOLÁCIA: PLATNÉ Z POLYSTYRÉNU EPS 70F v kombinácii FASADNA MINERÁLNA VLNA– HR.140mm (KOTVENÉ PLASTOVÝMI TANIEROVÝMI HMOŽDINKAMI)–DETAILNEJŠIE VIÐ VÝKR.č.06– POHLADY–FIGURY
 - VÝSTUŽNÁ VRSTVA – MALTA
 - PODKLADNÝ NÁTER
 - TENKOVRSŤOVÁ SILIKÁTOVÁ ROZTIERANÁ OMIETKA
- ZT03** ZATEPLENÍ OBVODOVÉHO PLÁŠŤA OKOLO SCHODISKA:
- LEPIACIA MALTA
 - TEPELNÁ IZOLÁCIA TRIEDY REAKCIE NA OHEŇ ASPOŇ A2–s1, d0 (napr.DOSKY STYRCON alt. MINERÁLNA VLNA), HR.140mm
 - VÝSTUŽNÁ VRSTVA – MALTA
 - PODKLADNÝ NÁTER
 - TENKOVRSŤOVÁ SILIKÁTOVÁ ROZTIERANÁ OMIETKA
- ZT04** ZATEPLENÍ OSTEŇÍ A NADPRAŽIA OKIEN A DVERÍ V ÚROVNI 1.NP–3.NP:
- LEPIACIA MALTA
 - TVRDENÁ TEPELNÁ IZOLÁCIA (napr. STYRODUR alt. EXTRUD.POLYSTYRÉN), HR.30mm
 - VÝSTUŽNÁ VRSTVA – MALTA
 - PODKLADNÝ NÁTER
 - TENKOVRSŤOVÁ SILIKÁTOVÁ ROZTIERANÁ OMIETKA
- ZT05** ZATEPLENÍ SPODNEJ PLOCHY STROPNÝCH DOSIEK NAD VSTUPOM
- LEPIACIA MALTA
 - TEPELNÁ IZOLÁCIA TRIEDY REAKCIE NA OHEŇ ASPOŇ A2–s1, d0 (napr.DOSKY STYRCON alt. MINERÁLNA VLNA), HR.140mm
 - VÝSTUŽNÁ VRSTVA – MALTA
 - PODKLADNÝ NÁTER
 - TENKOVRSŤOVÁ SILIKÁTOVÁ ROZTIERANÁ OMIETKA
- ZT06** ZATEPLENÍ OPORNÉHO MŮRIKA:
- LEPIACIA MALTA
 - TVRDENÁ TEPELNÁ IZOLÁCIA (napr. STYRODUR alt. EXTRUD.POLYSTYRÉN), HR.30mm
 - VÝSTUŽNÁ VRSTVA – MALTA
 - PODKLADNÝ NÁTER
 - TENKOVRSŤOVÁ SILIKÁTOVÁ ROZTIERANÁ OMIETKA
- ZT07** ZATEPLENÍ OSTEŇÍ A NADPRAŽIA OKIEN A DVERÍ V ÚROVNI 1.NP–3.NP:
- LEPIACIA MALTA
 - TVRDENÁ TEPELNÁ IZOLÁCIA (napr.DOSKY STYRCON alt. MINERÁLNA VLNA), HR.30mm
 - VÝSTUŽNÁ VRSTVA – MALTA
 - PODKLADNÝ NÁTER
 - TENKOVRSŤOVÁ SILIKÁTOVÁ ROZTIERANÁ OMIETKA

LEGENDA:

- OKENNÉ A DVERNÉ OTVORY
- OBVODOVÉ A VNÚTORNÉ KONŠTRUKCIE
- ▬ ZATEPLENIE OBVODOVEJ STENY ZT02 ZT03 (víd. legenda zateplovania)
- ▬ ZATEPLENIE OBVODOVEJ STENY – SOKLA ZT01 (víd. legenda zateplovania)
- ▬ NOVÝ OKAPOVÝ CHODNÍK (štrkový zber)
- DOMUROVANIE – YTONG HR.100MM (NOVÉ KONŠTRUKCIE PREKOTVÍT S EXIS. STENOU)

UPOZORNENIE:

- REALNÉ ROZMERY PRED REALIZÁCIOU PREMERAŤ A PREKONTROLOVAŤ PRIAMO NA STAVBE !!!
- AK SA VYSKYTNÚ NOVE ZISTOVANOSTI, KTORÉ MAJÚ VPLYV NA REALIZÁCIU STAVBY, PROJEKTANT SI VYHRADZUJE PRÁVO NA ZMENU PROJEKTU POČAS REALIZÁCIE.
- STATIK SI VYHRADZUJE PRÁVO NA ZMENU PROJEKTOVEJ DOKUMENTÁCIE POČAS REALIZÁCIE AJ Z INÝCH VEČNÝCH DOVODOV V ZÁJME DOSIAHNUTIA VACŠEJ BEZPEČNOSTI STAVBY.
- KONŠTRUKCIE, KTORÉ NIE SÚ ZAZNACENÉ VO VÝKRESOVEJ DOKUMENTÁCII SA BLIŽŠIE ŠPECIFIKUJÚ POČAS REALIZÁCIE.
- PRI VÝSTAVBE JE NUTNÉ DODRŽAŤ VŠETKY PREDPISY A ŠPECIFIKÁCIE PODLA NARIADENÍ VÝROBOVÝCH MATERIÁLOV A PRVKOV, KTORÉ NIE SÚ V PROJEKTE BLIŽŠIE ŠPECIFIKOVANÉ.
- PRI NEŠPECIFIKOVANÍ KRITÉRIÍ JE NUTNÉ DODRŽAŤ ZÁKONY, TECHNICKÉ NORMY A PREDPISY, PRIČOM ROZMERY MŮROV SÚ KÓTOVANÉ S VÝROBNÝMI ROZMERMÍ KUSOVÝCH STAVBY.

	ZODP. PROJEKTANT ING. ARCH. R. KOČAIDA	VYPRACOVAL ING. ARCH. R. KOČAIDA	KRESLIL ING. JURAJ PAVLOVÍČ	K2 ateliér s.r.o. Dlhá 16, 949 01 Nitra, 0908-778 761 0911-778 761
	STAVEBNÍK: Univerzita Konštantína Filozofa v Nitre, Tr. Andreja Hlinku 1, Nitra, PSČ 949 74, SR			
	AKCIA: Zníženie energetickej náročnosti budovy spoločenskej prístavby ŠD UKF Zobor, Dražovská 2, Nitra KÚ Zobor, parč.č. 4394/2			
	VÝKRES: PŮDORYS 3.NP			
				DÁTUM: 10/2018 STUPEŇ: PROJEKT FORMÁT: A4 MIERKA: 1:100 VÝKRES ČÍSLO: 04