



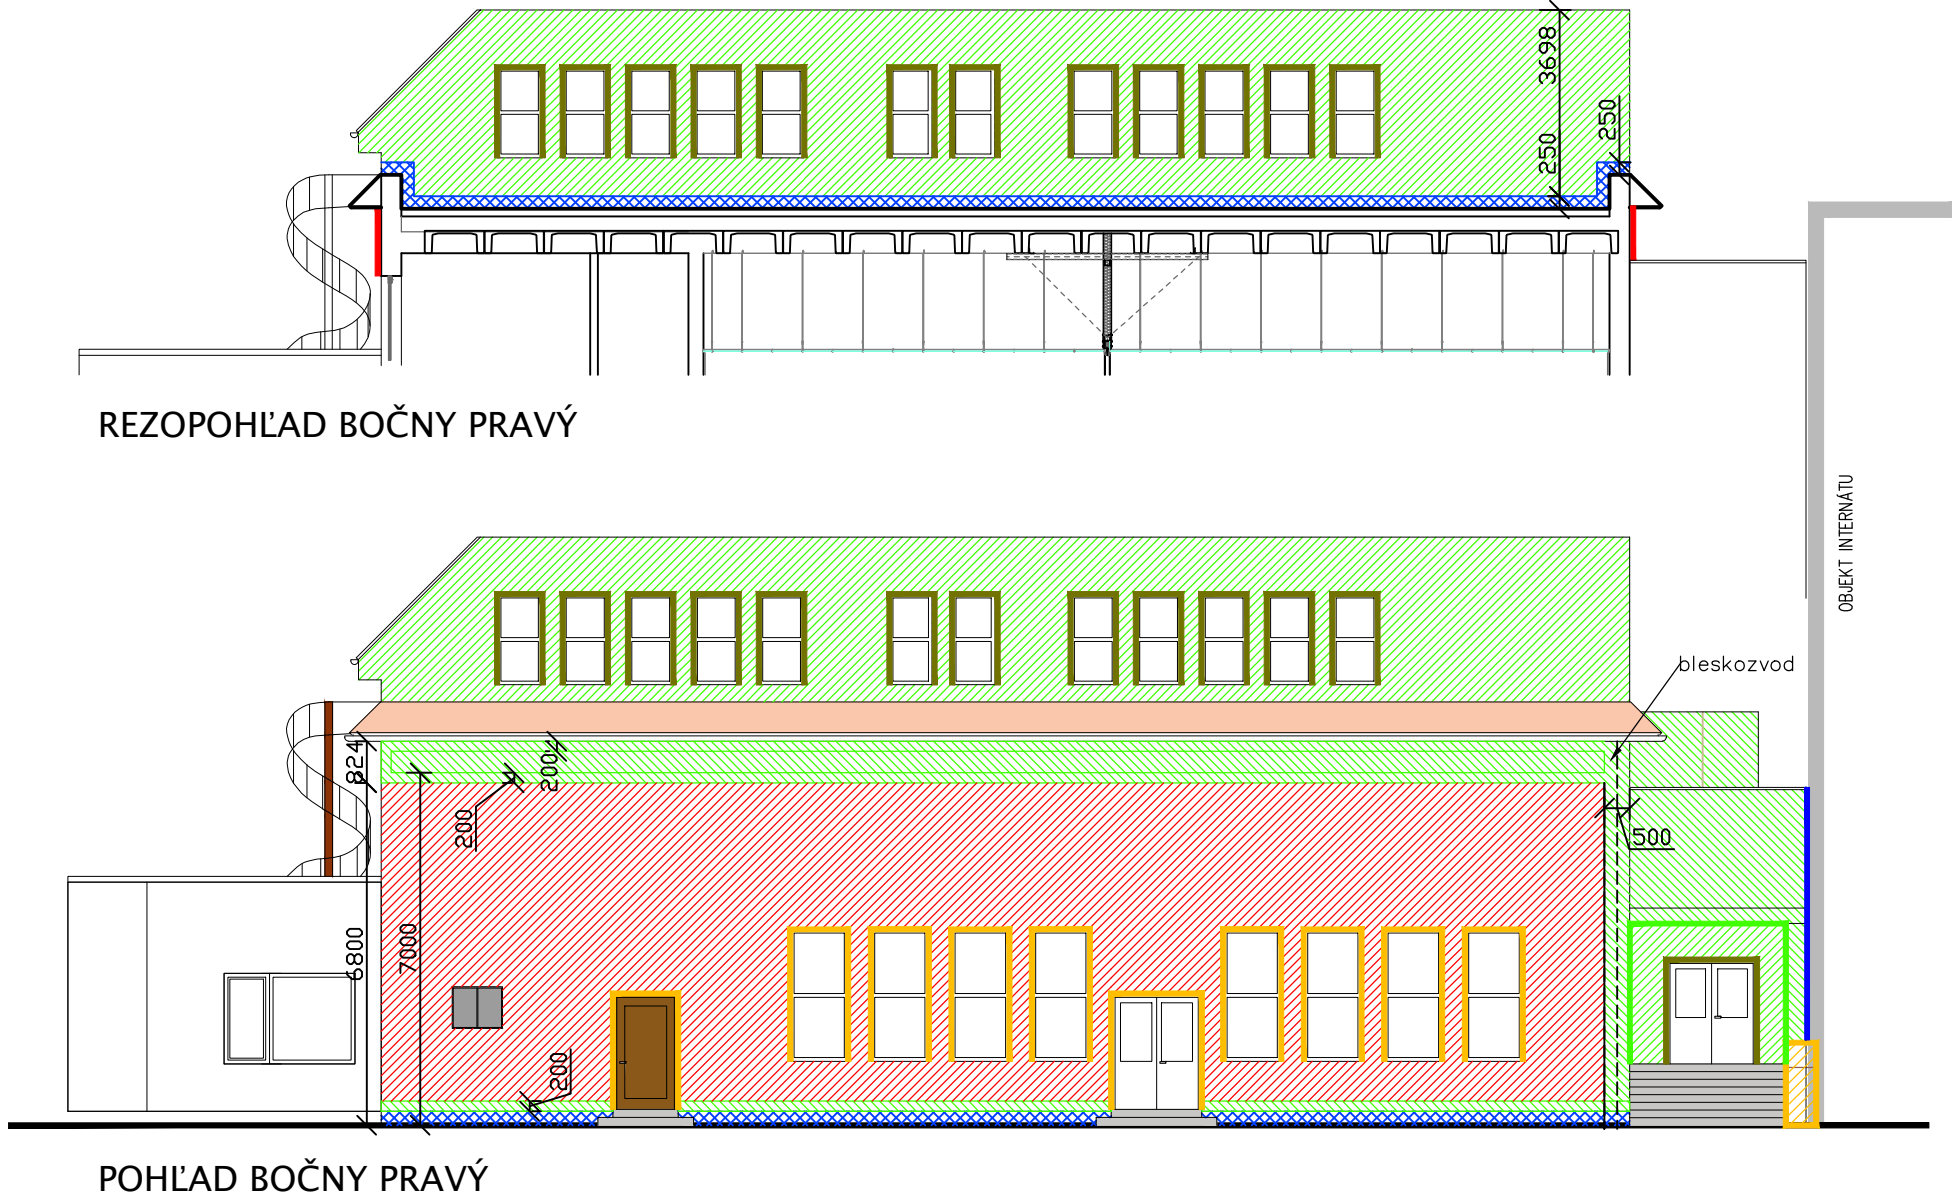


REZOPOHĽAD BOČNY PRAVÝ

POHĽAD BOČNY PRAVÝ

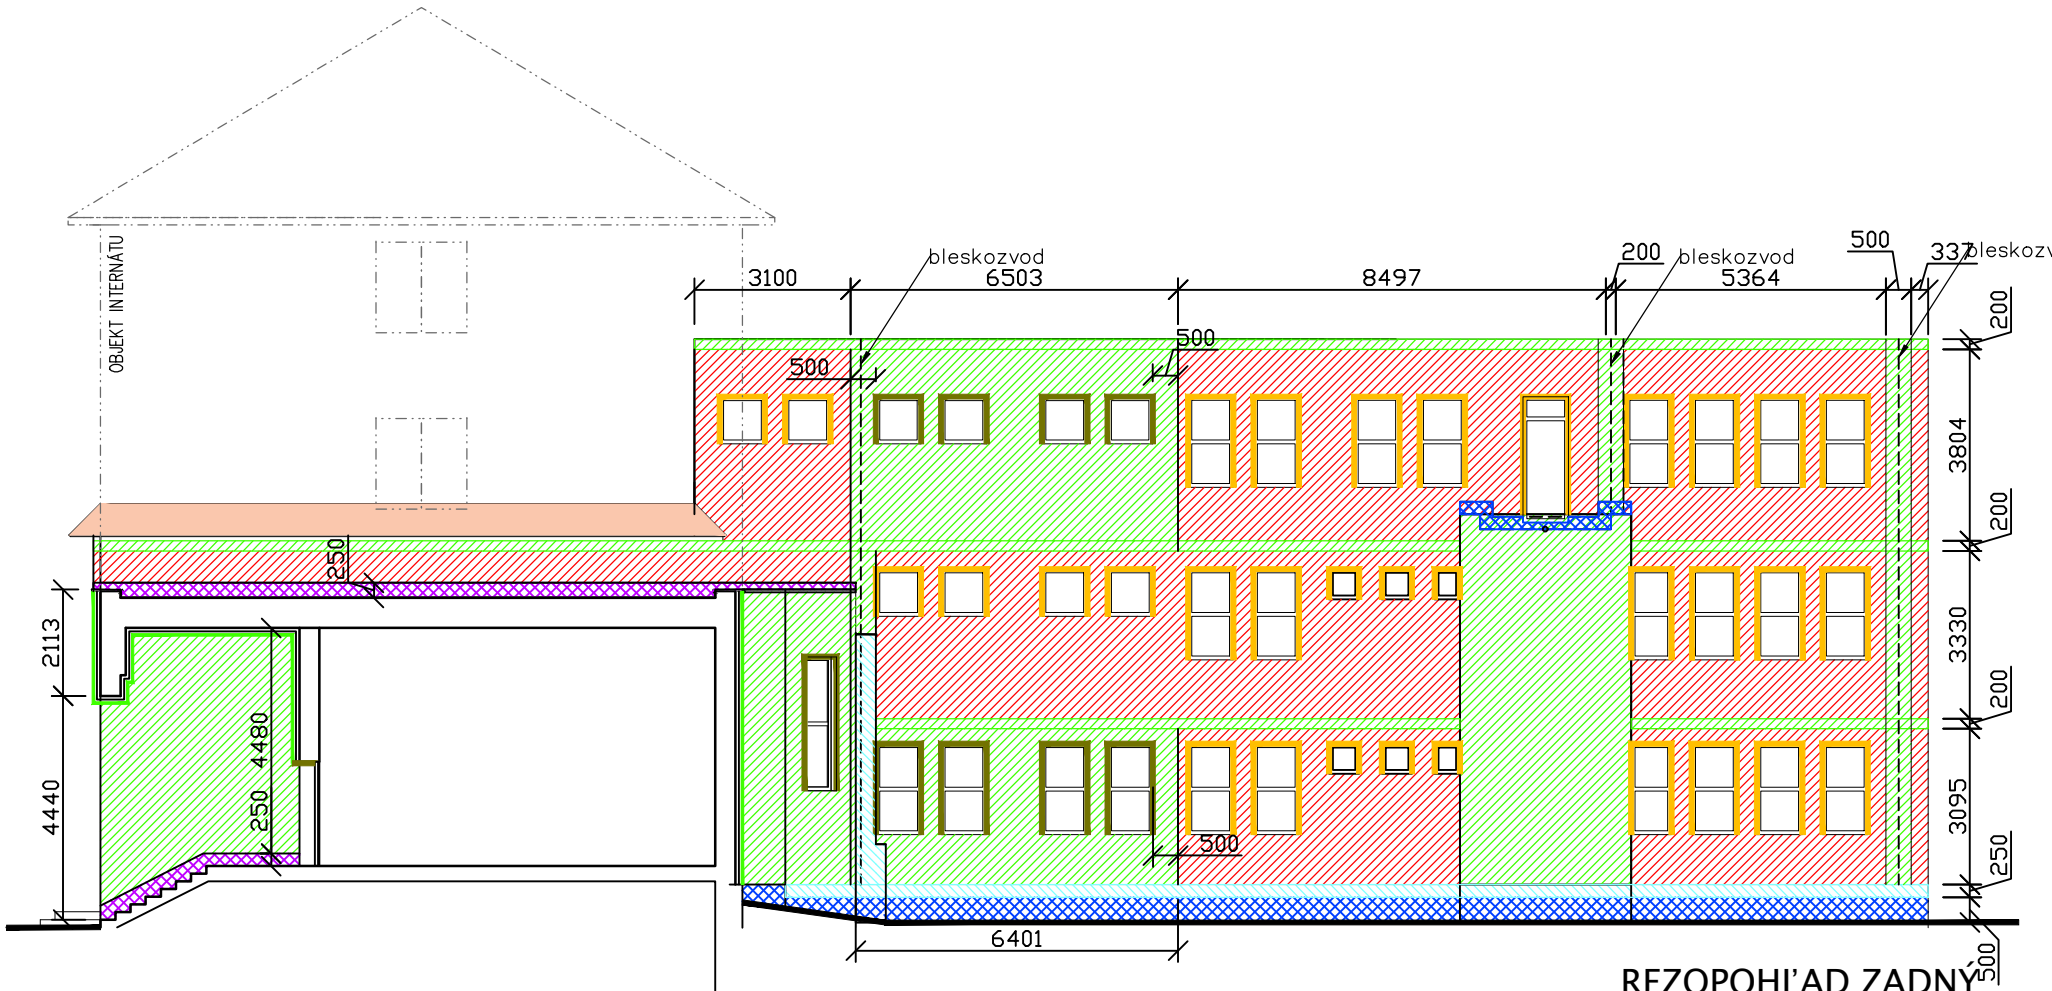


REZOPOHĽAD ZADNÝ

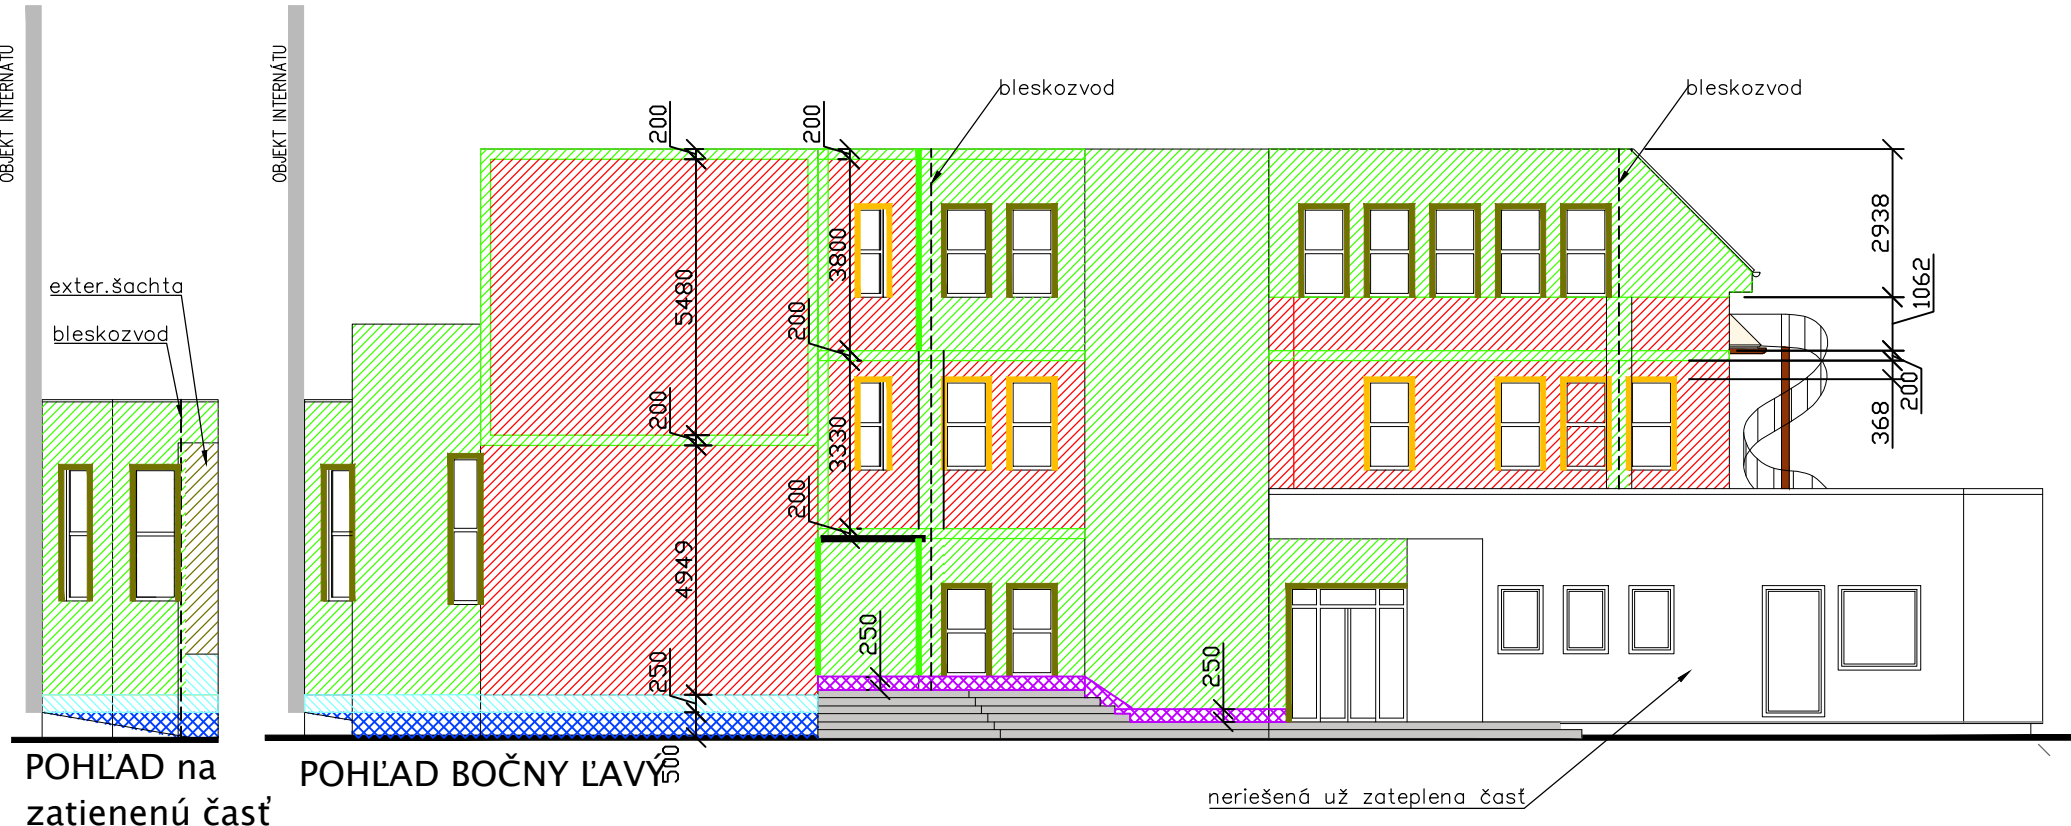

POHĽAD na zatienenú časť

POHĽAD BOČNY ĽAVÝ

neriešená už zateplena časť

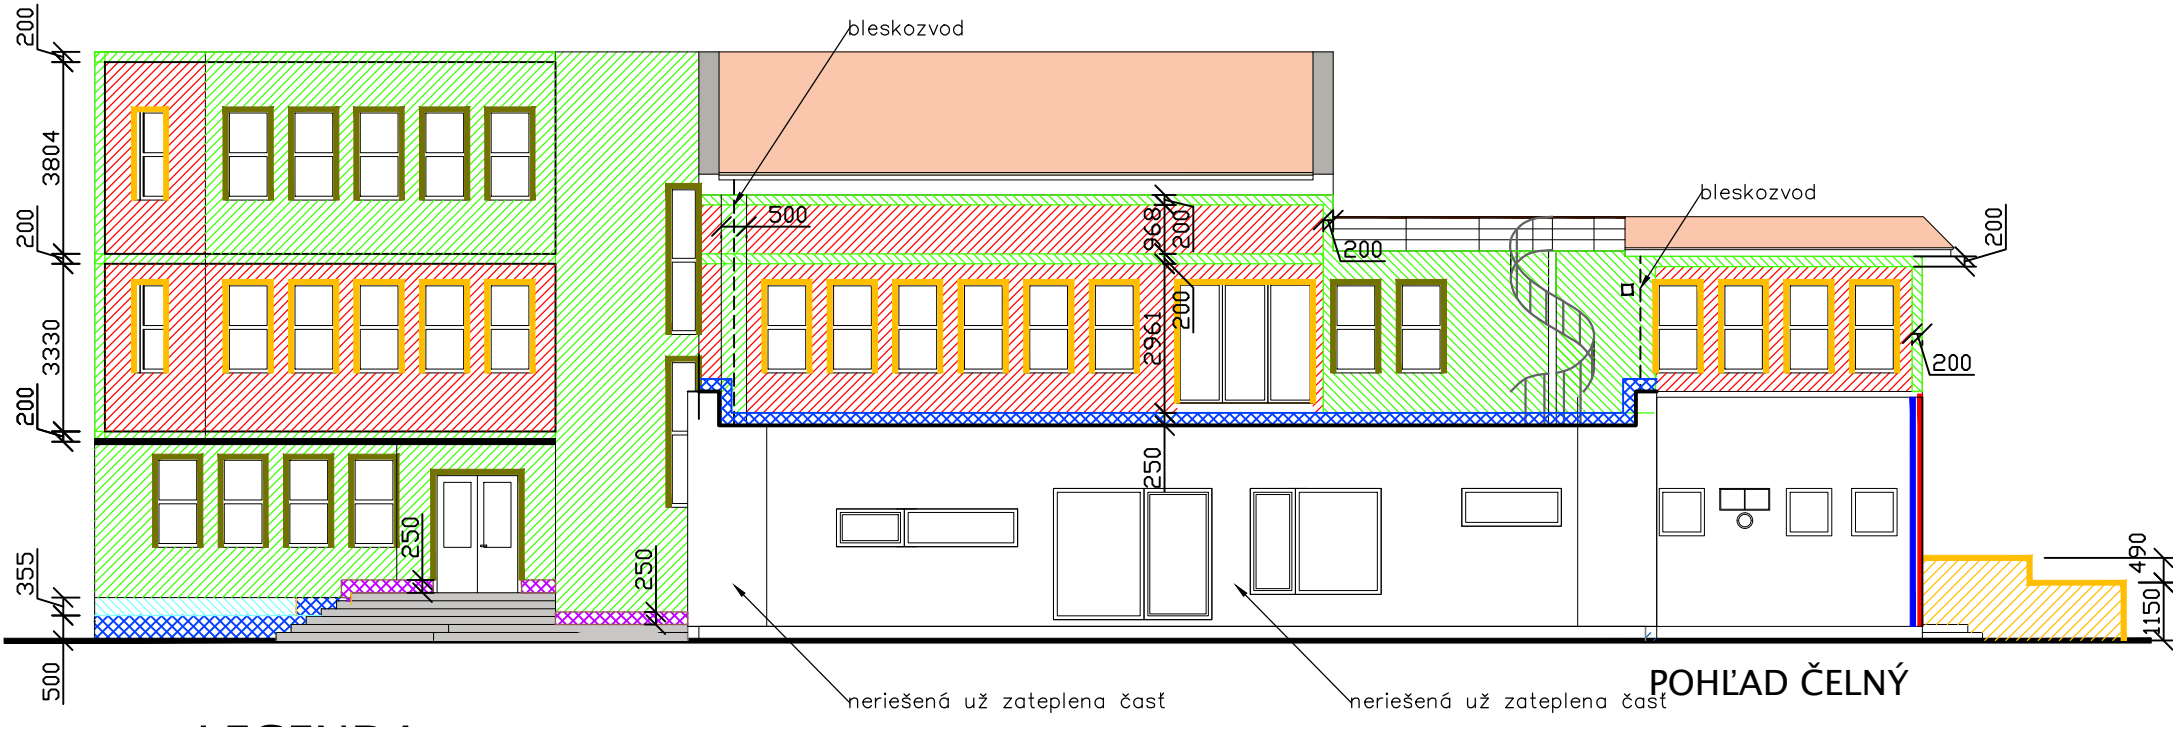

POHĽAD ČELNÝ

neriešená už zateplena časť

neriešená už zateplena časť

LEGENDA

- PLATNE TEPELNEJ IZOLÁCIE TRIEDY REAKCIE NA OHEŇ ASPOŇ A2-s1, d0 (napr.STYRCON alt. MINERÁLNA VLNA) HR.100mm
- PLATNE Z TVRDENEJ IZOLÁCIE (napr.STYRODUR alt. EXTRUD.POLYSTYRÉN), HR.140MM
- PLATNE Z TVRDENEJ IZOLÁCIE (napr.STYRODUR alt. EXTRUD.POLYSTYRÉN), HR.100MM
- PLATNE Z POLYSTYRÉNU EPS 70F, HR.140MM
- PLATNE TEPELNEJ IZOLÁCIE TRIEDY REAKCIE NA OHEŇ ASPOŇ A2-s1, d0 (napr.STYRCON alt. MINERÁLNA VLNA) HR.140mm
- PLATNE TEPELNEJ IZOLÁCIE TRIEDY REAKCIE NA OHEŇ ASPOŇ A2-s1, d0 (napr.STYRCON alt. MINERÁLNA VLNA) HR.220mm
- PLATNE Z TVRDENEJ IZOLÁCIE (napr.STYRODUR alt. EXTRUD.POLYSTYRÉN), HR.30MM
- PLATNE Z TRIEDY REAKCIE NA OHEŇ ASPOŇ A2-s1, d0 (napr.STYRCON alt. MINERÁLNA VLNA) HR.30MM
- DILATÁCIA-TMEL

	ZODP.PROJEKTANT	VYPRACOVAL	KRESLIL	K2 ateliér S.r.o. Dlhá 16, 949 01 Nitra, 0908-778 761 0911-778 761
	ING. ARCH. R. KOČAJDA	ING. ARCH. R. KOČAJDA	ING. JURAJ PAVLOVÍČ	
	STAVEBNÍK: Univerzita Konštantína Filozofa v Nitre, Tr. Andreja Hlinku 1, Nitra, PSČ 949 74, SR			
	AKCIA: Zníženie energetickej náročnosti budovy spoločenskej prístavby ŠD UKF Zobor, Dražovská 2, Nitra K.U. Zobor, parc.č. 4594/2			
VÝKRES:	POHĽADY-FIGURY			DÁTUM: 08/2018
				STUPEŇ: PROJEKT
				FORMÁT: A4
				MIERKA: 1:150
				VÝKRES ČÍSLO: 06