



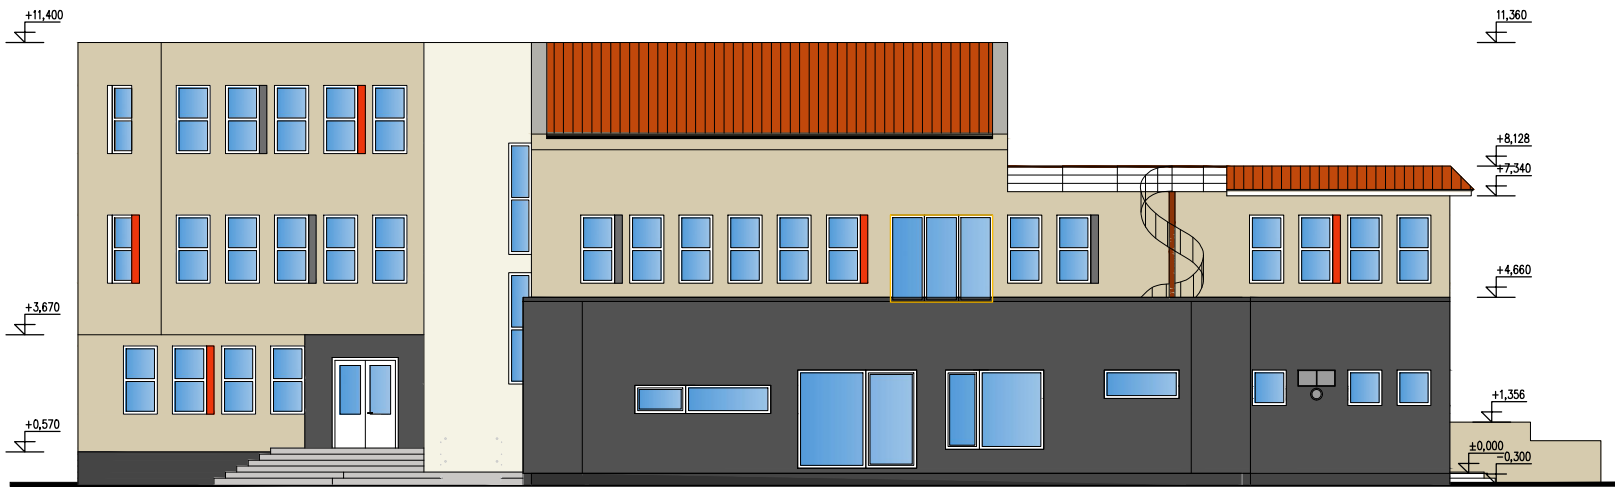

POHĽAD ČELNÝ

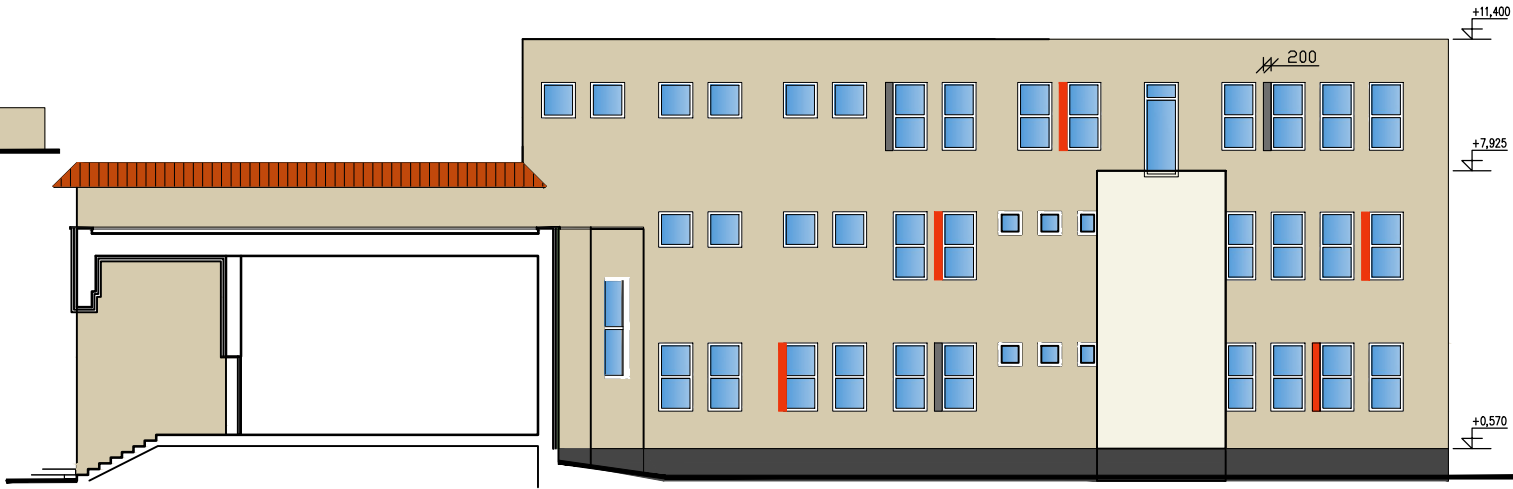

POHĽAD BOČNÝ ĽAVÝ




REZOPOHĽAD ZADNÝ

LEGENDA

- omietka BAUMIT – LIFE 0395
- omietka BAUMIT – LIFE 0398
- omietka BAUMIT – LIFE 0521
- omietka BAUMIT – LIFE 0442

UPOZORNENIE:

- REÁLNE ROZMERY PRED REALIZÁCIOU PREMERAŤ A PREKONTROLOVAŤ PRIAMO NA STAVBE !!!
- AK SA VYSKYTNÚ NOVÉ SKUTOČNOSTI, KTORÉ MAJÚ VPLYV NA REALIZÁCIU STAVBY, PROJEKTANT SI VYHRADZUJE PRÁVO NA ZMENU PROJEKTU POČAS REALIZÁCIE.
- STATIK SI VYHRADZUJE PRÁVO NA ZMENU PROJEKTOVEJ DOKUMENTÁCIE POČAS REALIZÁCIE AJ Z INÝCH VEČNÝCH DOVODOV V ZÁUJME DOSIAHNUTIA VAČŠEJ BEZPEČNOSTI STAVBY.
- KONŠTRUKCIE, KTORÉ NIE SÚ ZAZNAČENÉ VO VÝKRESOVEJ DOKUMENTÁCII SA BLIŽŠIE ŠPECIFIKUJÚ POČAS REALIZÁCIE.
- PRI VÝSTAVBE JE NUTNÉ DODRŽAŤ VŠETKY PREDPISY A ŠPECIFIKÁCIE PODLA NARIADENÍ VÝROBCOV MATERIÁLOV A PRVKOV, KTORÉ NIE SÚ V PROJEKTE BLIŽŠIE ŠPECIFIKOVANÉ.
- PRI NEŠPECIFIKOVANÍ KRITÉRIÍ JE NUTNÉ DODRŽAŤ ZÁKONY, TECHNICKÉ NORMY A PREDPISY, PRIČOM ROZMERY MÚROV SÚ KÓTOVANÉ S VÝROBNÝMI ROZMERMÍ KUSOVÝCH STAVIV.

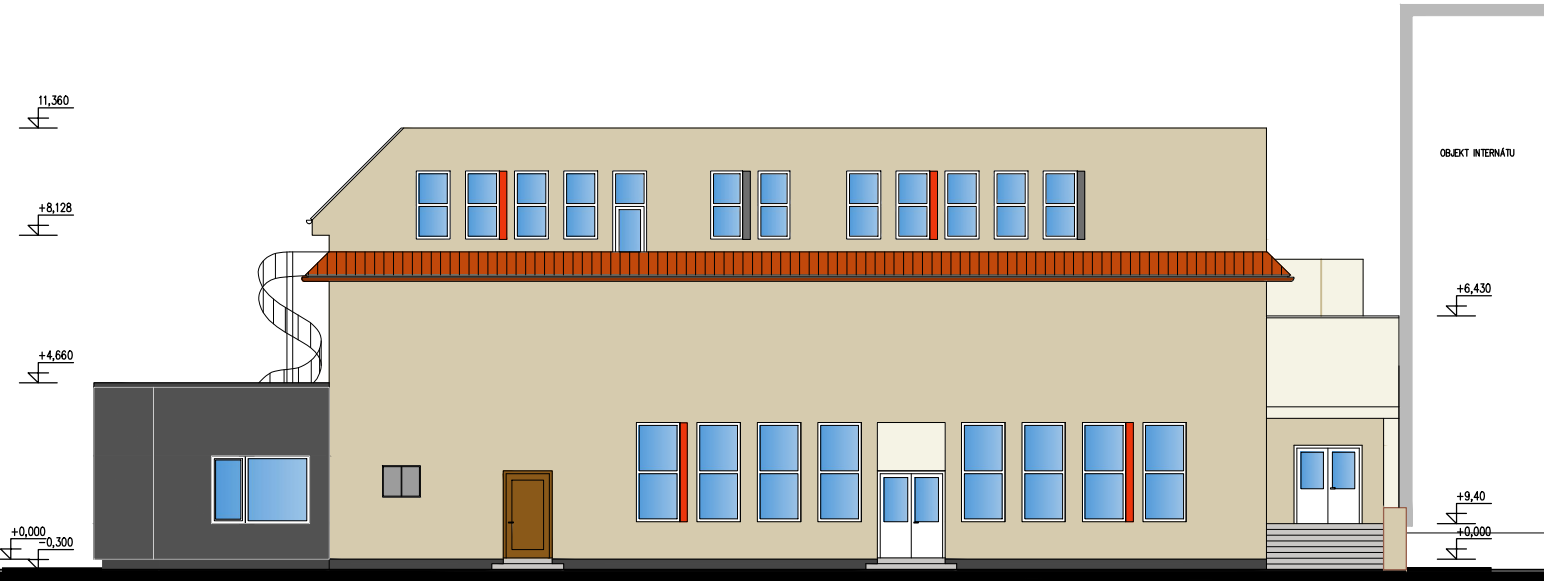

POHĽAD ČELNÝ

ZODP.PROJEKTANT	VYPRACOVAL	KRESLIL	K2 Dlhá 16, 949 01 Nitra, 0908-778 761 0911-778 761 ateliér s.r.o.	
ING. ARCH. R. KOČAJDA	ING. ARCH. R. KOČAJDA	ING. JURAJ PAVLOVIČ		
STAVEBNÍK: Univerzita Konštantína Filozofa v Nitre, Tr. Andreja Hlinku 1, Nitra, PSČ 949 74, SR			DÁTUM:	10/2018
AKCIA: Zníženie energetickej náročnosti budovy spoločenskej prístavby ŠD UKF Zobor, Dražovská 2, Nitra K.U. Zobor, parc.č. 4594/2			STUPEŇ:	PROJEKT
			FORMÁT:	2xA4
VÝKRES: POHĽADY			MIERKA:	VÝKRES ČÍSLO:
			1:200	07