


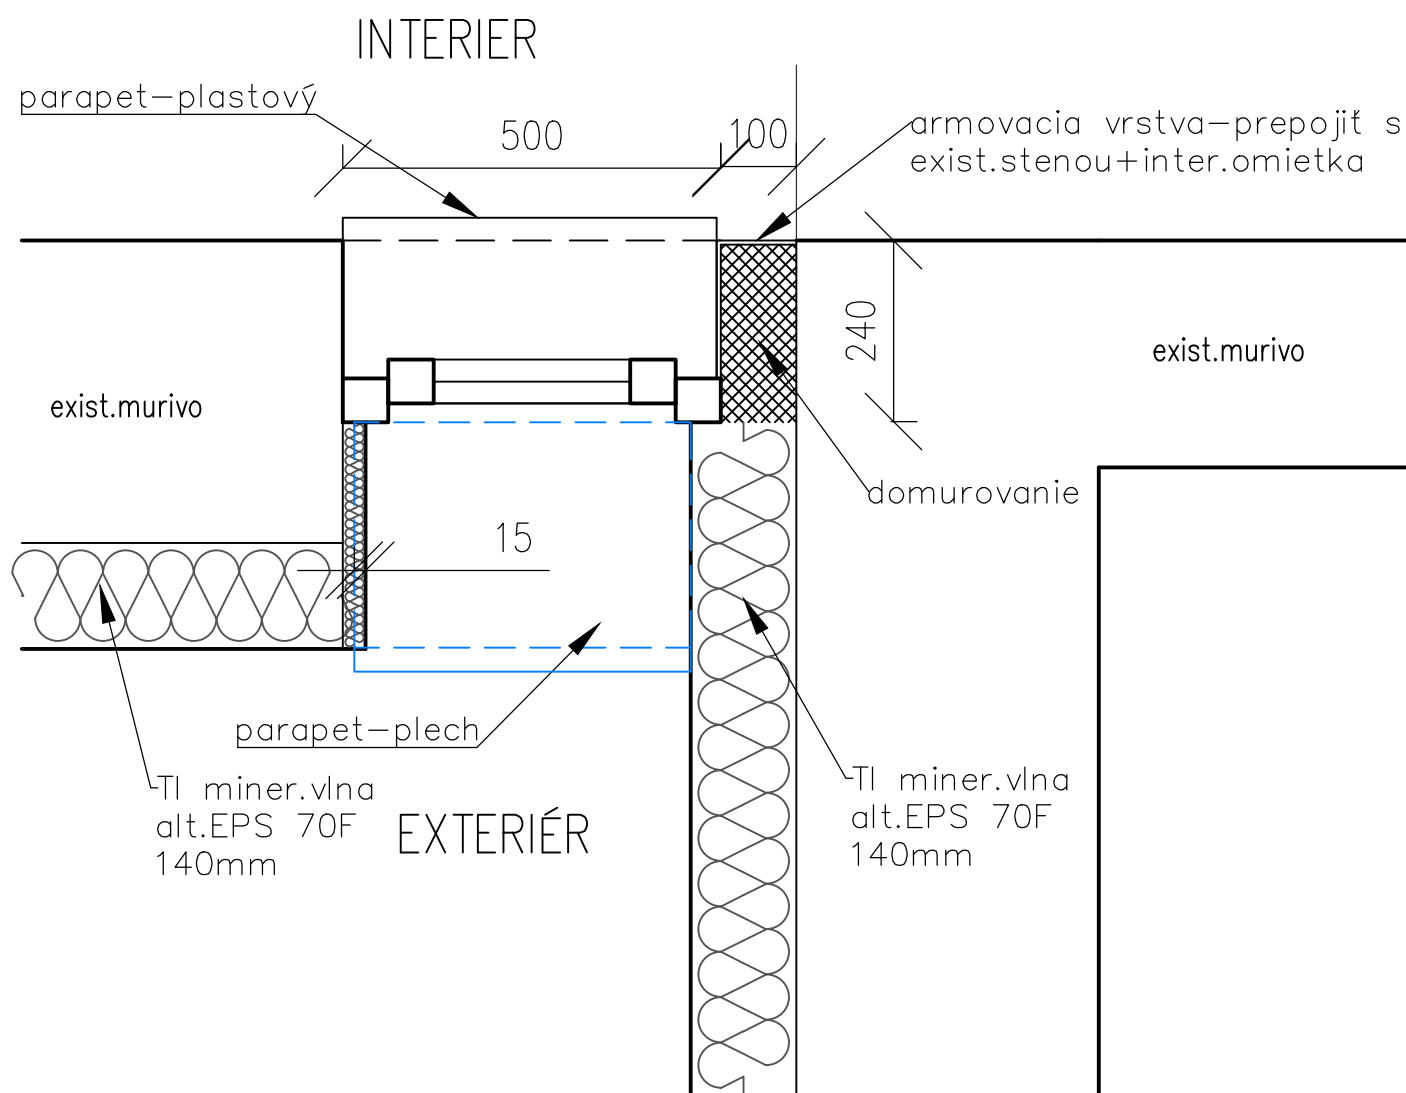

ZODPOVEDNÝ PROJEKTANT: ING. ARCH. R. KOČAJDA

VYPRACOVAL: ING.ARCH.M.KOČAJDOVÁ

DETAIL 1-DOMUROVANIE OSTENIA

STRANA

01

MIERKA