


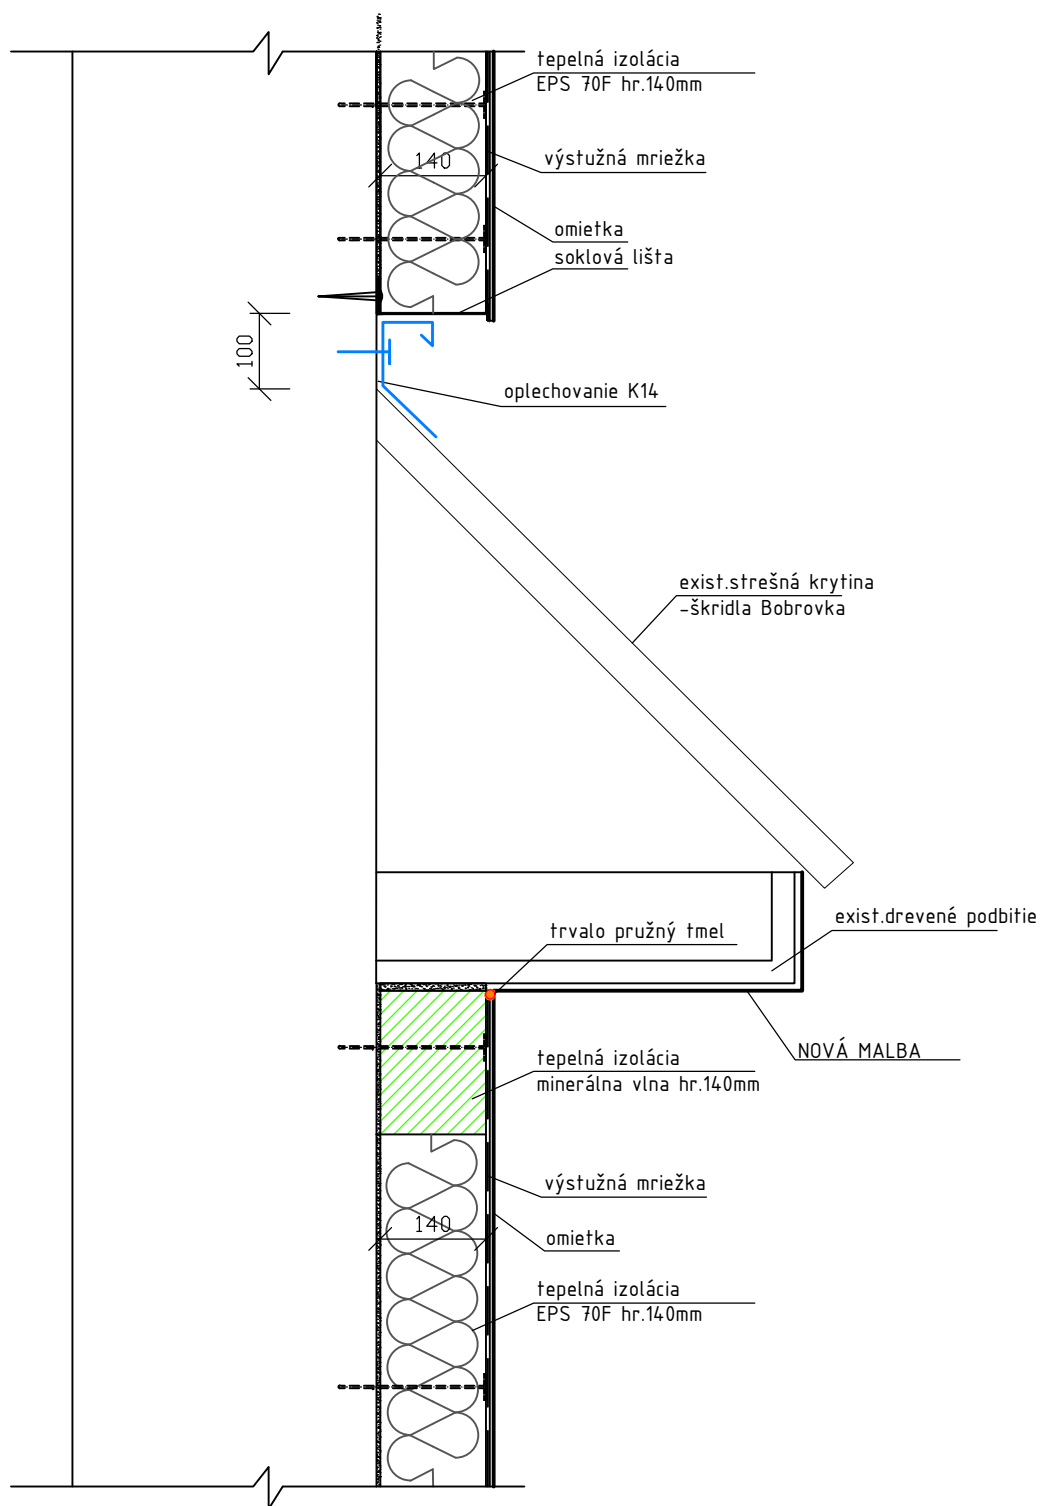

ZODPOVEDNÝ PROJEKTANT: ING. ARCH. R. KOČAJDA

VYPRACOVAL: ING.ARCH.M.KOČAJDOVÁ

DETAIL ZATEPLENIA PRI STYKU STRIEŠKY A STENY

STRANA

02

MIERKA