


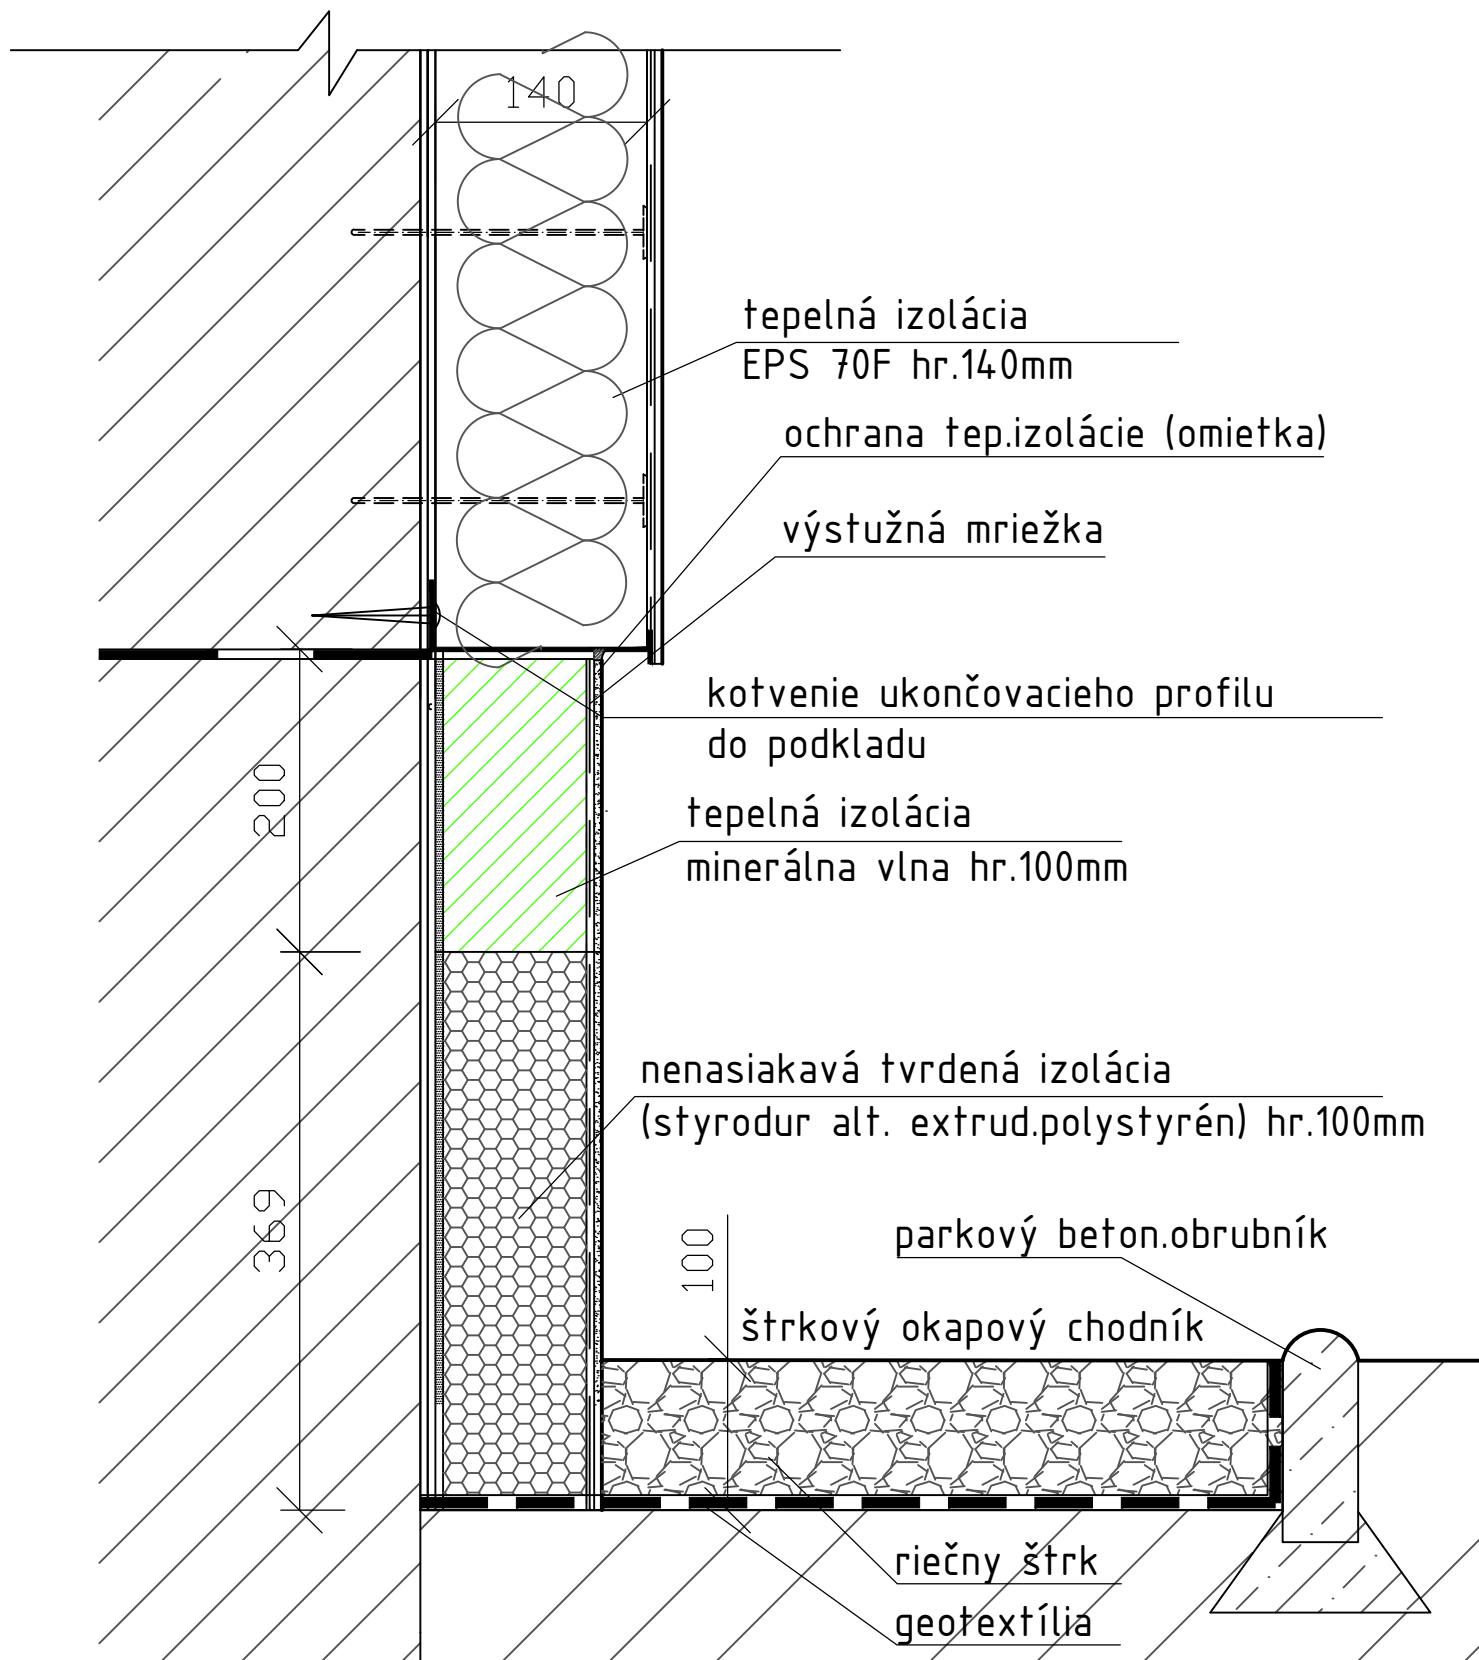

ZODPOVEDNÝ PROJEKTANT: ING. ARCH. R. KOČAJDA

VYPRACOVAL: ING.ARCH.M.KOČAJDOVÁ

DETAIL UKONČENIA SOKLA-ŠTRKOVÝ CHODNÍK

STRANA

MIERKA

04