


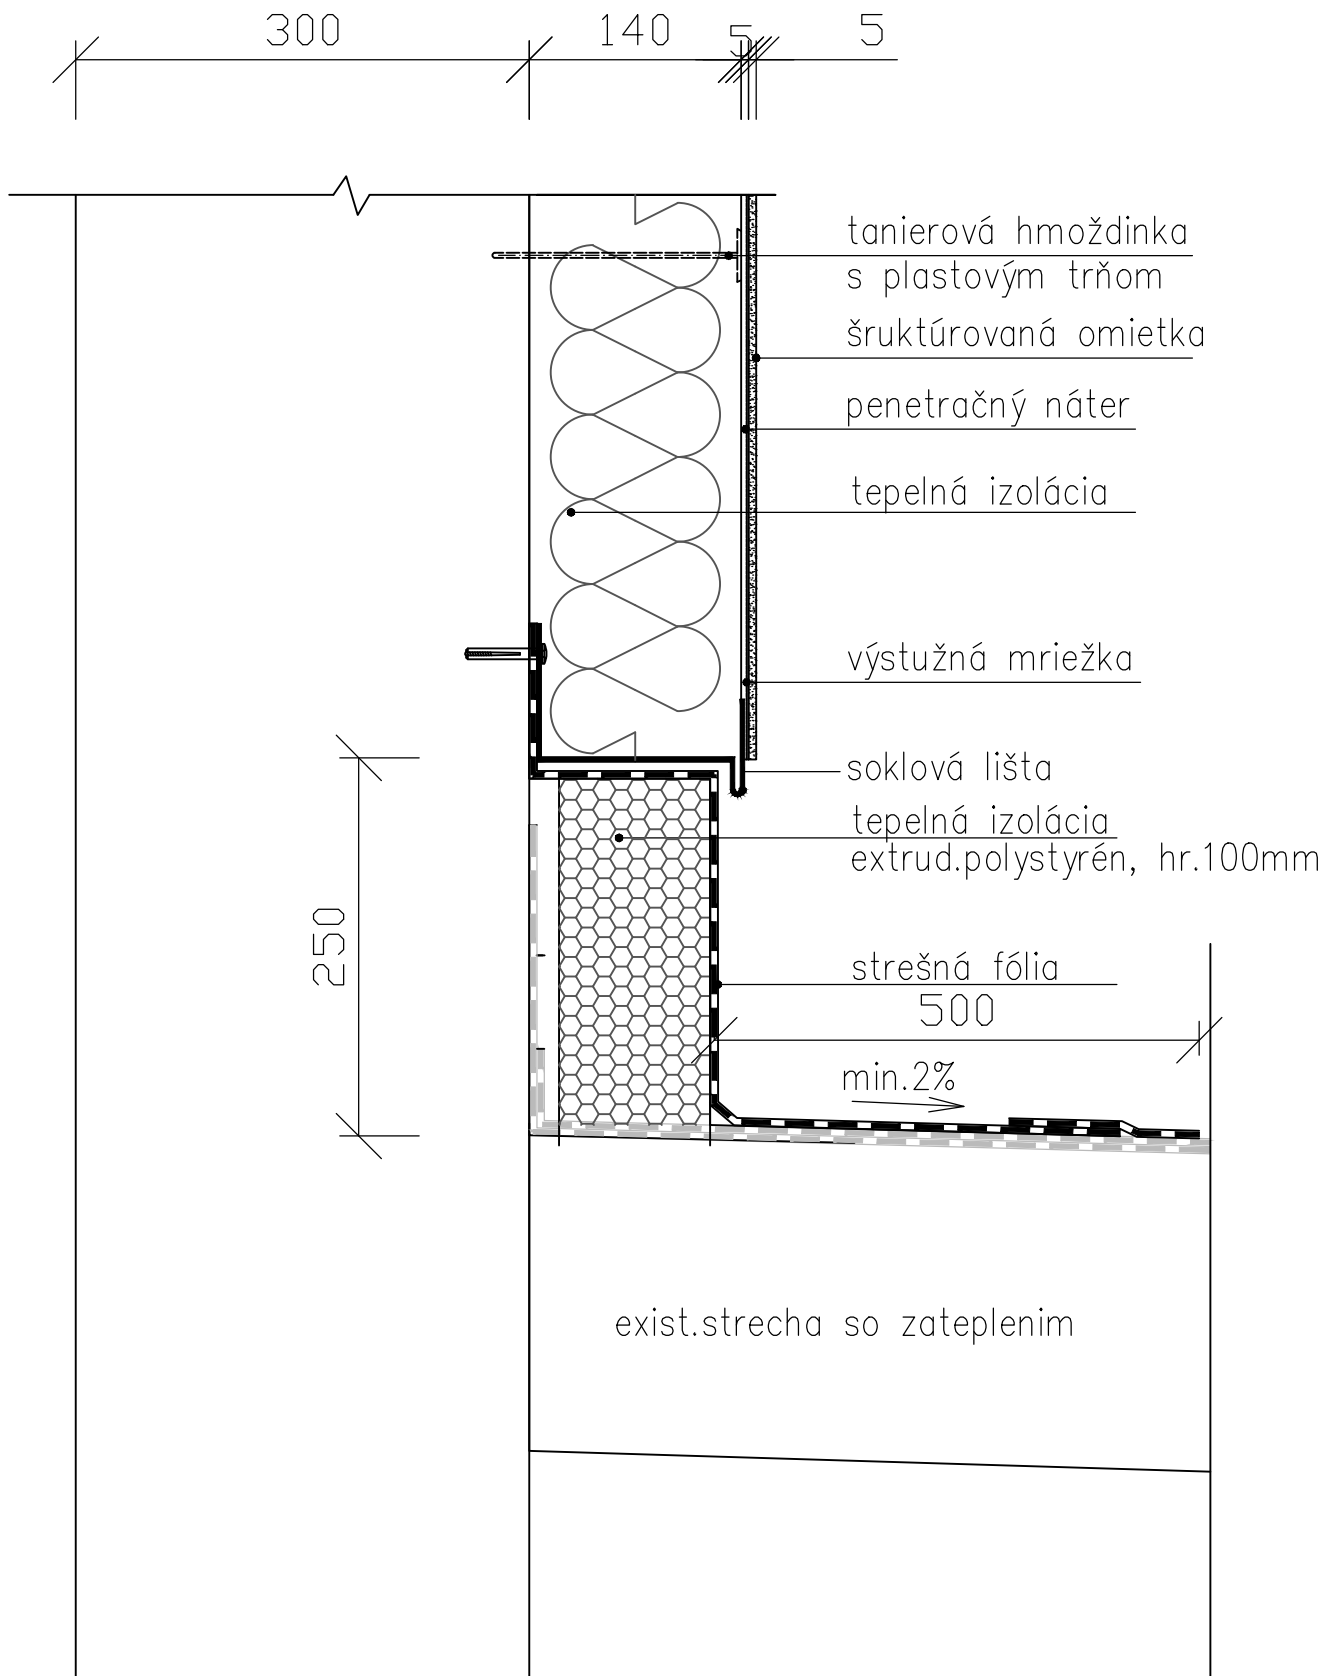

ZODPOVEDNÝ PROJEKTANT: ING. ARCH. R. KOČAJDA

VYPRACOVAL: ING.ARCH.M.KOČAJDOVÁ

DETAIL ZATEPLENIA STENY PRI PLOCHEJ STECHE

STRANA

MIERKA

05