


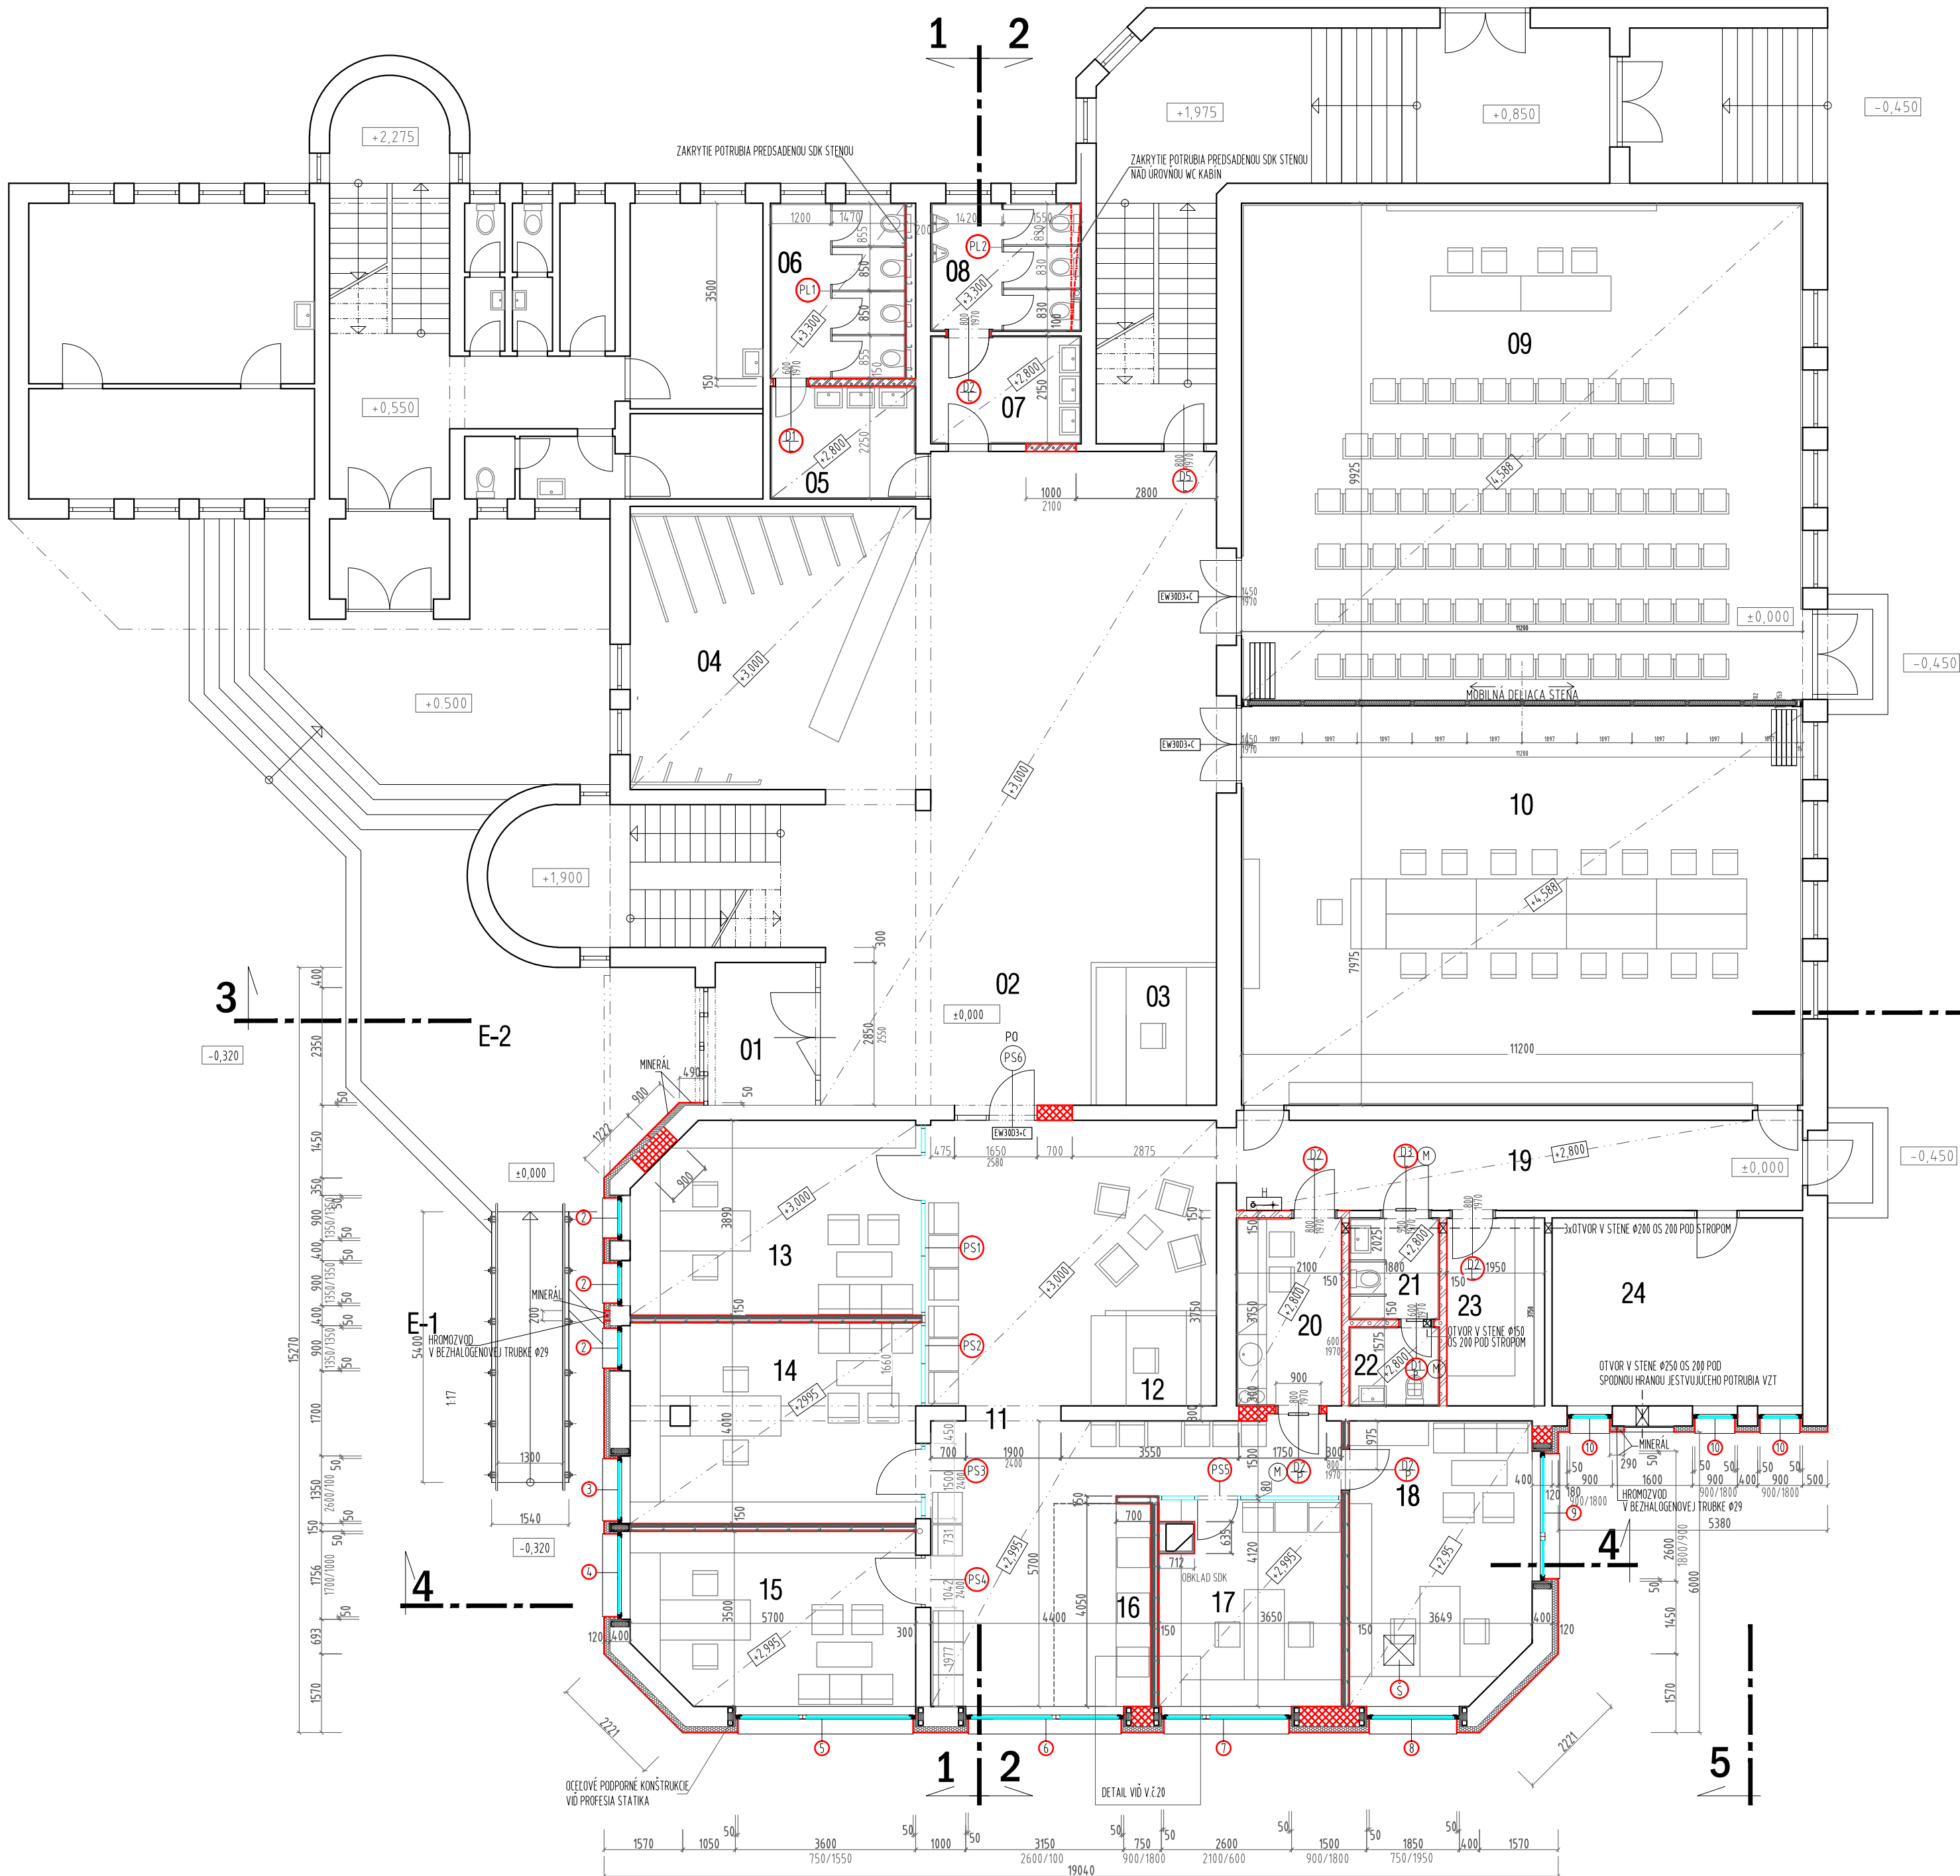

LEGENDA RIEŠENÝCH MIESTNOSTI

Č.M.	NÁZOV MIESTNOSTI	PLOCHA m ²	JESTVUJÚCI STAV			NAVRHOVANÉ ÚPRAVY			
						PODLAHA			
			PODLAHA	STENY	STROP	PRÍPRAVA PODKLADU	NOVÁ PODLAHA	STENY	STROP
E-1	RAMPA	8,32						BETÓNOVÁ PLOCHA, STROMBOUVANÝ POVRCH MALOVÉ LAKY, LEPKOVÁ MALTA, TRASOVIA 45 mm 20 mm 200 mm 200 mm	ZÁKLADNÉ ÚPRAVY PRE MOBILNÝCH
E-2	VÝSTUPNÁ PLOCHA	35,60	ZAKLADENÝ BETÓN			VYŠKŤOVANÉ ÚPRAVY PRE MAPOVANÉ RAMPY PREŠKŤOVANÉ	PERFOROVANÝ BETÓN OBRÁNKY NA TŤ		
01	ZÁČERIE	6,05	KERAMICKÁ DLAŽBA	OMIEKTA, MALOVKA	KAZETOVÝ PODHĽAD				
02	FOYER	88,30	KERAMICKÁ DLAŽBA		KAZETOVÝ PODHĽAD			VÝŠKŤOVANÁ OMIEKTOVÁ PO ELEKTRONICÁLII ELEKTRONICÁLII, ZÁKRYTIE DIVERZ OMIEKTA NA DOKUROVANÉ ČASTI MALOVKA	
03	RECEPCIA	6,60	KERAMICKÁ DLAŽBA		KAZETOVÝ PODHĽAD			VÝŠKŤOVANÁ OMIEKTOVÁ PO ELEKTRONICÁLII MALOVKA	
04	ŠATŤA	27,86	KERAMICKÁ DLAŽBA		KAZETOVÝ PODHĽAD				
05	WC ŽENY PREDSEŤ	6,52	KERAMICKÁ DLAŽBA	KERAMICKÝ OBRÁD		- NIVELIZAČNÁ IMPISTA 5 mm - VYŠKŤOVANÉ PODKLADU - POTIER 10 mm - VYŠKŤOVANÉ KERAMICKÉ DLAŽBY A CEMENTOVÉHO POTIERU DO HRÁDKY 75 mm	- DLAŽBA GREŠ - DLAŽBA PRÁDNY TPEL ADEK CA 20P CEA 5 mm/s - ŠARHŤOVANÁ ADEK GR - 0,3 kg/m ² - LEPIDLO ADEK XTG - 14 kg/m ²	DEMONTÁŽ KERAMICKÝCH OPRAVA PODKLADU POD NOVÝ KERAMICKÝ OBRÁD	KAZETOVÝ PODHĽAD
06	WC ŽENY	9,38	KERAMICKÁ DLAŽBA	KERAMICKÝ OBRÁD		- NIVELIZAČNÁ IMPISTA 5 mm - VYŠKŤOVANÉ PODKLADU - POTIER 10 mm - VYŠKŤOVANÉ KERAMICKÉ DLAŽBY A CEMENTOVÉHO POTIERU DO HRÁDKY 75 mm	- DLAŽBA GREŠ - DLAŽBA PRÁDNY TPEL ADEK CA 20P CEA 5 mm/s - ŠARHŤOVANÁ ADEK GR - 0,3 kg/m ² - LEPIDLO ADEK XTG - 14 kg/m ²	VÝŠKŤOVANÉ KERAMICKÉ OBRÁD OBRÁDNY PRE REZERVY 2. Ú. A. ELEKTRON. OPRAVA PODKLADU POD NOVÝ KERAMICKÝ OBRÁD ZAKRYTIE POTRUBIA PREDAJENOU SOK STENOU NOVÝ KERAMICKÝ OBRÁD	KAZETOVÝ PODHĽAD
07	WC MUŽI PREDSEŤ	6,45	KERAMICKÁ DLAŽBA	KERAMICKÝ OBRÁD		- NIVELIZAČNÁ IMPISTA 5 mm - VYŠKŤOVANÉ PODKLADU - POTIER 10 mm - VYŠKŤOVANÉ KERAMICKÉ DLAŽBY A CEMENTOVÉHO POTIERU DO HRÁDKY 75 mm	- DLAŽBA GREŠ - DLAŽBA PRÁDNY TPEL ADEK CA 20P CEA 5 mm/s - ŠARHŤOVANÁ ADEK GR - 0,3 kg/m ² - LEPIDLO ADEK XTG - 14 kg/m ²	DEMONTÁŽ KERAMICKÝCH OPRAVA PODKLADU POD NOVÝ KERAMICKÝ OBRÁD	KAZETOVÝ PODHĽAD
08	WC MUŽI	7,96	KERAMICKÁ DLAŽBA	KERAMICKÝ OBRÁD		- NIVELIZAČNÁ IMPISTA 5 mm - VYŠKŤOVANÉ PODKLADU - POTIER 10 mm - VYŠKŤOVANÉ KERAMICKÉ DLAŽBY A CEMENTOVÉHO POTIERU DO HRÁDKY 75 mm	- DLAŽBA GREŠ - DLAŽBA PRÁDNY TPEL ADEK CA 20P CEA 5 mm/s - ŠARHŤOVANÁ ADEK GR - 0,3 kg/m ² - LEPIDLO ADEK XTG - 14 kg/m ²	VÝŠKŤOVANÉ KERAMICKÉ OBRÁD OBRÁDNY PRE REZERVY 2. Ú. A. ELEKTRON. OPRAVA PODKLADU POD NOVÝ KERAMICKÝ OBRÁD ZAKRYTIE POTRUBIA PREDAJENOU SOK STENOU NOVÝ KERAMICKÝ OBRÁD	KAZETOVÝ PODHĽAD
09	KONFERENČNÁ SÁLA	111,16	KERAMICKÁ DLAŽBA	OBRÁD KOMPOTNÝMI DOSKAMI	KAZETOVÝ PODHĽAD			BEZ ÚPRAV	DEMONTÁŽ KAZETOVÉHO PODKLADU MONTÁŽ OCELIOVÝCH KONSTRUKCI MOBILNÝCH ELEKTRONICÁLII
10	KONFERENČNÁ SÁLA ŠTUDENTSKÝ PARLAMENT	88,31	KERAMICKÁ DLAŽBA	OBRÁD KOMPOTNÝMI DOSKAMI	KAZETOVÝ PODHĽAD			BEZ ÚPRAV	DEMONTÁŽ KAZETOVÉHO PODKLADU MONTÁŽ OCELIOVÝCH KONSTRUKCI MOBILNÝCH ELEKTRONICÁLII
11	HALA	51,92	KERAMICKÁ DLAŽBA	OMIEKTA POŠKODENÁ FARBAMI	OMIEKTA POŠKODENÁ FARBAMI ZÁVERŠENÁ OCELIOVÁ KONSTRUKCIA	- NIVELIZAČNÁ IMPISTA 10 mm - ADEKOVÝ MOSTIK 1 mm - ČISTENIE, LITOPHIN KF GRUNDRINGER - 8,3 kg/m ²	- LAMINÁTOVÁ PLOCHA TREDA ŽŤAŽE AC 4/33 8 mm - PODLAHA POD PĽAVÁJUCE PODLAHY 7 mm	VYŠKŤOVANÉ ÚPRAVY PRE DIVERZ STAVENÉ ÚPRAVY PRE ELEKTRONICÁLII NOVÁ OMIEKTA - MALOVKA	ELEKTRONICÁLII MONTÁŽ OCELIOVÝCH KONSTRUKCI MOBILNÝCH ELEKTRONICÁLII NOVÝ KAZETOVÝ PODHĽAD A ÚPRAVY PRE SVETLO A VÝŠKŤY VŤ DO PODHĽADU
12	INFORMÁCIE	4,50	KERAMICKÁ DLAŽBA			- NIVELIZAČNÁ IMPISTA 10 mm - ADEKOVÝ MOSTIK 1 mm - ČISTENIE, LITOPHIN KF GRUNDRINGER - 8,3 kg/m ²	- LAMINÁTOVÁ PLOCHA TREDA ŽŤAŽE AC 4/33 8 mm - PODLAHA POD PĽAVÁJUCE PODLAHY 7 mm	Z DVOCH STRÁN INTERIOVÉHO PRŮVY STAVENÉ ÚPRAVY PRE ELEKTRONICÁLII NOVÁ OMIEKTA - MALOVKA	ELEKTRONICÁLII MONTÁŽ OCELIOVÝCH KONSTRUKCI MOBILNÝCH ELEKTRONICÁLII NOVÝ KAZETOVÝ PODHĽAD A ÚPRAVY PRE SVETLO DO PODHĽADU
13	MANAŽÉR	21,38	KERAMICKÁ DLAŽBA	OMIEKTA POŠKODENÁ FARBAMI	OMIEKTA POŠKODENÁ FARBAMI	- NIVELIZAČNÁ IMPISTA 10 mm - ADEKOVÝ MOSTIK 1 mm - ČISTENIE, LITOPHIN KF GRUNDRINGER - 8,3 kg/m ²	- LAMINÁTOVÁ PLOCHA TREDA ŽŤAŽE AC 4/33 8 mm - PODLAHA POD PĽAVÁJUCE PODLAHY 7 mm	VYŠKŤOVANÉ VONKAŠNÁ OBRÁD OBRÁDNY PRE REZERVY 2. Ú. A. ELEKTRON. OPRAVA PODKLADU POD NOVÝ KERAMICKÝ OBRÁD ZAKRYTIE POTRUBIA PREDAJENOU SOK STENOU NOVÝ KERAMICKÝ OBRÁD	ELEKTRONICÁLII MONTÁŽ OCELIOVÝCH KONSTRUKCI MOBILNÝCH ELEKTRONICÁLII NOVÝ KAZETOVÝ PODHĽAD A ÚPRAVY PRE SVETLO A VÝŠKŤY VŤ DO PODHĽADU
14	KONZULTÁCIE	22,64	KERAMICKÁ DLAŽBA	OMIEKTA POŠKODENÁ FARBAMI	OMIEKTA POŠKODENÁ FARBAMI	- NIVELIZAČNÁ IMPISTA 10 mm - ADEKOVÝ MOSTIK 1 mm - ČISTENIE, LITOPHIN KF GRUNDRINGER - 8,3 kg/m ²	- LAMINÁTOVÁ PLOCHA TREDA ŽŤAŽE AC 4/33 8 mm - PODLAHA POD PĽAVÁJUCE PODLAHY 7 mm	VYŠKŤOVANÉ VONKAŠNÁ OBRÁD OBRÁDNY PRE REZERVY 2. Ú. A. ELEKTRON. OPRAVA PODKLADU POD NOVÝ KERAMICKÝ OBRÁD ZAKRYTIE POTRUBIA PREDAJENOU SOK STENOU NOVÝ KERAMICKÝ OBRÁD	ELEKTRONICÁLII MONTÁŽ OCELIOVÝCH KONSTRUKCI MOBILNÝCH ELEKTRONICÁLII NOVÝ KAZETOVÝ PODHĽAD A ÚPRAVY PRE SVETLO DO PODHĽADU
15	KONZULTÁCIE	79,14	KERAMICKÁ DLAŽBA	OMIEKTA POŠKODENÁ FARBAMI	OMIEKTA POŠKODENÁ FARBAMI	6 sf - NIVELIZAČNÁ IMPISTA 10 mm - ADEKOVÝ MOSTIK 1 mm - ČISTENIE, LITOPHIN KF GRUNDRINGER - 8,3 kg/m ² 12 sf - VYŠKŤOVANÉ VÝŠKŤOVANÉ PODKLADU DO 10 mm VYŠKŤOVANÉ PODKLADU DO 10 mm	- LAMINÁTOVÁ PLOCHA TREDA ŽŤAŽE AC 4/33 8 mm - PODLAHA POD PĽAVÁJUCE PODLAHY 7 mm	VYŠKŤOVANÉ VONKAŠNÁ OBRÁD OBRÁDNY PRE REZERVY 2. Ú. A. ELEKTRON. OPRAVA PODKLADU POD NOVÝ KERAMICKÝ OBRÁD ZAKRYTIE POTRUBIA PREDAJENOU SOK STENOU NOVÝ KERAMICKÝ OBRÁD	ELEKTRONICÁLII MONTÁŽ OCELIOVÝCH KONSTRUKCI MOBILNÝCH ELEKTRONICÁLII NOVÝ KAZETOVÝ PODHĽAD A ÚPRAVY PRE SVETLO DO PODHĽADU
16	KOPÍRKY	1,85	KERAMICKÁ DLAŽBA	OMIEKTA POŠKODENÁ FARBAMI	OMIEKTA POŠKODENÁ FARBAMI	- NIVELIZAČNÁ IMPISTA 10 mm - ADEKOVÝ MOSTIK 1 mm - ČISTENIE, LITOPHIN KF GRUNDRINGER - 8,3 kg/m ²	- LAMINÁTOVÁ PLOCHA TREDA ŽŤAŽE AC 4/33 8 mm - PODLAHA POD PĽAVÁJUCE PODLAHY 7 mm	OPRAVA PRE ELEKTRONICÁLII NOVÁ OMIEKTA - MALOVKA	ELEKTRONICÁLII MONTÁŽ OCELIOVÝCH KONSTRUKCI MOBILNÝCH ELEKTRONICÁLII NOVÝ KAZETOVÝ PODHĽAD A ÚPRAVY PRE SVETLO DO PODHĽADU
17	KONZULTÁCIE	16,67	KERAMICKÁ DLAŽBA	OMIEKTA POŠKODENÁ FARBAMI	OMIEKTA POŠKODENÁ FARBAMI	- NIVELIZAČNÁ IMPISTA 10 mm - ADEKOVÝ MOSTIK 1 mm - ČISTENIE, LITOPHIN KF GRUNDRINGER - 8,3 kg/m ²	- LAMINÁTOVÁ PLOCHA TREDA ŽŤAŽE AC 4/33 8 mm - PODLAHA POD PĽAVÁJUCE PODLAHY 7 mm	VYŠKŤOVANÉ VONKAŠNÁ OBRÁD OBRÁDNY PRE REZERVY 2. Ú. A. ELEKTRON. OPRAVA PODKLADU POD NOVÝ KERAMICKÝ OBRÁD ZAKRYTIE POTRUBIA PREDAJENOU SOK STENOU NOVÝ KERAMICKÝ OBRÁD	ELEKTRONICÁLII MONTÁŽ OCELIOVÝCH KONSTRUKCI MOBILNÝCH ELEKTRONICÁLII NOVÝ KAZETOVÝ PODHĽAD A ÚPRAVY PRE SVETLO DO PODHĽADU
18	KANCELÁRIA	20,00	KERAMICKÁ DLAŽBA	OMIEKTA POŠKODENÁ FARBAMI	OMIEKTA POŠKODENÁ FARBAMI	- NIVELIZAČNÁ IMPISTA 10 mm - ADEKOVÝ MOSTIK 1 mm - ČISTENIE, LITOPHIN KF GRUNDRINGER - 8,3 kg/m ²	- LAMINÁTOVÁ PLOCHA TREDA ŽŤAŽE AC 4/33 8 mm - PODLAHA POD PĽAVÁJUCE PODLAHY 7 mm	VYŠKŤOVANÉ VONKAŠNÁ OBRÁD OBRÁDNY PRE REZERVY 2. Ú. A. ELEKTRON. OPRAVA PODKLADU POD NOVÝ KERAMICKÝ OBRÁD ZAKRYTIE POTRUBIA PREDAJENOU SOK STENOU NOVÝ KERAMICKÝ OBRÁD	ELEKTRONICÁLII MONTÁŽ OCELIOVÝCH KONSTRUKCI MOBILNÝCH ELEKTRONICÁLII NOVÝ KAZETOVÝ PODHĽAD A ÚPRAVY PRE SVETLO DO PODHĽADU
19	CHOUBA	28,34	PVC	OMIEKTA	OMIEKTA	- NIVELIZAČNÁ IMPISTA 10 mm - VYŠKŤOVANÉ PODKLADU - ODSŤAŽOVANIE PVC A NIVELITU	- LAMINÁTOVÁ PLOCHA TREDA ŽŤAŽE AC 4/33 8 mm - PODLAHA POD PĽAVÁJUCE PODLAHY 7 mm	OPRAVA PRE ELEKTRONICÁLII NOVÁ OMIEKTA - MALOVKA	ELEKTRONICÁLII MONTÁŽ OCELIOVÝCH KONSTRUKCI MOBILNÝCH ELEKTRONICÁLII NOVÝ KAZETOVÝ PODHĽAD A ÚPRAVY PRE SVETLO DO PODHĽADU
20	KUCHYNKA	7,87	KERAMICKÁ DLAŽBA	KERAMICKÝ OBRÁD	OMIEKTA	- NIVELIZAČNÁ IMPISTA 10 mm - VYŠKŤOVANÉ PODKLADU DO 10 mm - ODSŤAŽOVANIE KERAMICKÝCH DLAŽBY 30 - VYŠKŤOVANÉ VÝŠKŤOVANÉ PODKLADU - VYŠKŤOVANÉ ZDRAVOTNÝCH INŠTALÁCII	- DLAŽBA GREŠ - DLAŽBA PRÁDNY TPEL ADEK CA 20P CEA 5 mm/s - ŠARHŤOVANÁ ADEK GR - 0,3 kg/m ² - LEPIDLO ADEK XTG - 14 kg/m ²	VYŠKŤOVANÉ VONKAŠNÁ OBRÁD OBRÁDNY PRE REZERVY 2. Ú. A. ELEKTRON. OPRAVA PODKLADU POD NOVÝ KERAMICKÝ OBRÁD ZAKRYTIE POTRUBIA PREDAJENOU SOK STENOU NOVÝ KERAMICKÝ OBRÁD	ELEKTRONICÁLII MONTÁŽ OCELIOVÝCH KONSTRUKCI MOBILNÝCH ELEKTRONICÁLII NOVÝ KAZETOVÝ PODHĽAD A ÚPRAVY PRE SVETLO DO PODHĽADU
21	WC ŽŤP	3,65	PVC	OMIEKTA	OMIEKTA	- NIVELIZAČNÁ IMPISTA 10 mm - VYŠKŤOVANÉ PODKLADU - ODSŤAŽOVANIE PVC A NIVELITU	- DLAŽBA GREŠ - DLAŽBA PRÁDNY TPEL ADEK CA 20P CEA 5 mm/s - ŠARHŤOVANÁ ADEK GR - 0,3 kg/m ² - LEPIDLO ADEK XTG - 14 kg/m ²	STAVENÁ OPRAVA PRE VŤ OPRAVA PRE ELEKTRONICÁLII PRÍPRAVA PODKLADU POD KERAMICKÝ OBRÁD KERAMICKÝ OBRÁD MALOVKA A NA DIVERZ	ELEKTRONICÁLII MONTÁŽ OCELIOVÝCH KONSTRUKCI MOBILNÝCH ELEKTRONICÁLII NOVÝ KAZETOVÝ PODHĽAD A ÚPRAVY PRE SVETLO DO PODHĽADU
22	ÚPRAVŤOVANÉ	2,84	PVC	OMIEKTA	OMIEKTA	- NIVELIZAČNÁ IMPISTA 10 mm - VYŠKŤOVANÉ PODKLADU - ODSŤAŽOVANIE PVC A NIVELITU	- DLAŽBA GREŠ - DLAŽBA PRÁDNY TPEL ADEK CA 20P CEA 5 mm/s - ŠARHŤOVANÁ ADEK GR - 0,3 kg/m ² - LEPIDLO ADEK XTG - 14 kg/m ²	STAVENÁ OPRAVA PRE VŤ OPRAVA PRE ELEKTRONICÁLII PRÍPRAVA PODKLADU POD KERAMICKÝ OBRÁD KERAMICKÝ OBRÁD	ELEKTRONICÁLII MONTÁŽ OCELIOVÝCH KONSTRUKCI MOBILNÝCH ELEKTRONICÁLII NOVÝ KAZETOVÝ PODHĽAD A ÚPRAVY PRE SVETLO DO PODHĽADU
23	SKLAD	7,31	PVC	OMIEKTA	OMIEKTA	- NIVELIZAČNÁ IMPISTA 10 mm - VYŠKŤOVANÉ PODKLADU - ODSŤAŽOVANIE PVC A NIVELITU	- PVC 10 mm - LEPIDLO	STAVENÁ OPRAVA PRE VŤ OPRAVA PRE ELEKTRONICÁLII PRÍPRAVA PODKLADU POD KERAMICKÝ OBRÁD KERAMICKÝ OBRÁD	ELEKTRONICÁLII MONTÁŽ OCELIOVÝCH KONSTRUKCI MOBILNÝCH ELEKTRONICÁLII NOVÝ KAZETOVÝ PODHĽAD A ÚPRAVY PRE SVETLO DO PODHĽADU
24	STROJŤOVNÁ	18,75	PVC	OMIEKTA	OMIEKTA			VYŠKŤOVANÁ OPRAVA PRE VŤ VYŠKŤOVANÁ OMIEKTY PO ELEKTRONICÁLII MALOVKA	VYŠKŤOVANÉ OMIEKTY PO ELEKTRONICÁLII MALOVKA
REŠENÁ ČASŤ			436,62						

LEGENDA

- ŠACHTOVÝ POKLOP S OBLŤOVANÝM C20R600 600x600-HLÍNÍK
- SADOKRATOVNÁ PREKŤA C20R600 600x600-HLÍNÍK
- NAVRHOVANÉ PRŮVY Z PREČOVANÝCH YTONG
- JESTVUJÚCE MURIVO
-KONTAKTNÝ ZATEPLOVACÍ SYSTÉM BAUMIT STAR-120 mm
- NAVRHOVANÉ MURIVO Z TENHÁJ HELLUZ 4,0
-KONTAKTNÝ ZATEPLOVACÍ SYSTÉM BAUMIT STAR-120 mm
- JESTVUJÚCE MURIVO
-KONTAKTNÝ ZATEPLOVACÍ SYSTÉM BAUMIT MINERAL-120 mm

SADA Č.:	ZODP. PROJEKTANT: ING. ARCH. MARIAN KURČ	PROJEKTOVÁ KANCELÁRIA
	ARCHITEKTÚRA: ING. ARCH. M. KURČ, ING. ARCH. P. KŤAŽEK, ING. ARCH. I. ČŤÁRY ml.	
	H.I.P.: ING. ARCH. MARIAN KURČ	
	VYPRACOVANÉ: ING. PAVOL PEČIAR	
VÝKRES Č. 01	INVESTOR: UKF TRIEDA ANDREA HLINUKA 1, 949 74 NITRA	e-mail: shfinal@shfinal.sk
	NÁZOV: PORADENSKÉ CENTRUM UKF V NITRE -ÚPRAVA	
	DATUM: 12/2016	
	STUPEŇ: JP	
OBSAH:	PŮDORYS I. NADZEMNÉHO PODLAŽIA	Č. ZAK.: M-1100
ČASŤ:	A R C H	FORMÁT: Bx A4