


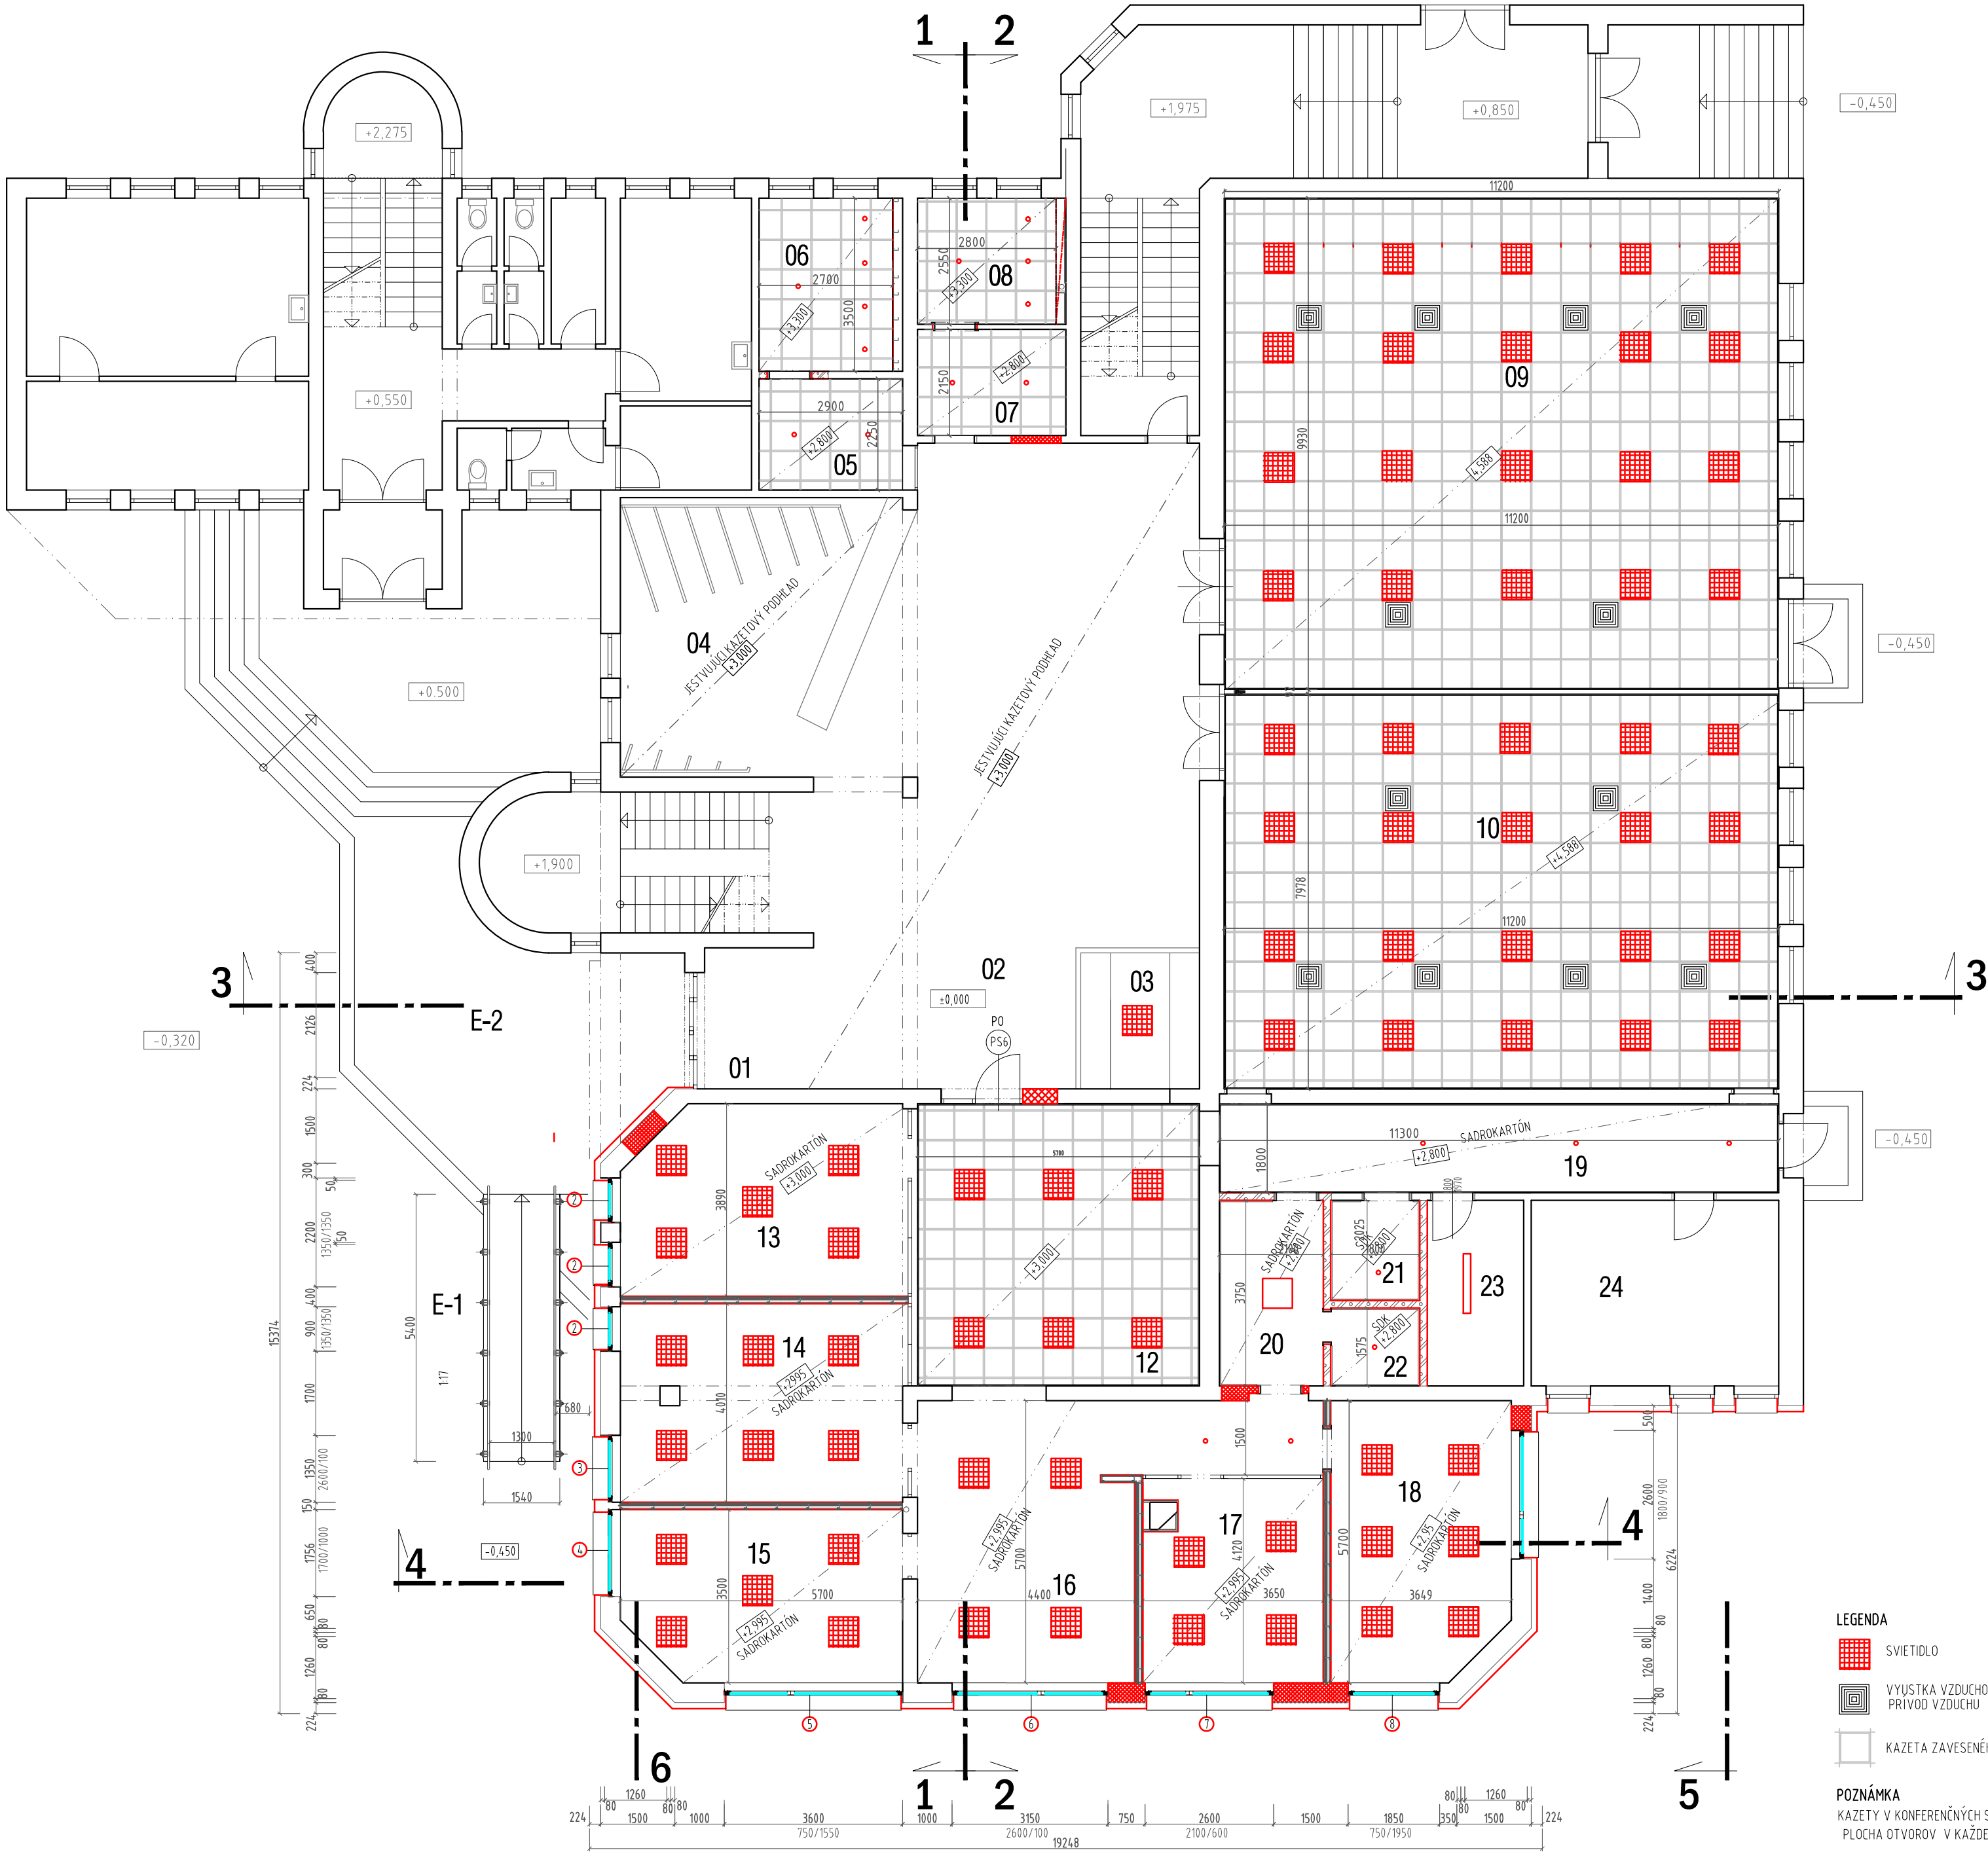

- LEGENDA
- SVIETIDLO
 - VYUSTKA VZDUCHOTECHNIKY
PRIVOD VZDUCHU
 - KAZETA ZAVESENÉHO PODHLADU

POZNÁMKA
KAZETY V KONFERENČNÝCH SÁLACH SÚ PERFOROVANÉ
PLOCHA OTVOROV V KAŽDEJ KONFERENČNEJ SÁLE 0,5 m²

SADA Č.:	ZODP. PROJEKTANT: ING. ARCH. MARIÁN KURUC	PROJEKTOVÁ KANCELÁRIA SHfinal s.r.o. e-mail: shfinal@shfinal.sk
	ARCHITEKTÚRA: ING. ARCH. M. KURUC, ING. ARCH. P. KŇÁŽEK, ING. ARCH. I. ČITÁRY ml.	
	H.I.P.: ING. ARCH. MARIÁN KURUC	
	VYPRACOVAL: ING. PAVOL PEČIAR	
	INVESTOR: UKF TRIEDA ANDREJA HLINKU 1, 949 74 NITRA	
VÝKRES Č. 02	NÁZOV: PORADENSKÉ CENTRUM UKF V NITRE - ÚPRAVA	DÁTUM: 12/2016
		STUPEŇ: J.P.
	OBSAH: PODHLÁDY	Č. ZAK.: M=1:100
		FORMÁT: 8x A4
		ČASŤ: A R C H.