

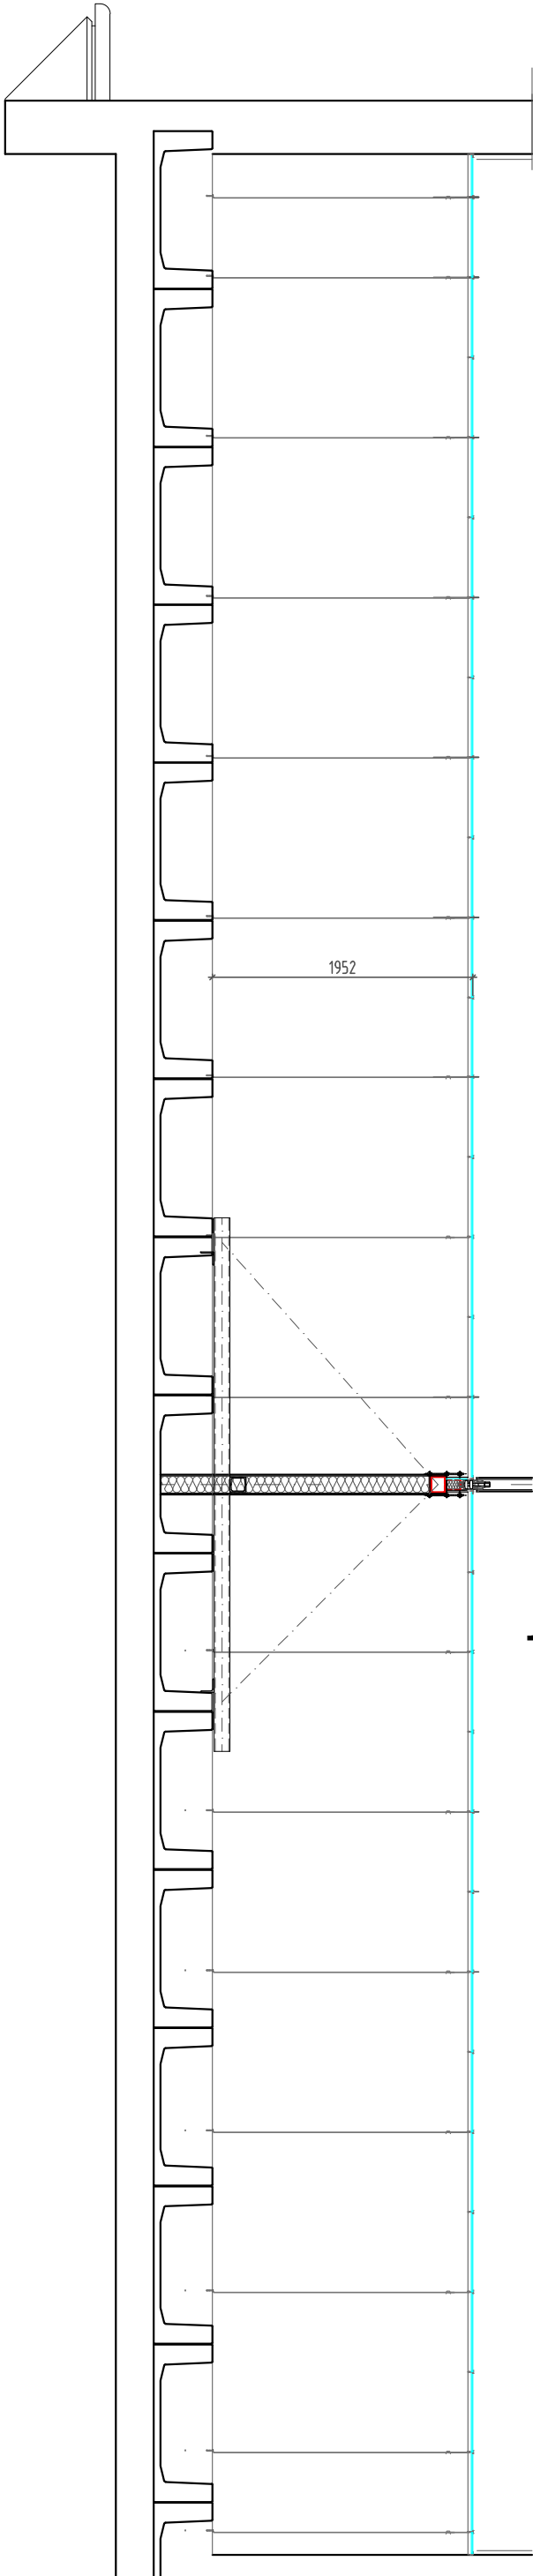


REZ R-R
M 1:50

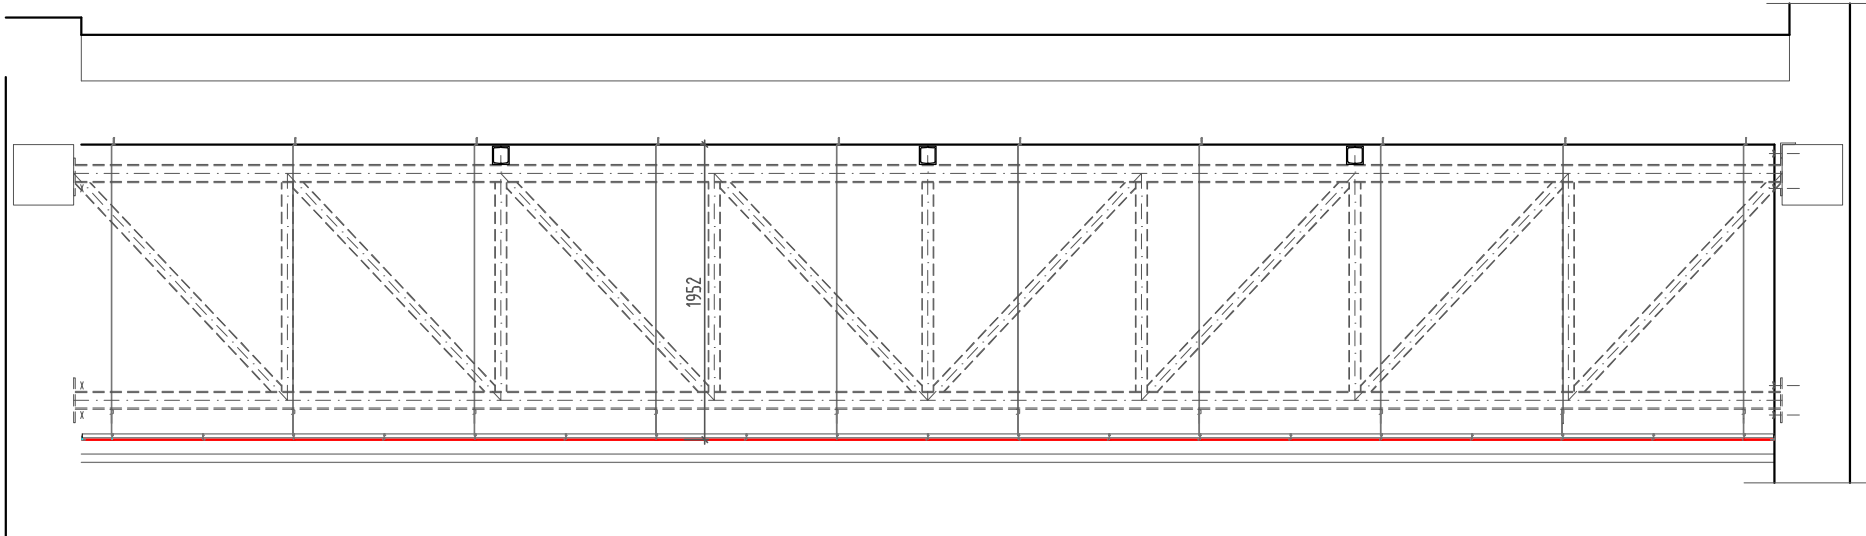


09

10

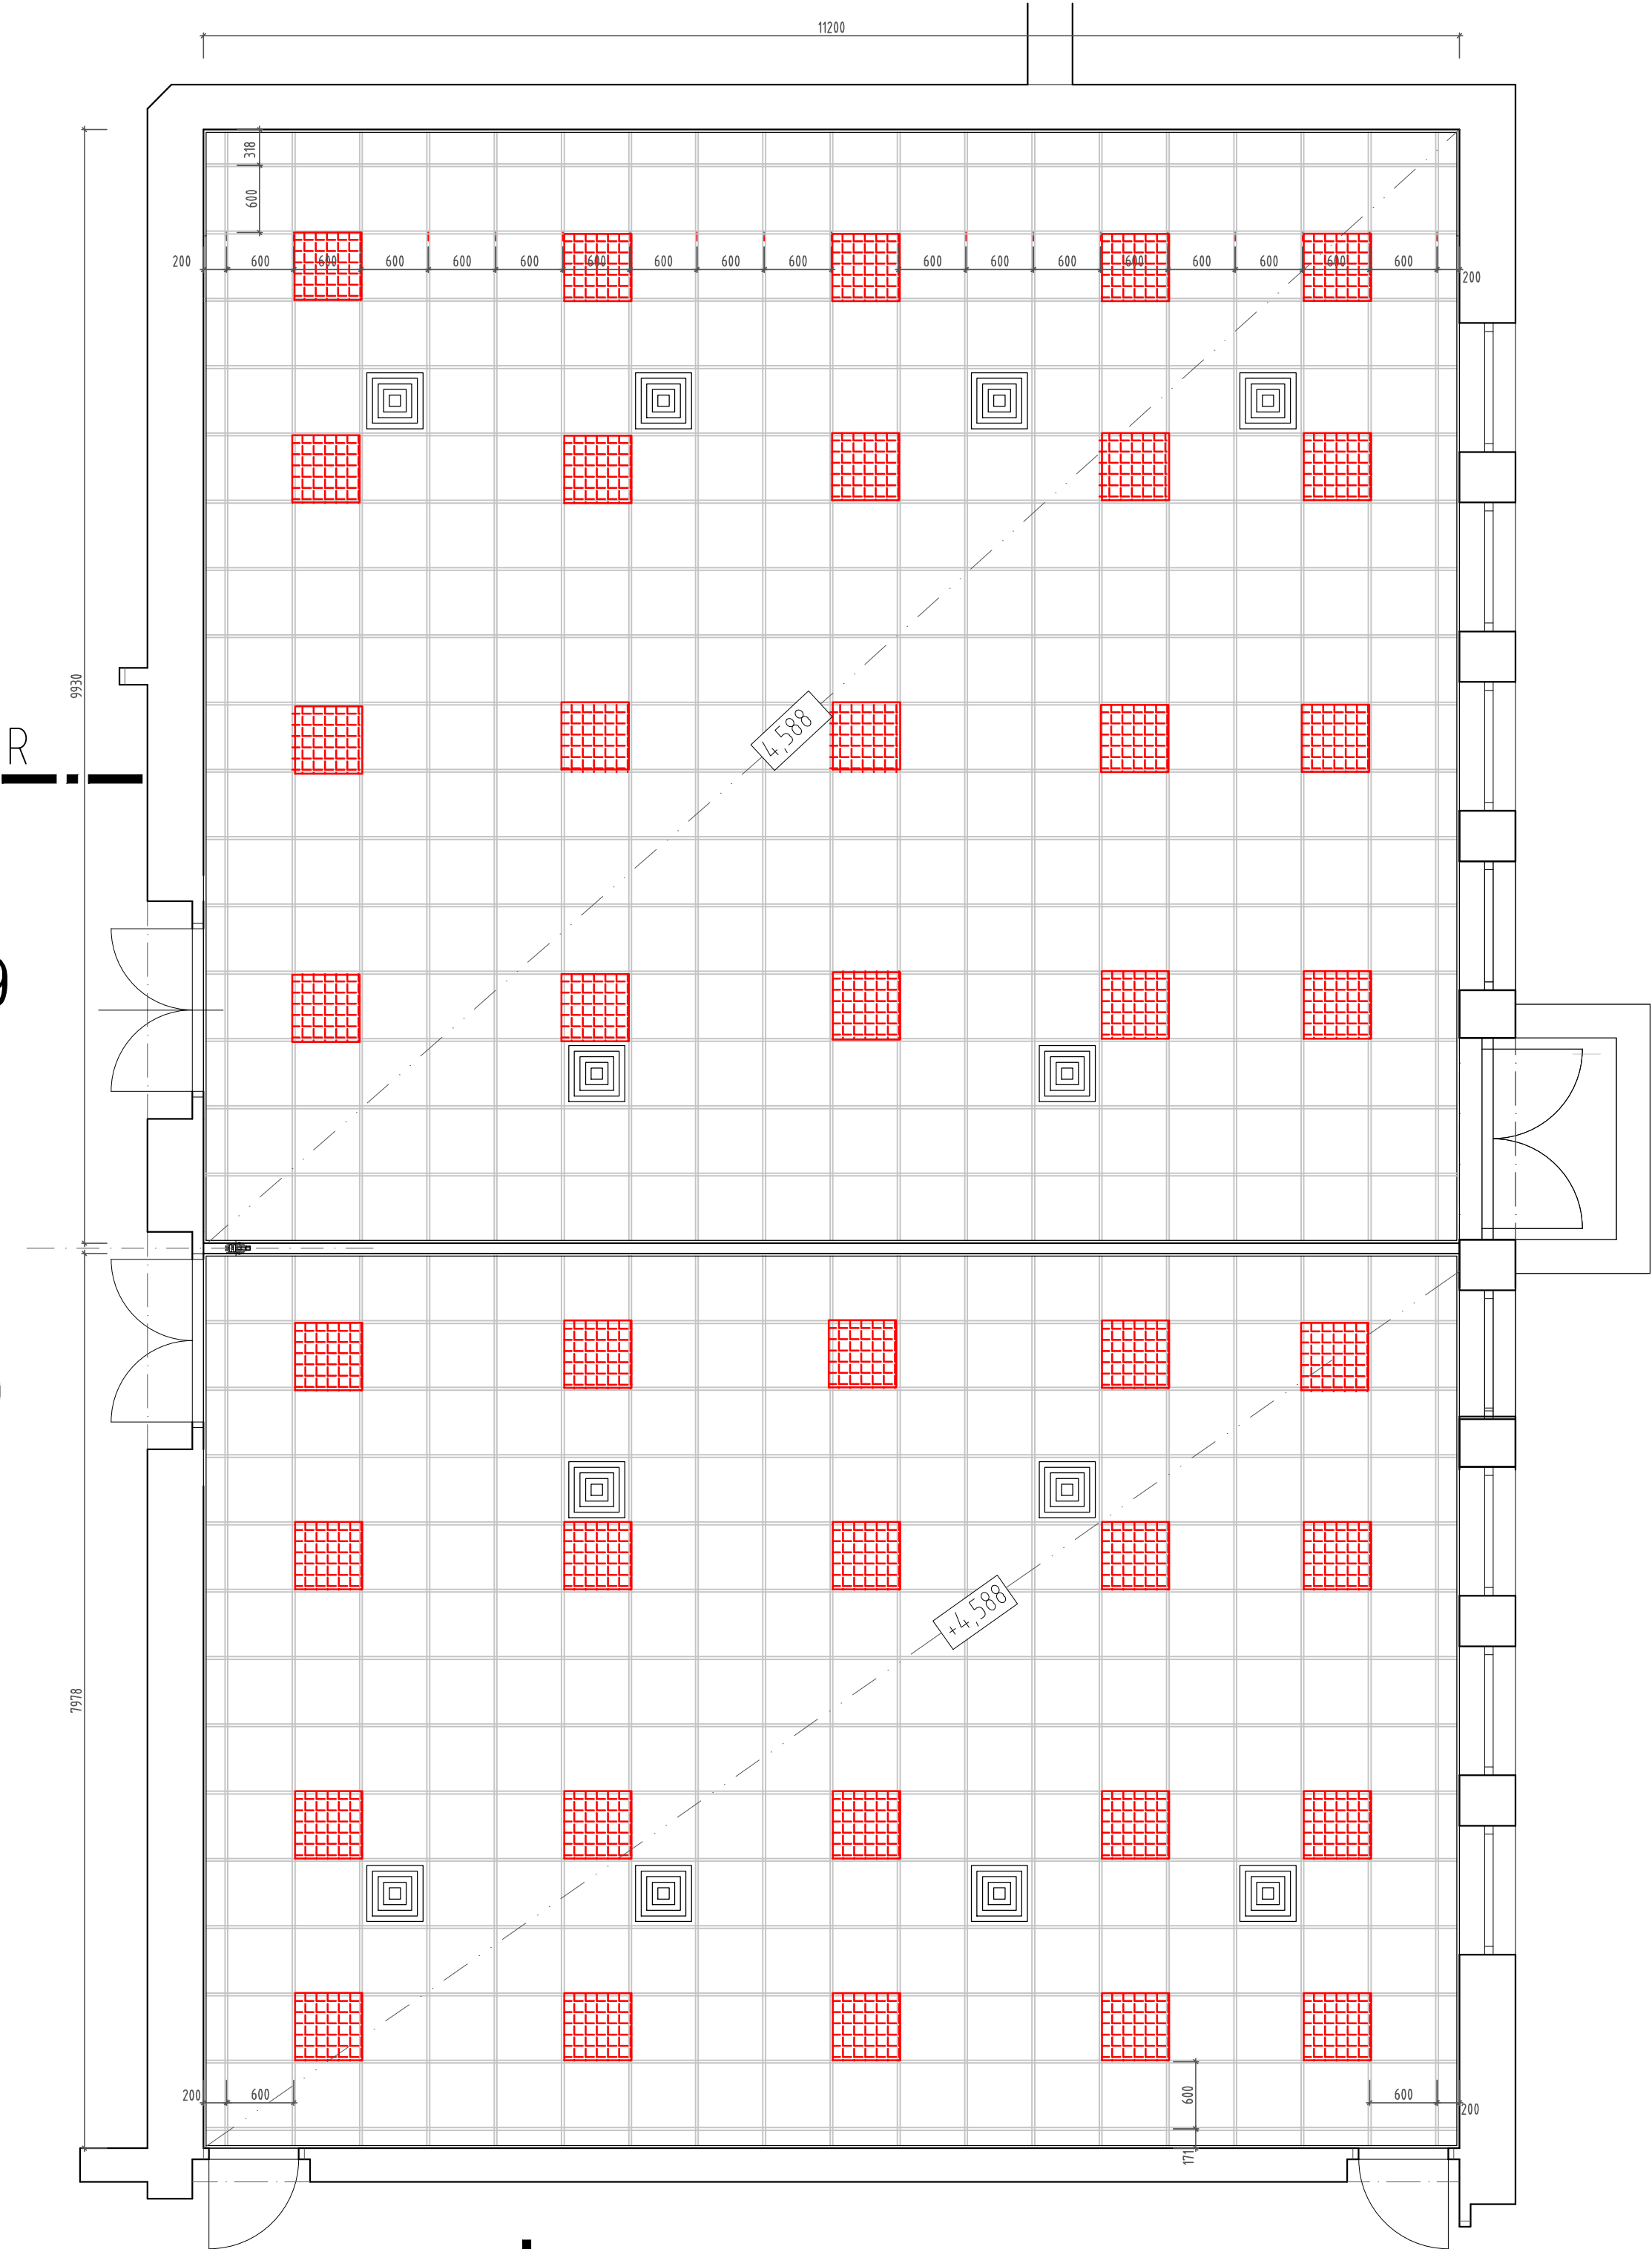


REZ R-R
M 1:50

LEGENDA

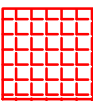

SVIETIDLO

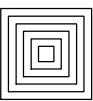

VYUSTKA VZDUCHOTECHNIKY
PRIVOD VZDUCHU



KAZETA ZAVESENÉHO PODHLADU
PERFOROVANA

PLOCHA OTVOROV
V KAŽDEJ KONFERENČNEJ SÁLE 0,5 m2

R

SADA Č.:	ZODP. PROJEKTANT: ING. ARCH. MARIÁN KURUC	PROJEKTOVÁ KANCELÁRIA SHfinal .s.r.o. e-mail: shfinal@shfinal.sk
	ARCHITEKTÚRA: ING. ARCH. M. KURUC, ING. ARCH. P. KŇAŽEK, ING. ARCH. I. ČITÁRY ml.	
	H.I.P.: ING. ARCH. MARIÁN KURUC	
	VYPRACOVAL: ING. PAVOL PEČIAR	
	INVESTOR: UKF TRIEDA ANDREJA HLINKU 1, 949 74 NITRA	
VÝKRES Č. 03	NÁZOV: PORADENSKÉ CENTRUM UKF V NITRE -ÚPRAVA	DÁTUM: 12/2016
		STUPEN: J.P.
		Č. ZAK.: M-150
		MERITKO: 4x A4
	OBSAH: PODHLAD V KONFERENČNEJ SÁLE	ČASŤ: ARCH.