


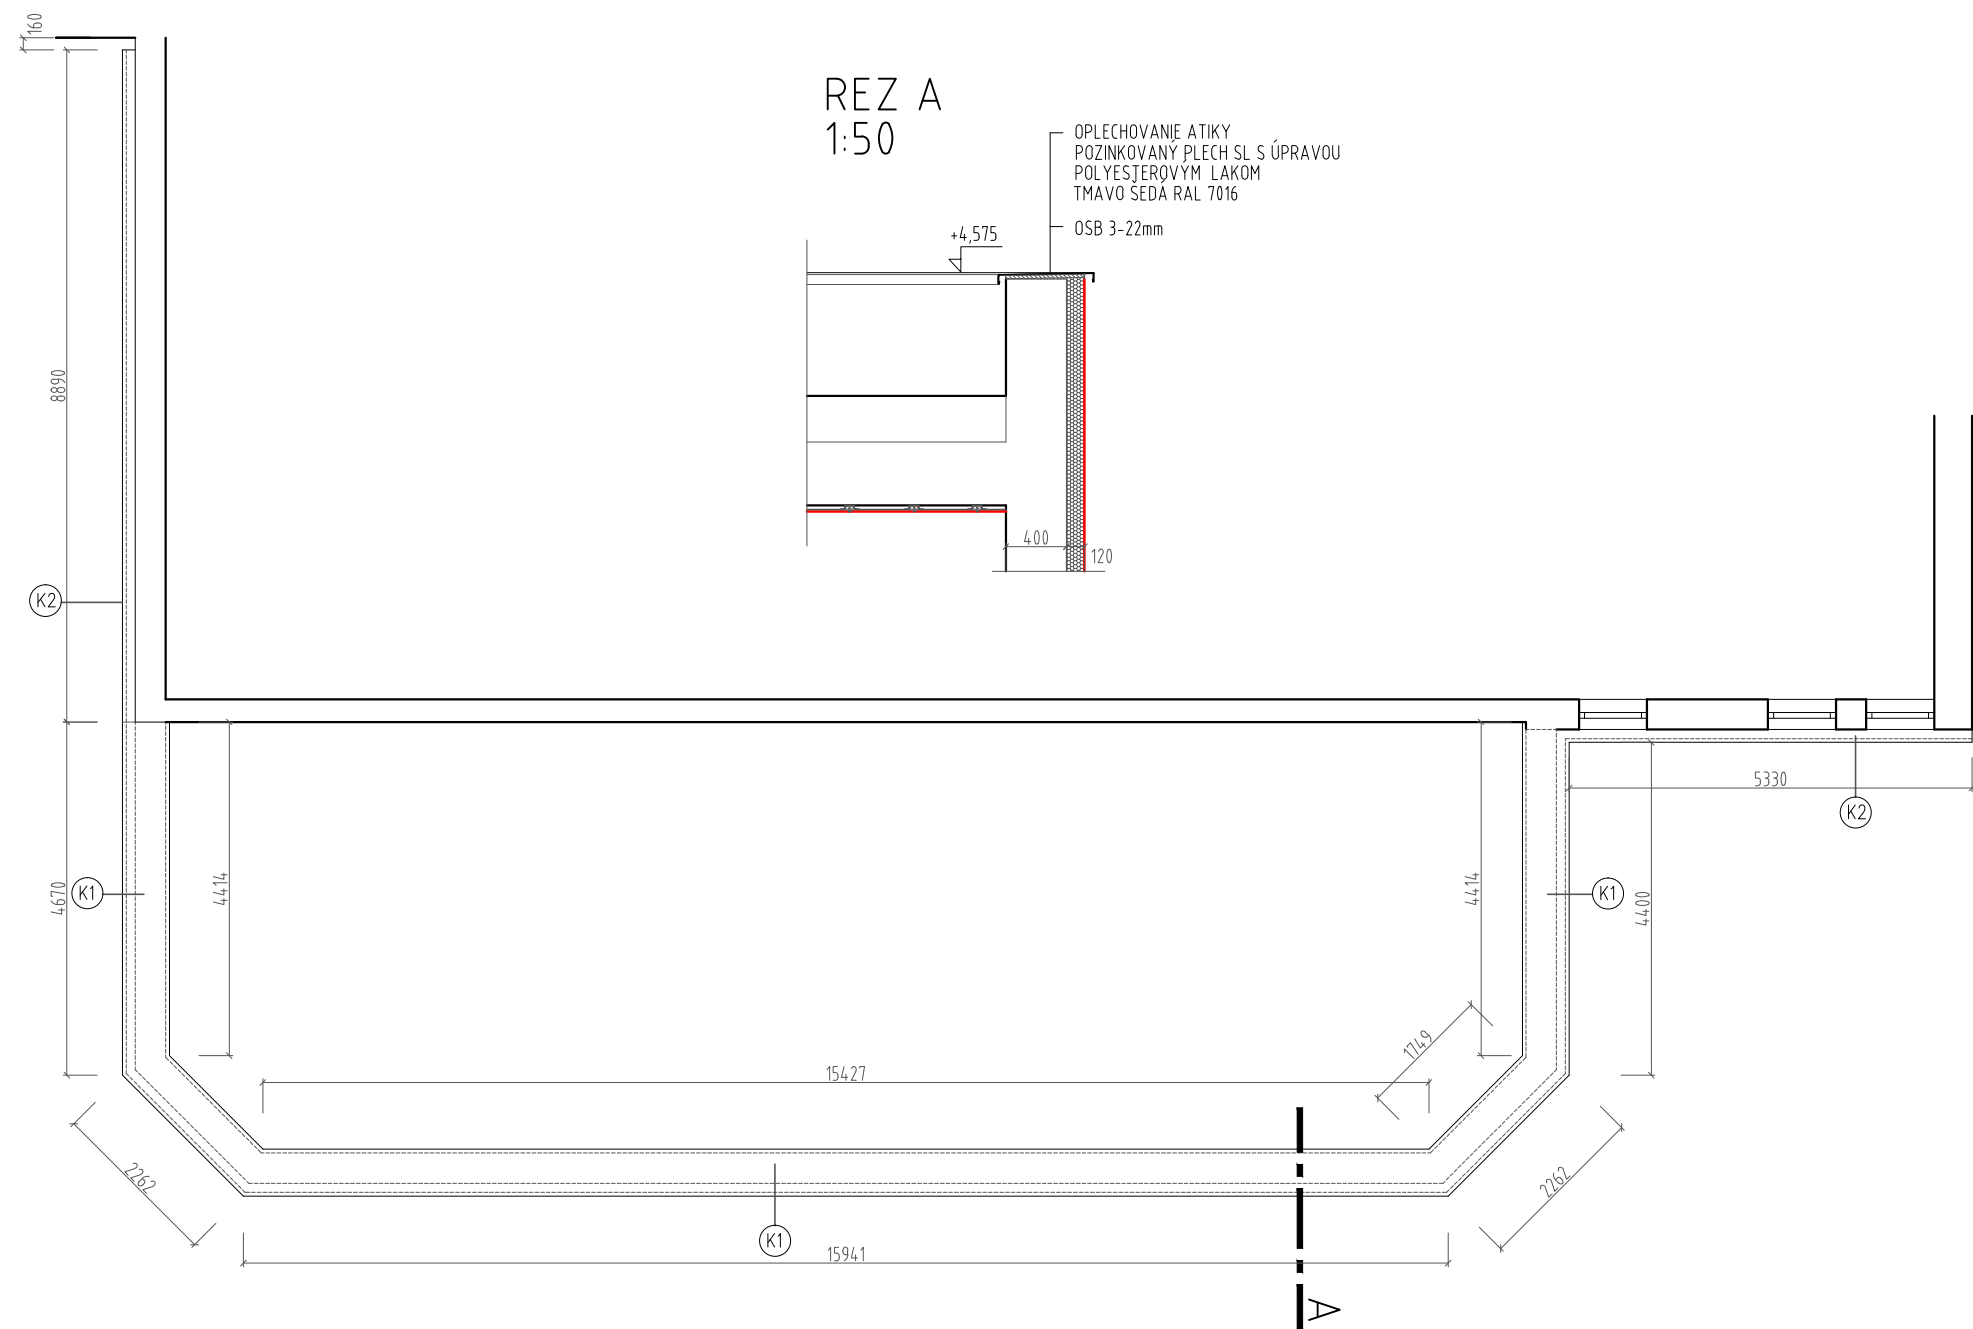

Oplechovanie atiky

SADA Č.:	ZODP. PROJEKTANT: ING. ARCH. MARIÁN KURUC	PROJEKTOVÁ KANCELÁRIA SHfinal <i>s.r.o.</i> e-mail: shfinal@shfinal.sk
	ARCHITEKTÚRA: ING. ARCH. M. KURUC, ING. ARCH. P. KŇAŽEK, ING.ARCH. I. ČITÁRY ml.	
	H.I.P.: ING. ARCH. MARIÁN KURUC	
	VYPRACOVAL: ING.PAVOL PECIAR	
	INVESTOR: UKF TRIEDA ANDREJA HLINKU 1, 949 74 NITRA	
VÝKRES Č. 04	NÁZOV: PORADENSKÉ CENTRUM UKF V NITRE -ÚPRAVA	DÁTUM: 12/2016
		STUPEŇ: J.P
		Č.ZAK.:
		MERÍTKO: M=1:100
		FORMÁT: 2x A4
	OBSAH: OPLECHOVANIE ATIKY KONŠTRUKCIA ODVETRAanej FASÁDY V ÚROVNI ATIKY	ČASŤ: A R C H.