


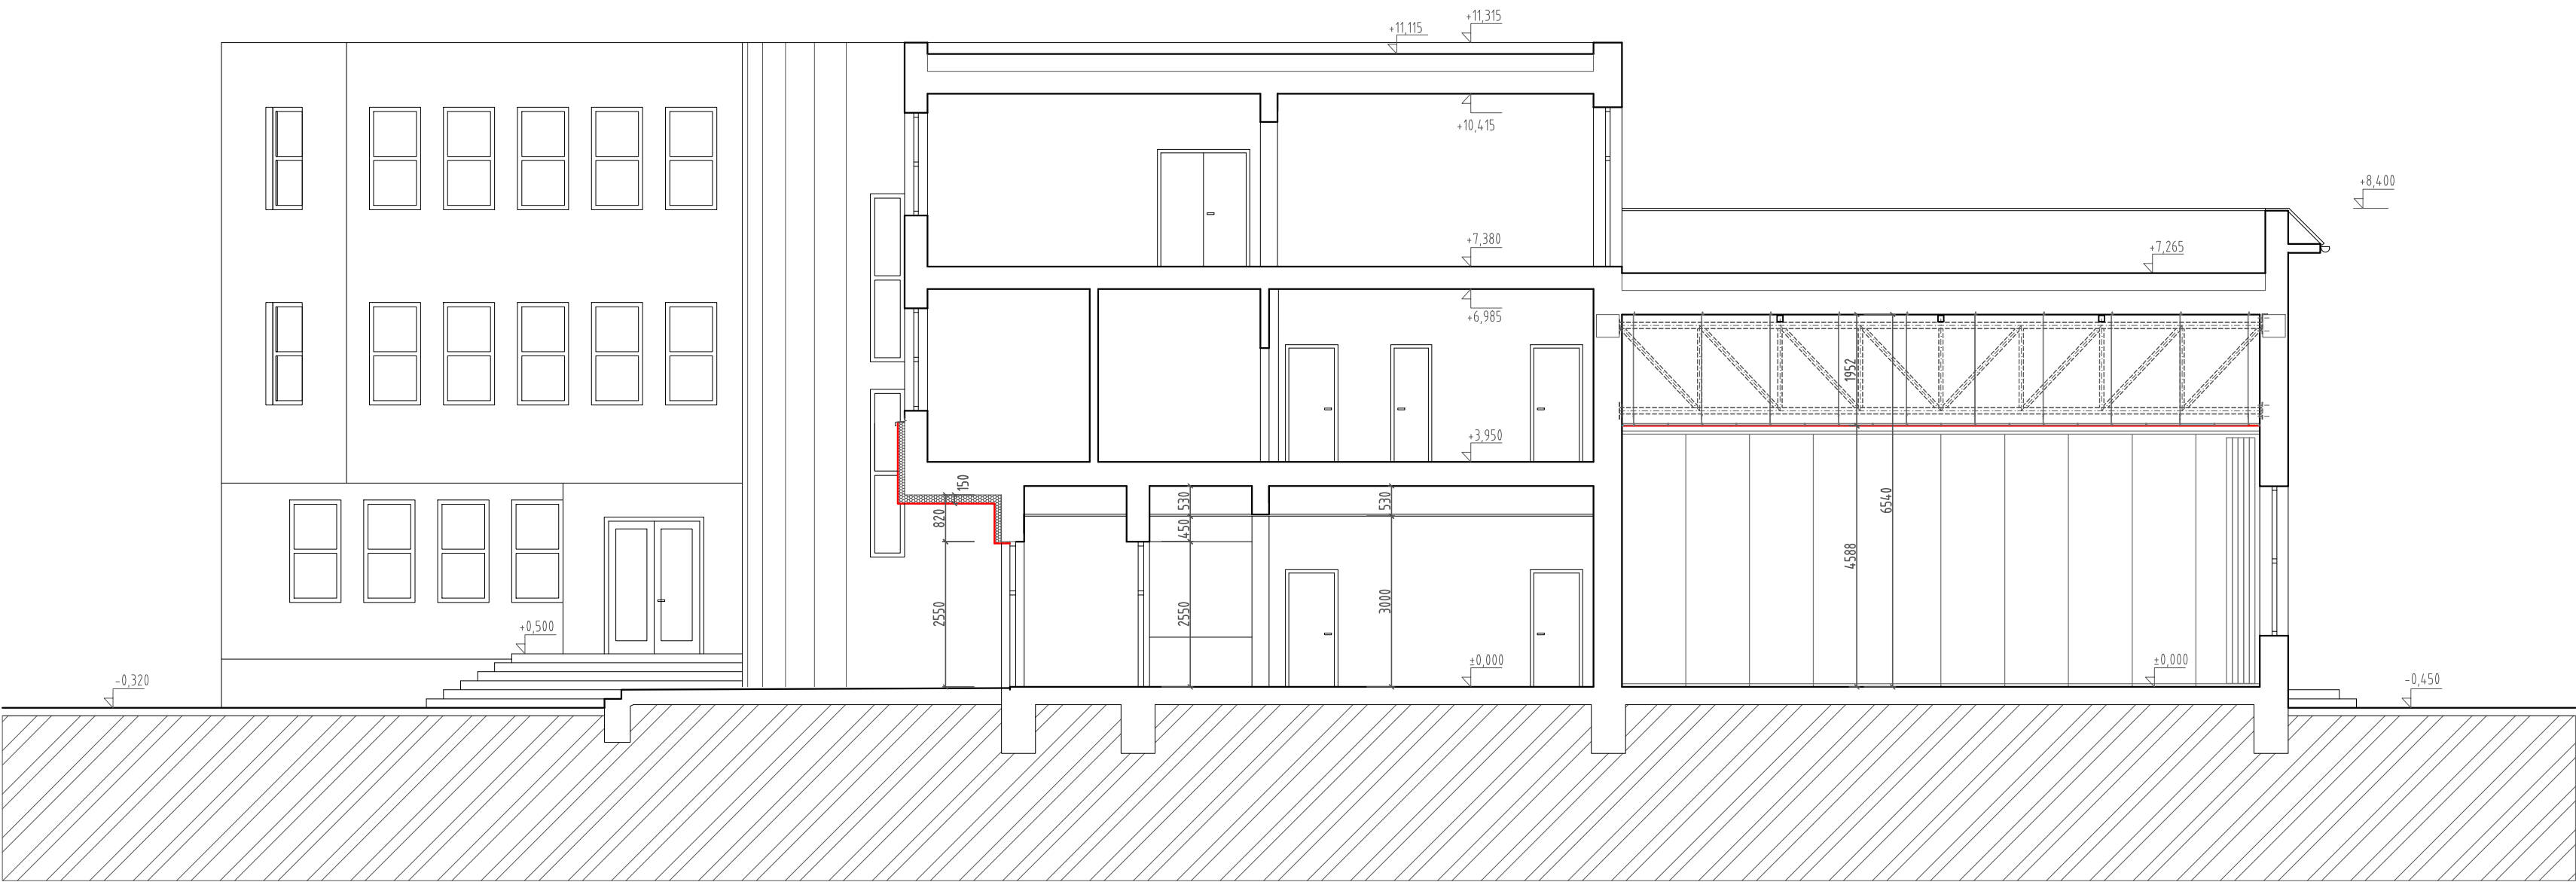

REZOPOHĽAD 3-3

SADA Č.:	ZODP. PROJEKTANT: ING. ARCH. MARIÁN KURUC	PROJEKTOVÁ KANCELÁRIA SHfinal <i>s.r.o.</i> e-mail: shfinal@shfinal.sk
	ARCHITEKTÚRA: ING. ARCH. M. KURUC, ING. ARCH. P. KŇAŽEK, ING. ARCH. I. ČITÁRY ml.	
	H.I.P.: ING. ARCH. MARIÁN KURUC	
	VYPRACOVAL: ING. PAVOL PECIAR	
	INVESTOR: UKF TRIEDA ANDREJA HLINKU 1, 949 74 NITRA	
VÝKRES Č. 07	NÁZOV: PORADENSKÉ CENTRUM UKF V NITRE -ÚPRAVA	DÁTUM: 12/2016
		STUPEN: J.P
		Č. ZAK.: M-1:100
		MERITKO: 3x A4
		ČASŤ: ARCH.
	OBSAH: REZOPOHĽAD 3-3	