


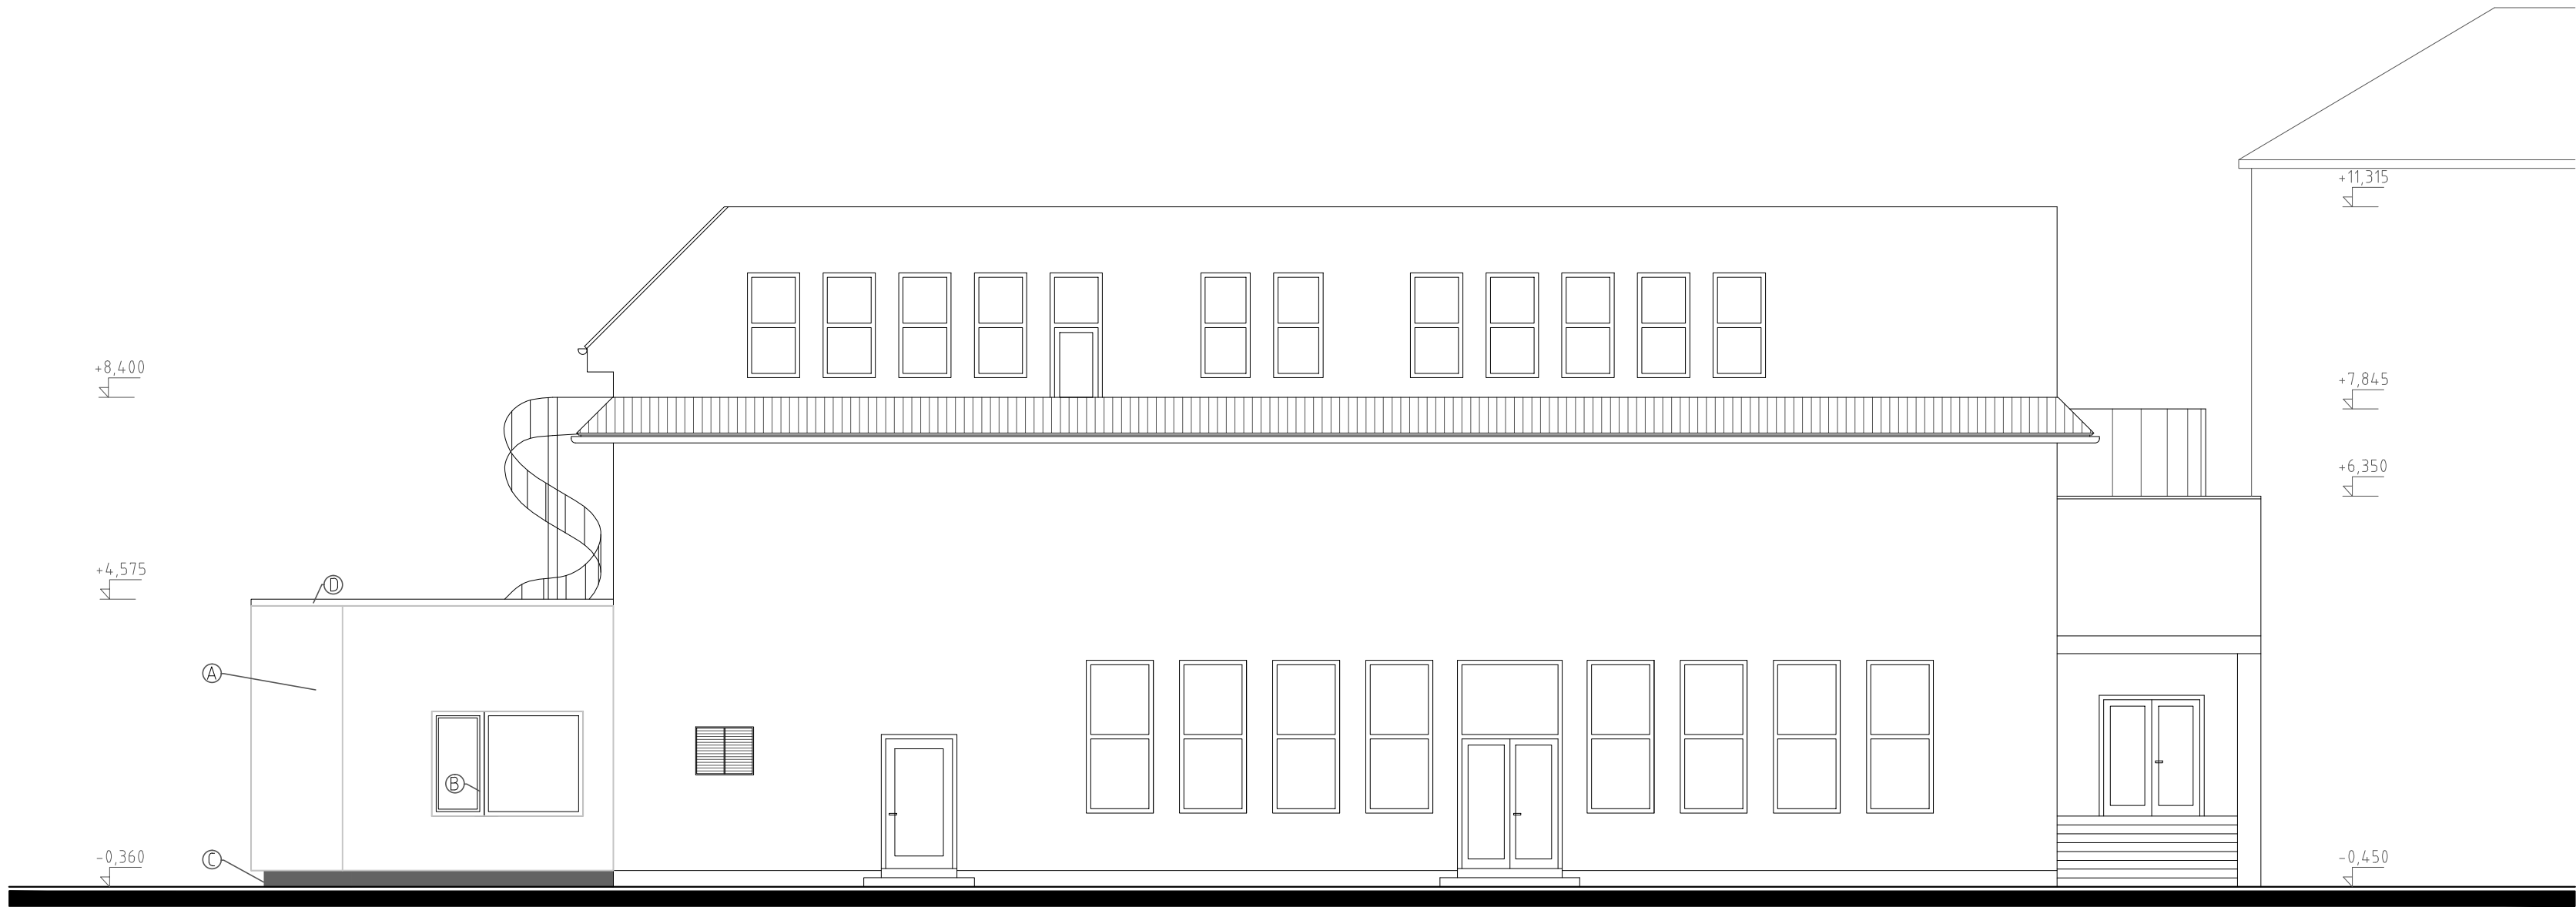

- LEGENDA MATERIALOV
- Ⓐ – ŠEDÁ 0883-BAUMIT LIFE
 - Ⓑ – PLASTOVÉ VÝPLNE OTVOROV FAREBNÝ ODTIEŇ GRAU (RENOLIT 7155.050.167)
 - Ⓒ – BAUMIT LIFE M 331
 - Ⓓ – ZÁBRADLIE RAL 7016

POHLAD VÝCHODNÝ – NÁVRH

SADA Č.:	ZODP. PROJEKTANT: ING. ARCH. MARIÁN KURUC	PROJEKTOVÁ KANCELÁRIA <i>SHfinal</i> s.r.o. e-mail: shfinal@shfinal.sk
	ARCHITEKTÚRA: ING. ARCH. M. KURUC, ING. ARCH. P. KŇÁŽEK, ING.ARCH. I. ČITÁRY ml.	
	H.I.P.: ING. ARCH. MARIÁN KURUC	
	VYPRACOVAL: ING.PAVOL PECIAR	
	INVESTOR: UKF TRIEDA ANDRÉJA HLINKU 1, 949 74 NITRA	
VÝKRES Č. 12	NÁZOV: PORADENSKÉ CENTRUM UKF V NITRE -ÚPRAVA	DÁTUM: 12/2016
		STUPEN: J.P
		Č.ZAK.:
		MERITKO: M=1:100
		FORMÁT: 3x A4
	OBSAH: POHLAD VÝCHODNÝ- NÁVRH	ČASŤ: A R C H.