
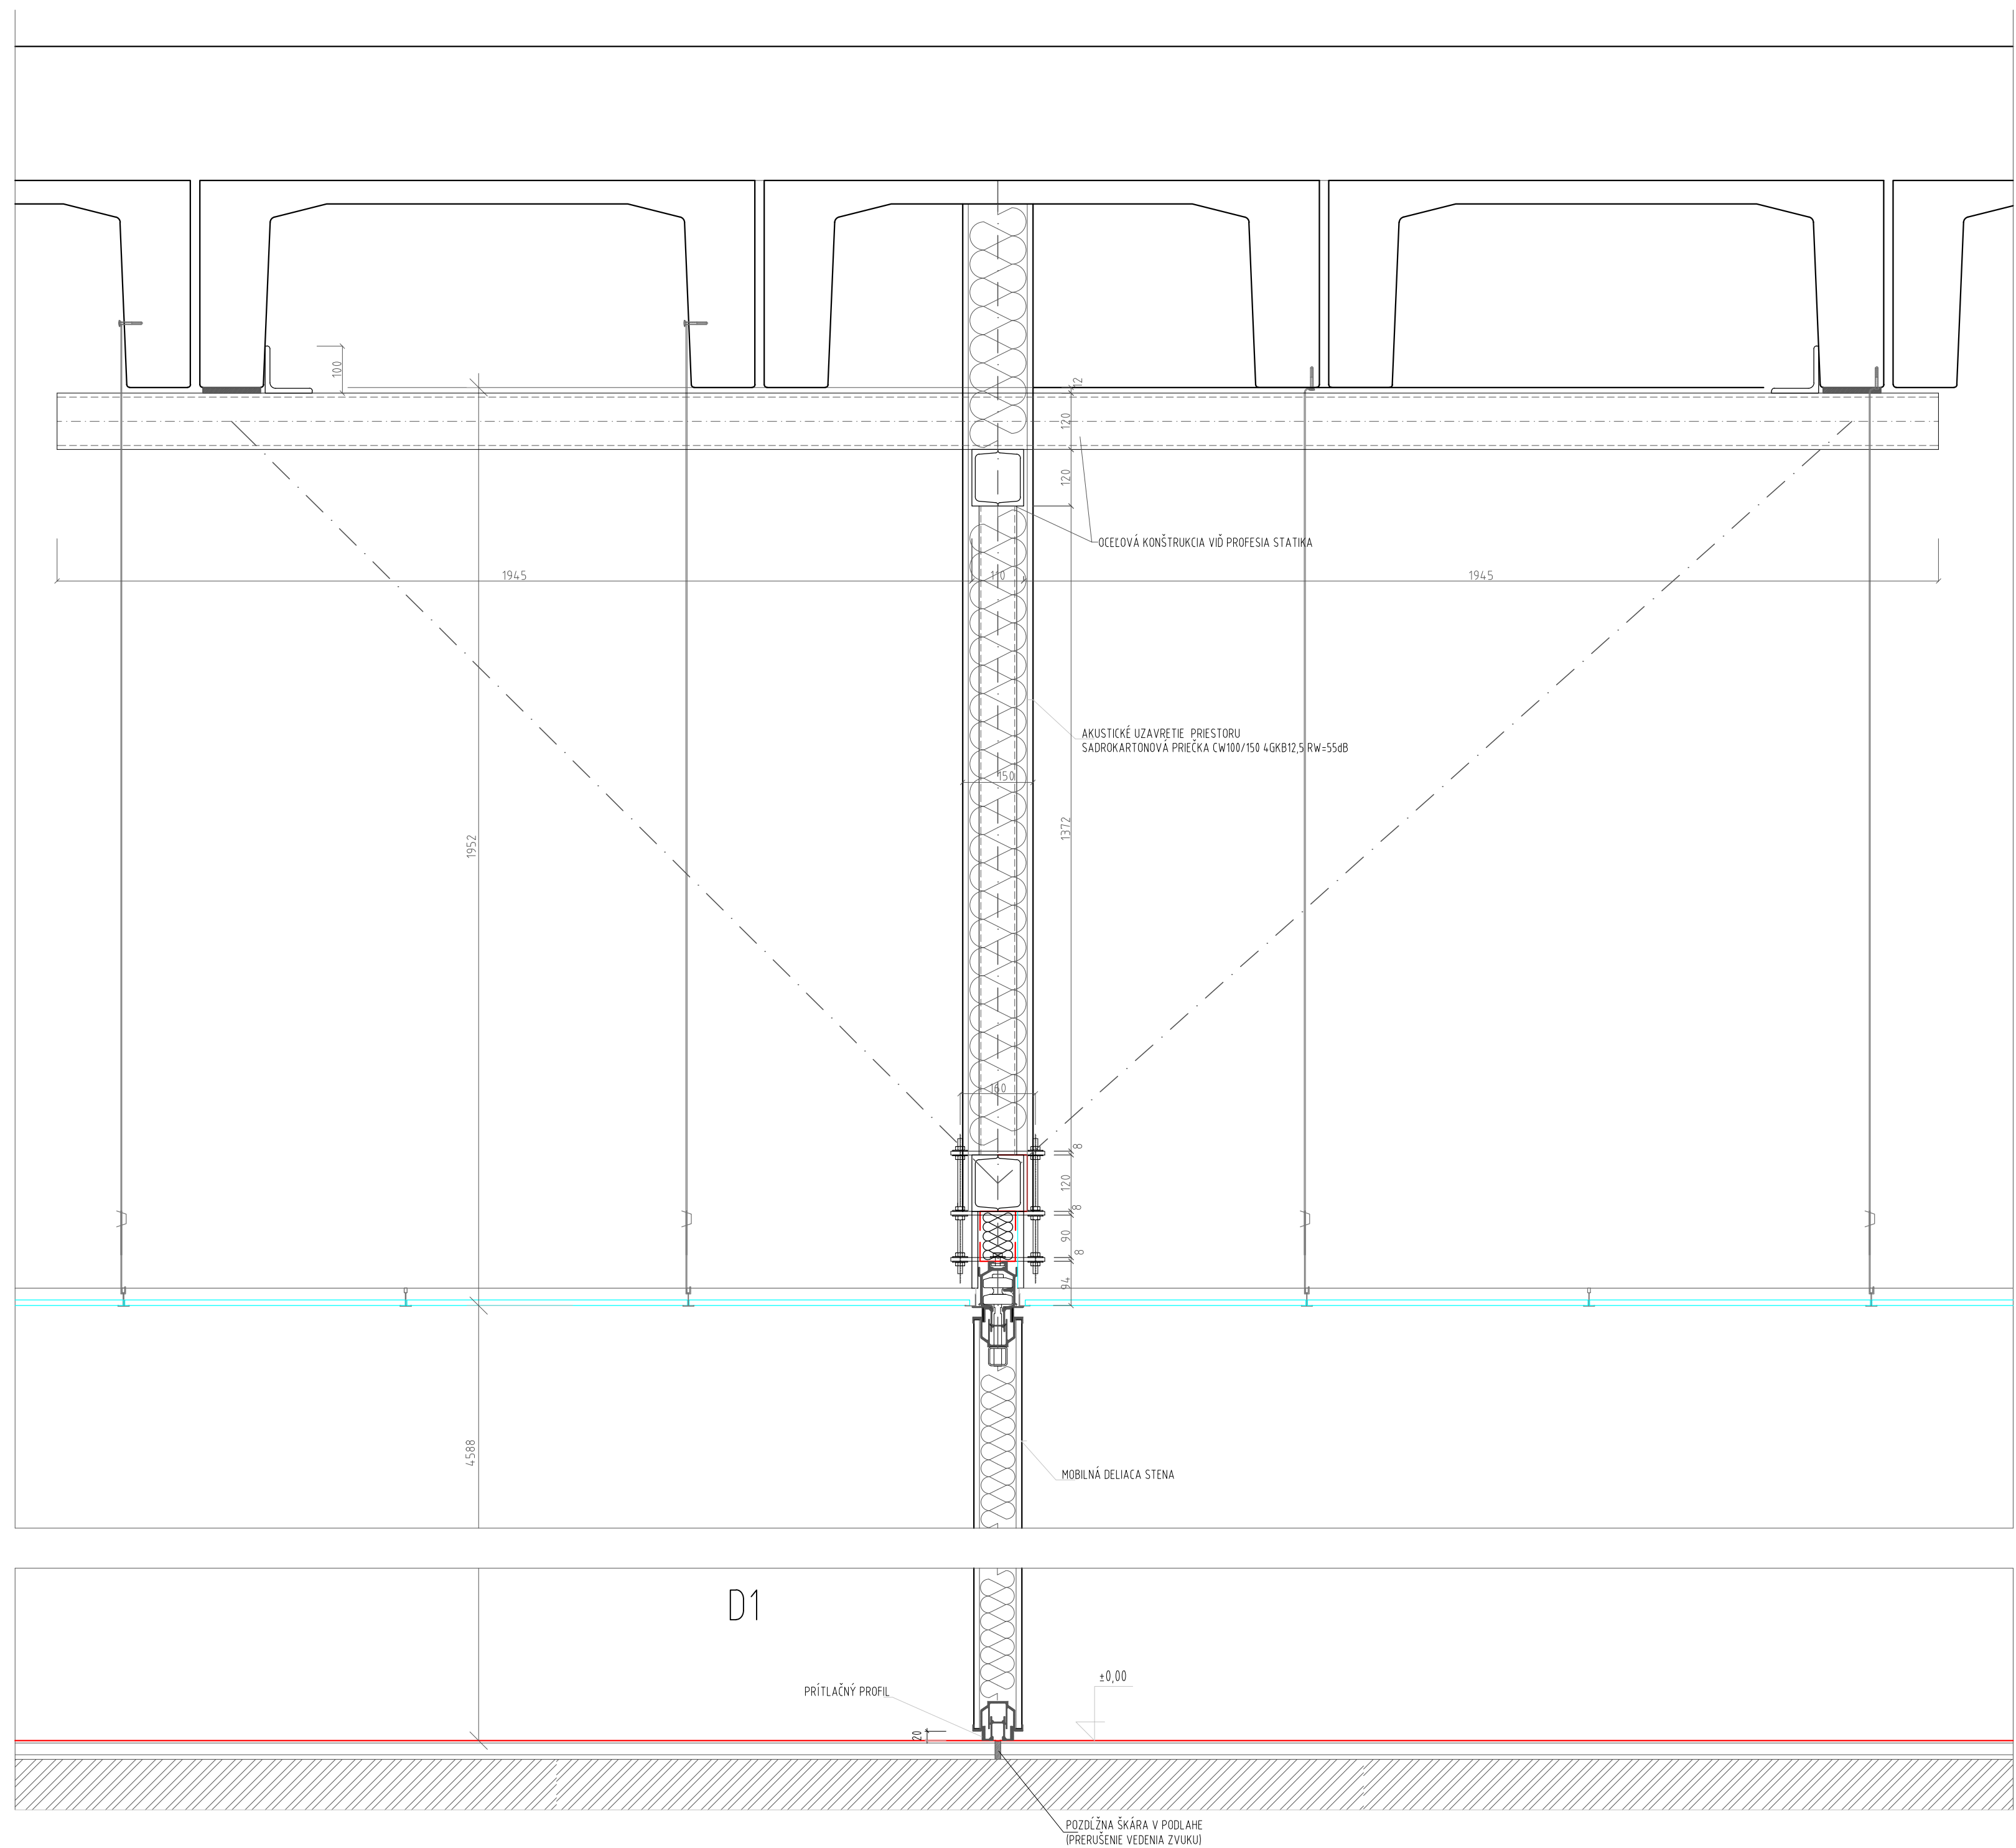
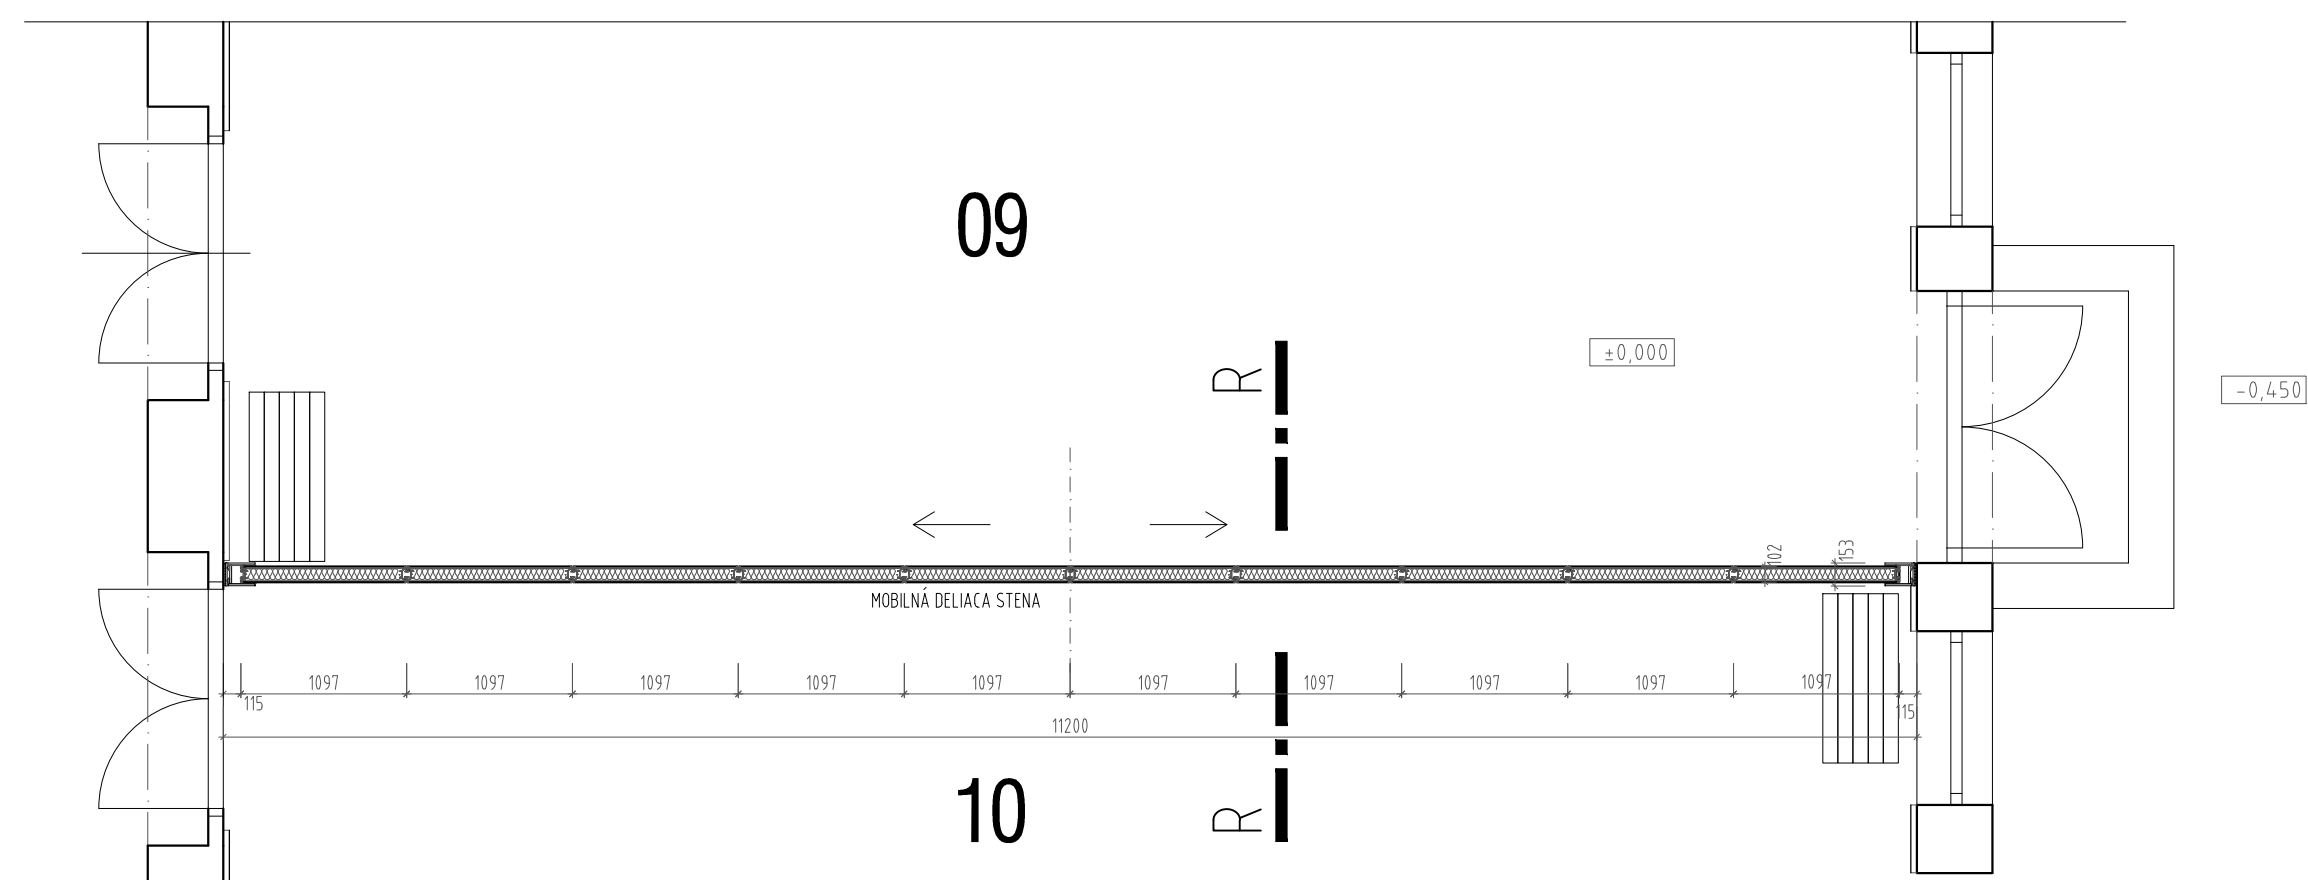


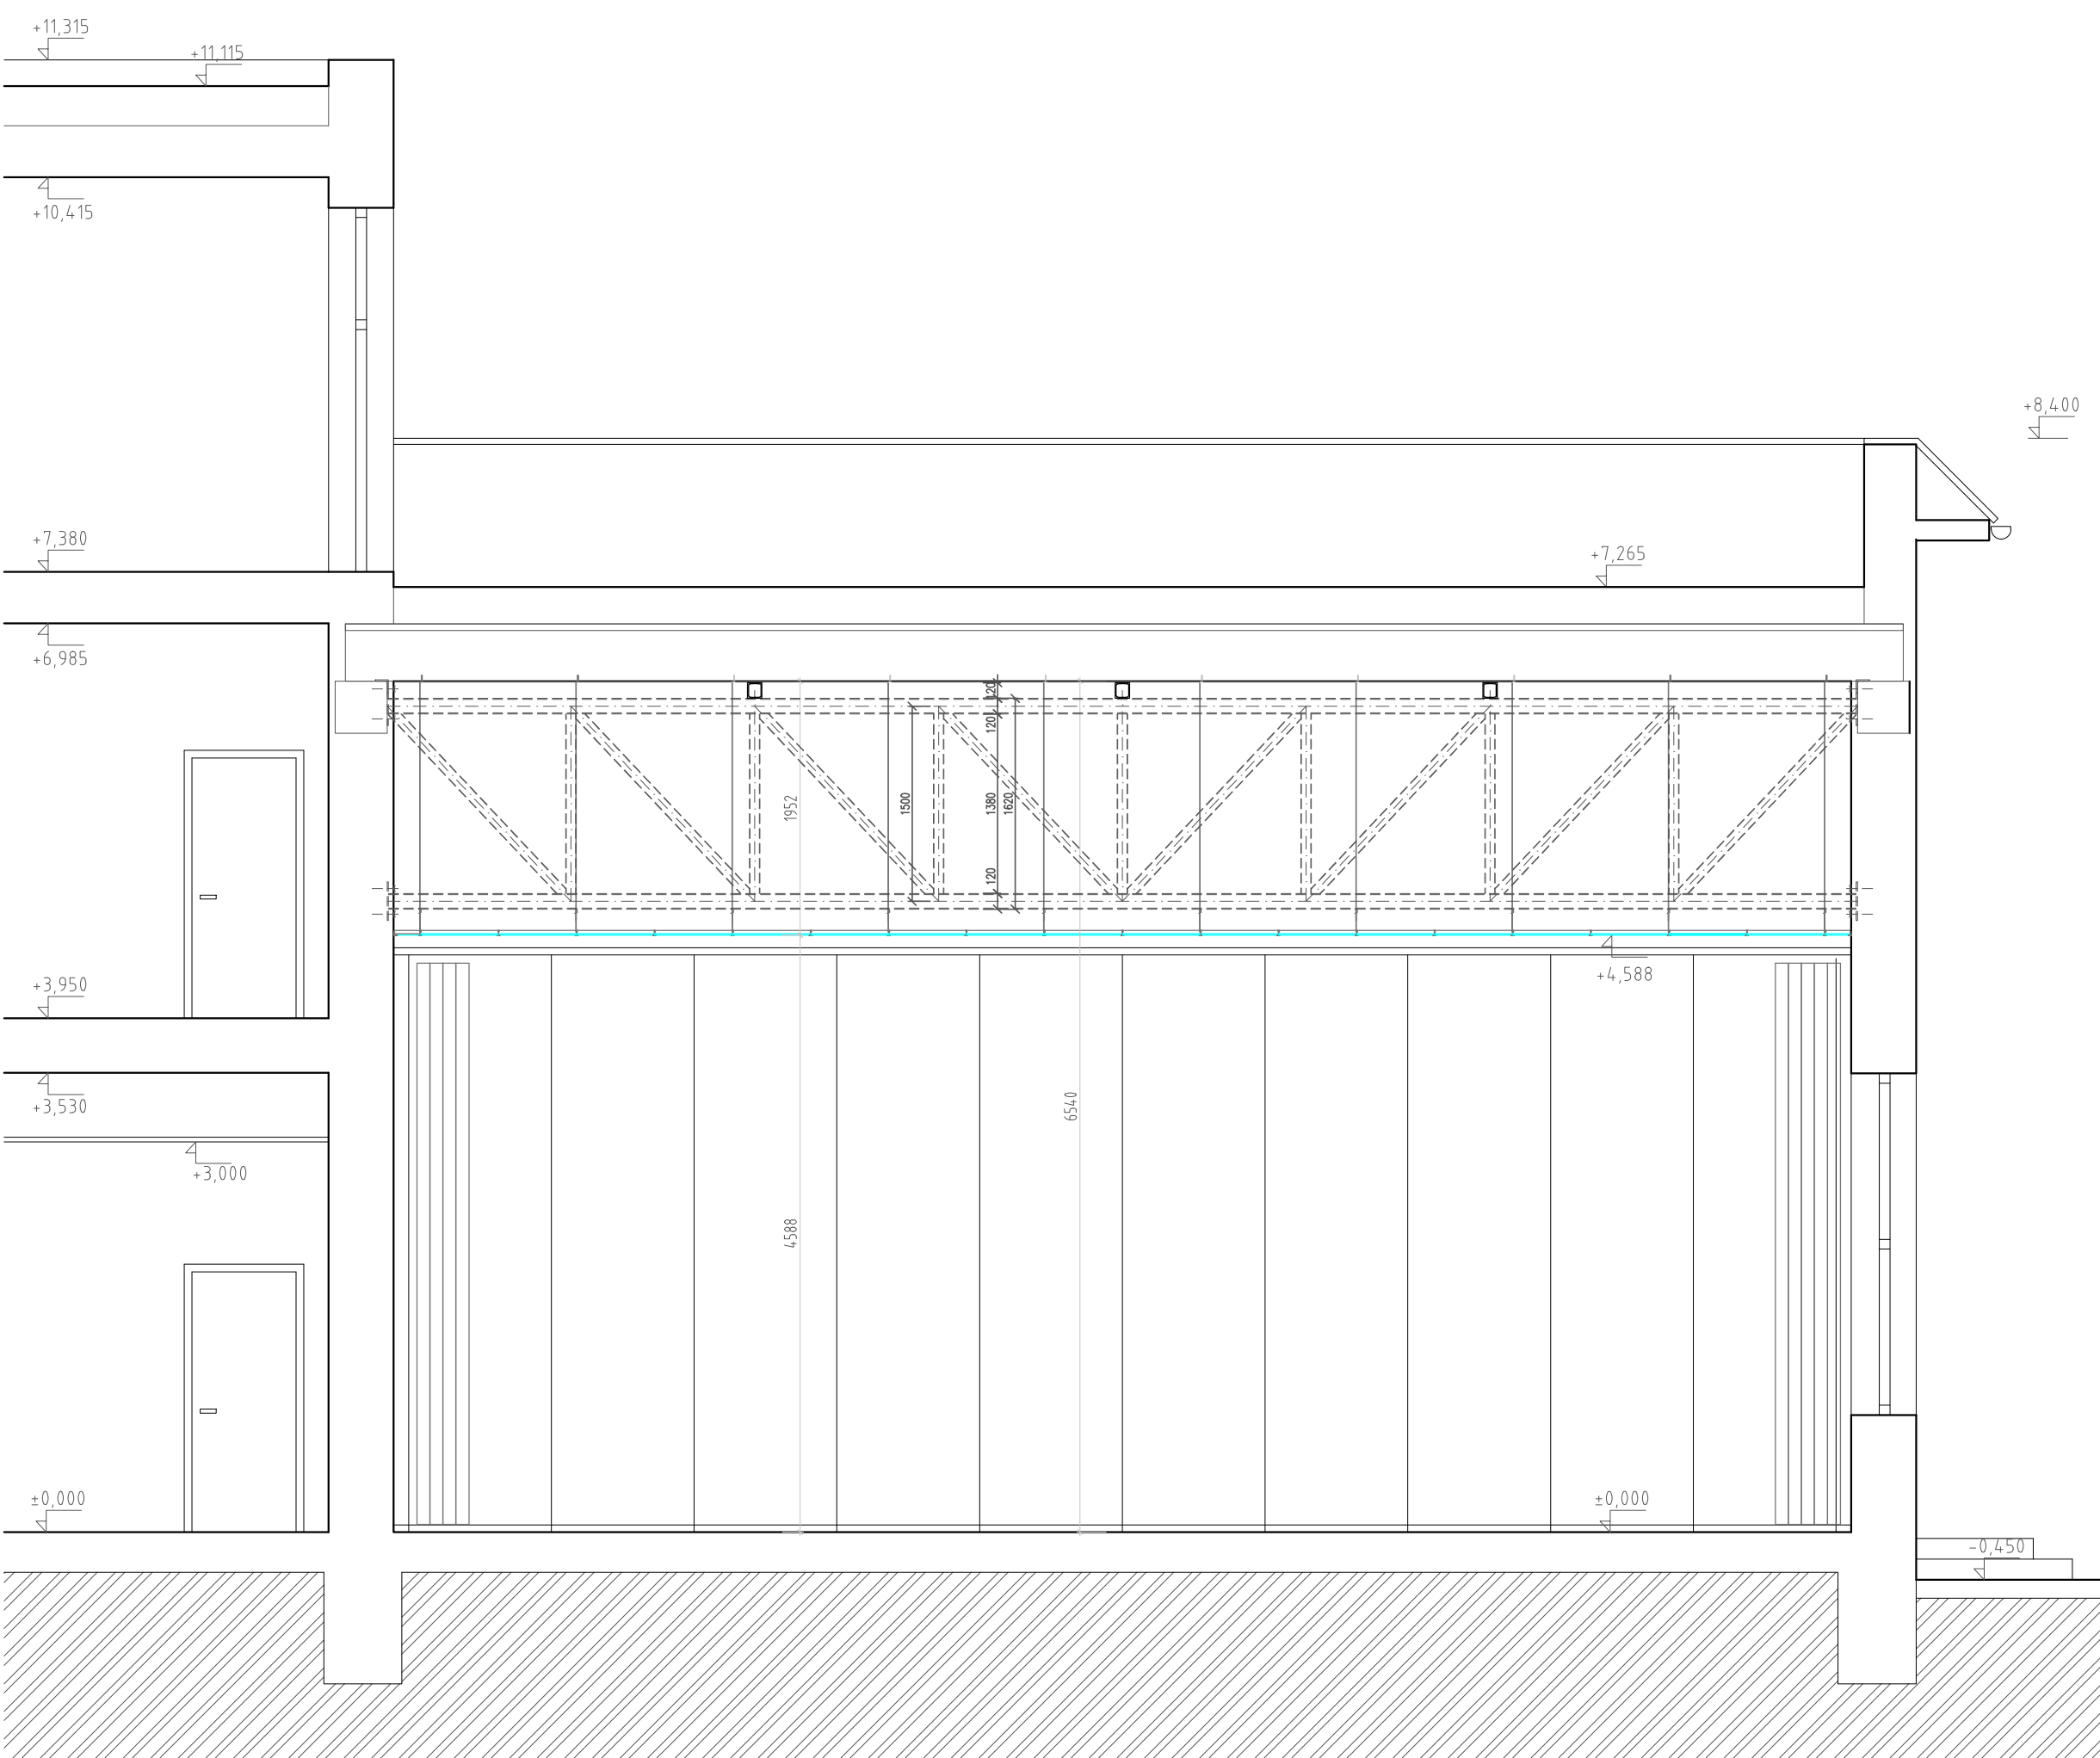

SADA Č.	ZOOP. PROJEKTANT: ING. ARCH. MARIÁN KURUC ARCHITEKTURA: ING. ARCH. M. KURUC, ING. ARCH. P. KNÁŽEK, ING. ARCH. I. ČITÁRY ML. HIP.: ING. ARCH. MARIÁN KURUC VYPRACOVAL: ING. PAVOL PEČIAR INVESTOR: UKF TIEĎA ANDREA JA HLINKU I, 94,9 74 NITRA	PROJEKTOVÁ KANCELÁRIA  e-mail: shfinal@shfinal.sk
	VÝKRES Č. 13 NÁZOV: PORADENSKÉ CENTRUM UKF V NITRE -ÚPRAVA	DÁTUM: 12/2016 STUPEŇ: J.P. Č. ZAK.: MERITOKO: M=150 M=110 FORMÁT: 8x A4
	OBSAH: MOBILNÁ DELIACA STENA	ČASŤ: A R C H.