



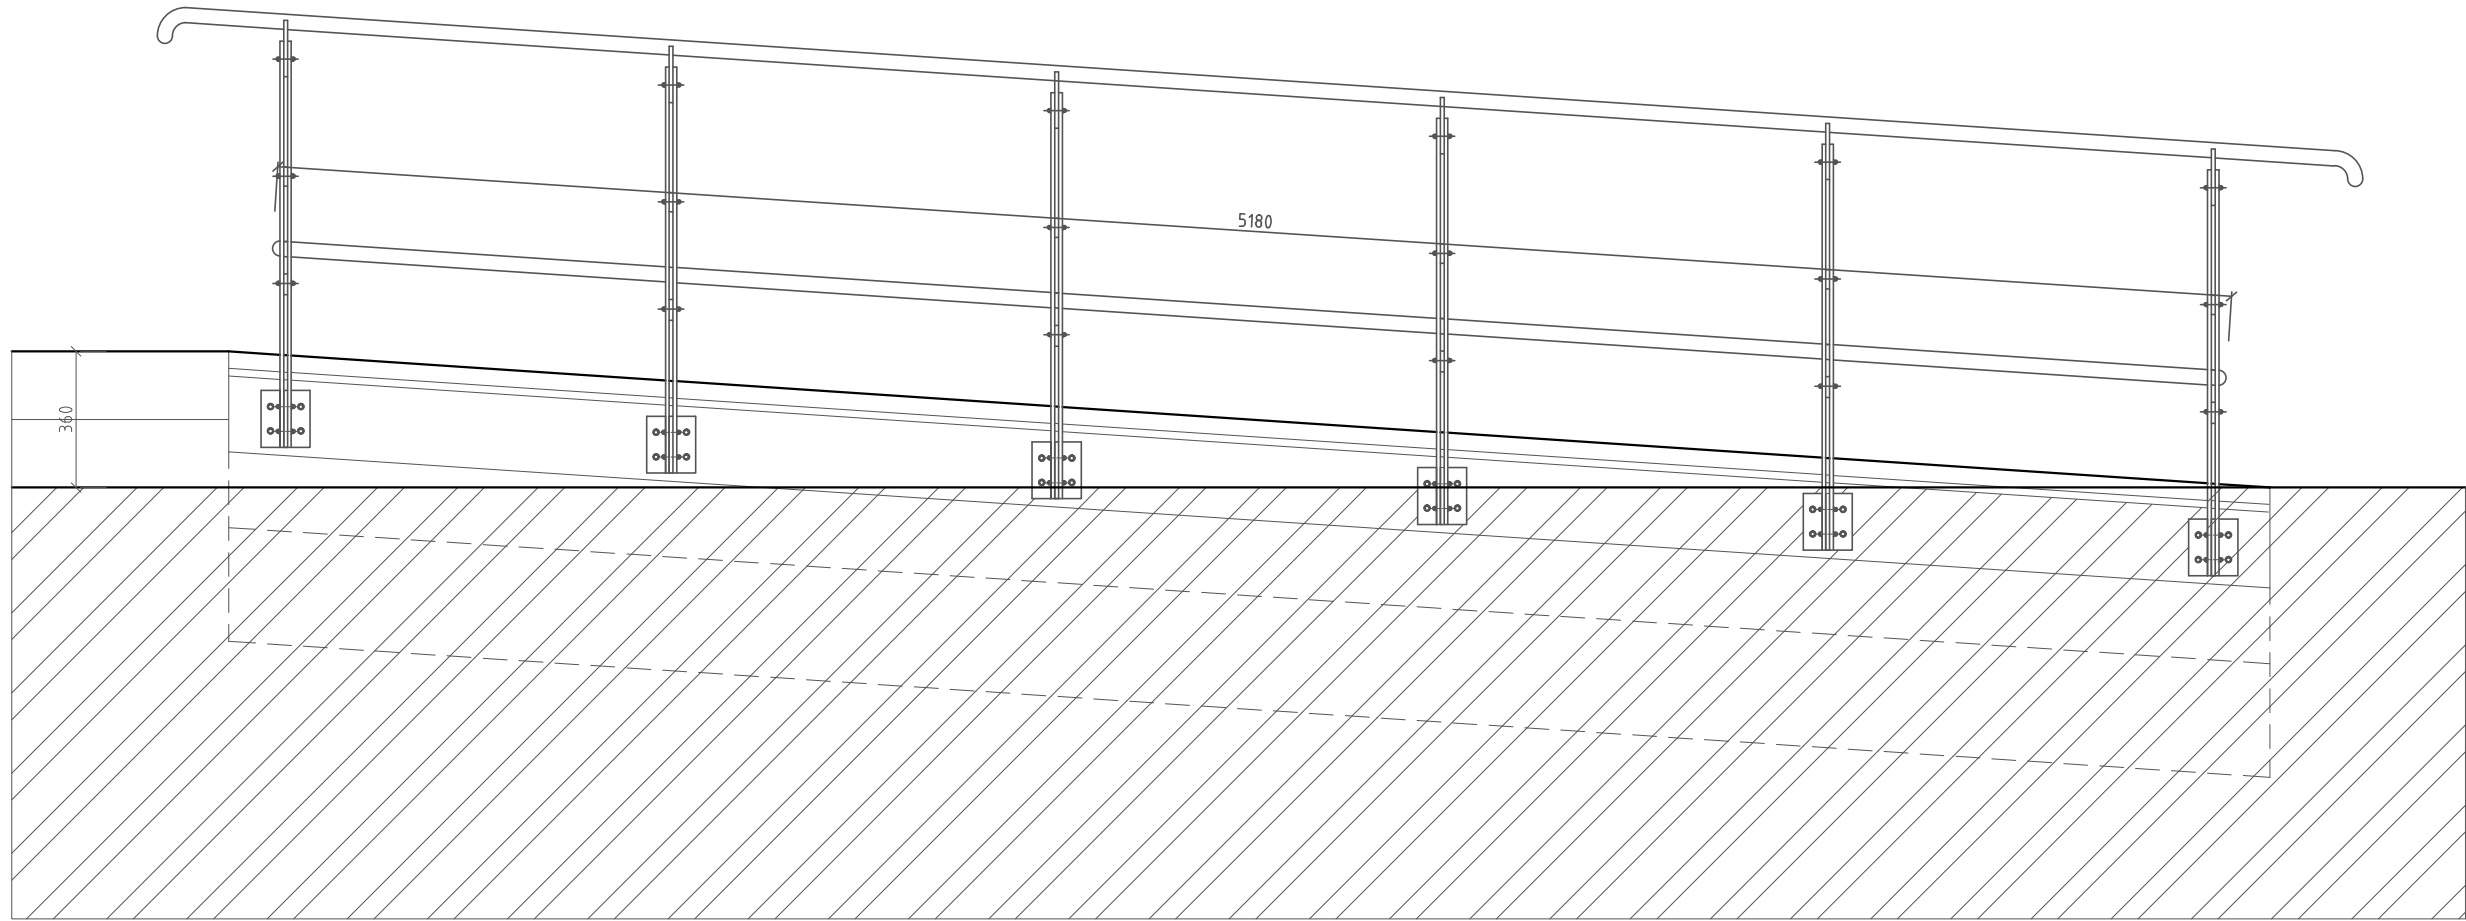


POHL'AD
M= 1:20

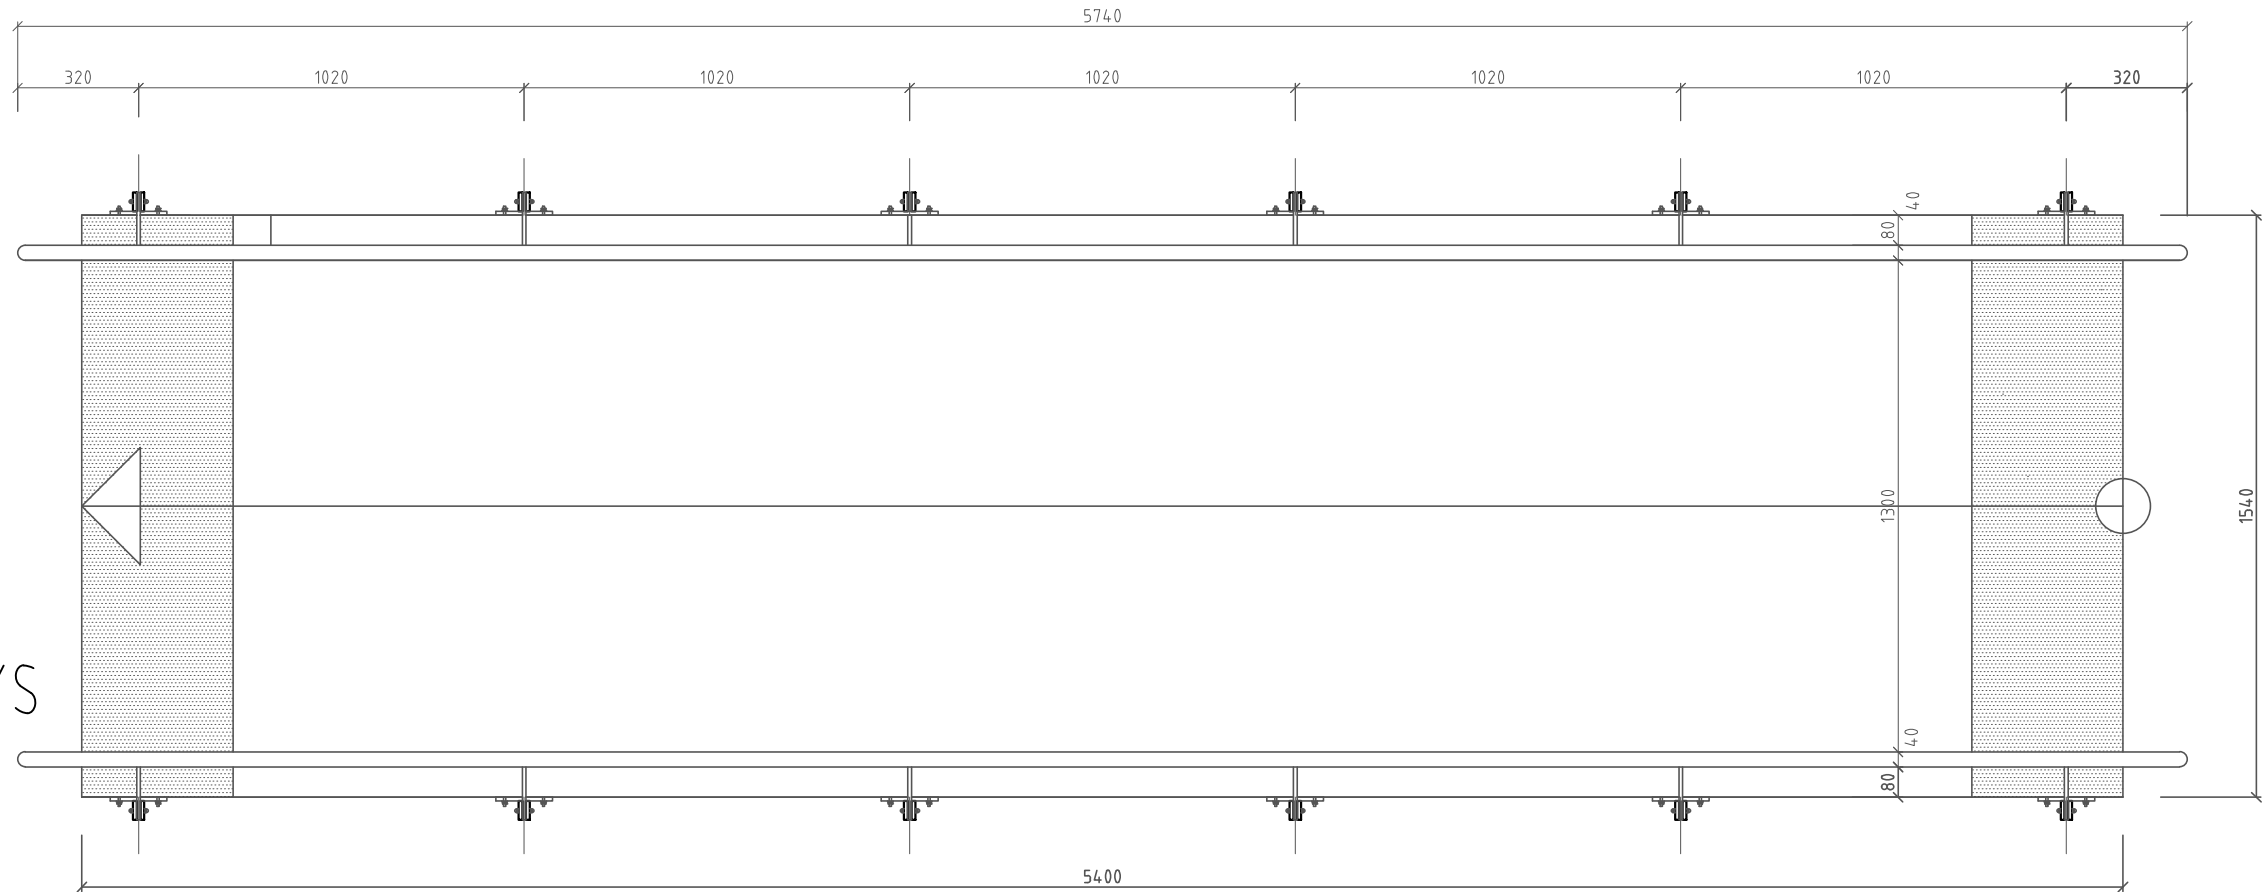


PÔDORYS
M= 1:20

REZ
M= 1:10

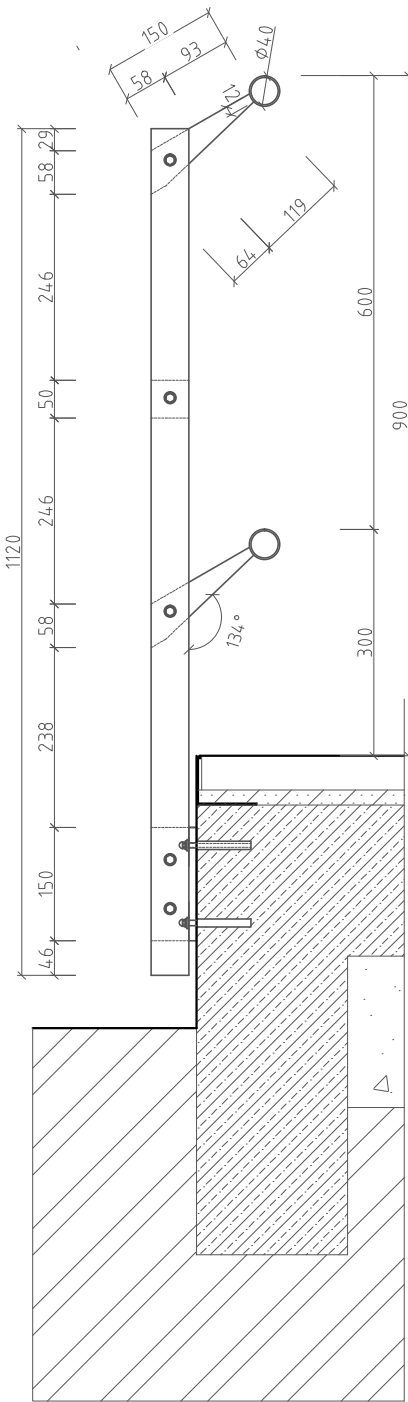


PÔDORYS
M= 1:10

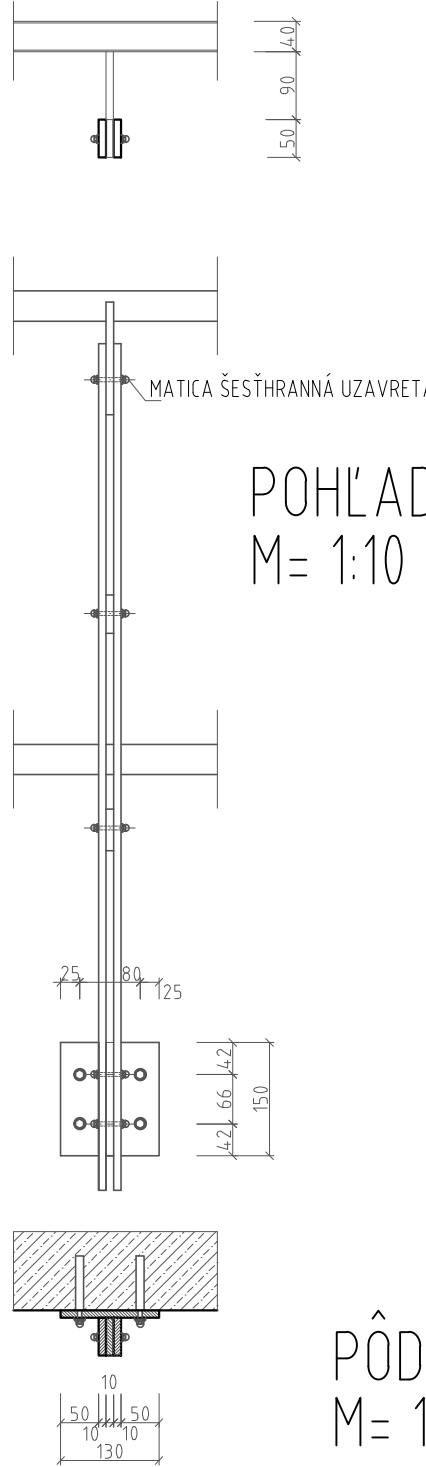

PÔDORYS
M= 1:10

REZ
M= 1:20

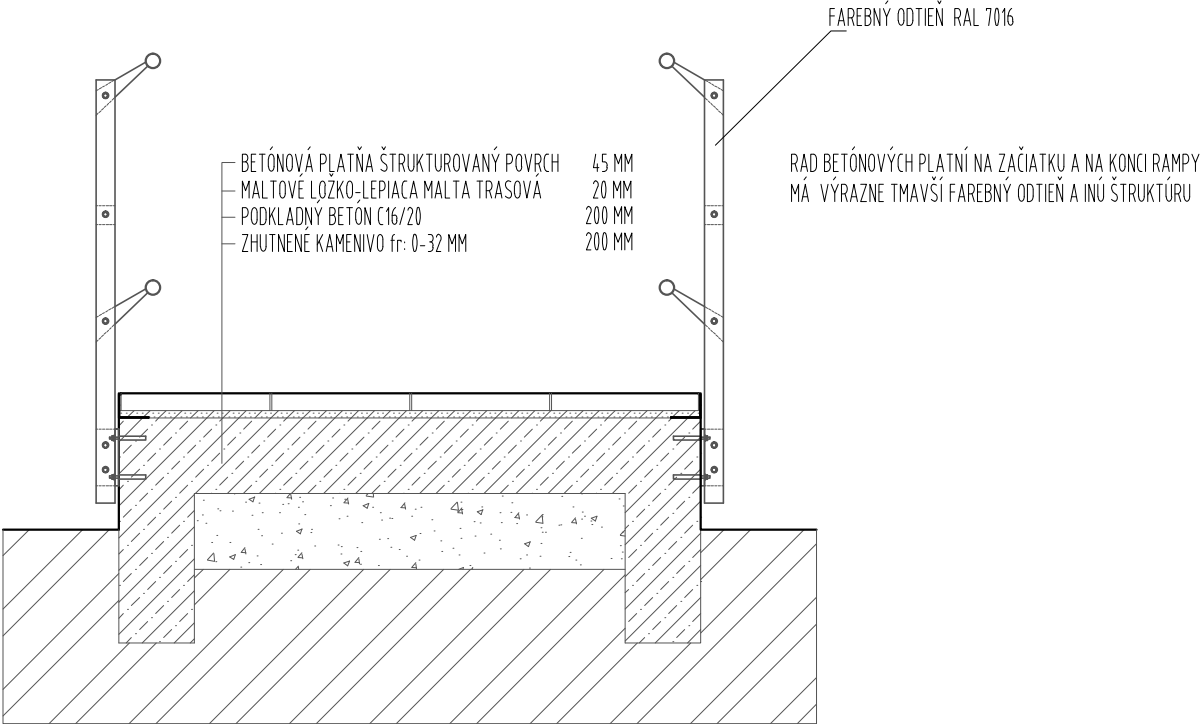

VÝPIS MATERIÁLU

DRUH MATERIÁLU	MNOŽSTVO m	HMOTNOSŤ	
		KG/m	CELKOM
kg			
TYČ PLOCHÁ 50/10	17,16	3,93	67,44
TRUBKA D=40/2,5 NEREZ	24	2,348	56,35
TYČ PLOCHÁ 150/10	1,56	11,78	18,38
KOTVY DO BETÓNU	48 ks		
VÁHA OCELE CELKOM kg			142,17

SADA Č.:	ZODP. PROJEKTANT: ING. ARCH. MARIÁN KURUC	PROJEKTOVÁ KANCELÁRIA SHfinal s.r.o. e-mail: shfinal@shfinal.sk
	ARCHITEKTÚRA: ING. ARCH. M. KURUC, ING. ARCH. P. KŇAŽEK, ING. ARCH. I. ČITÁRY ml.	
	H.I.P.: ING. ARCH. MARIÁN KURUC	
	VYPRACOVAL: ING. PAVOL PECIAR	
VÝKRES Č. 14	INVESTOR: UKF TRIEDA ANDREJA HLINKU 1, 949 74 NITRA	DÁTUM: 12/2016
	PORADENSKÉ CENTRUM UKF V NITRE -ÚPRAVA	STUPEŇ: J.P.
		Č. ZAK.: M=1:20
		MERÍTKO: 3x A4
OBSAH:	DETAIL ZÁBRADLIA RAMPY	ČASŤ: ARCH.