


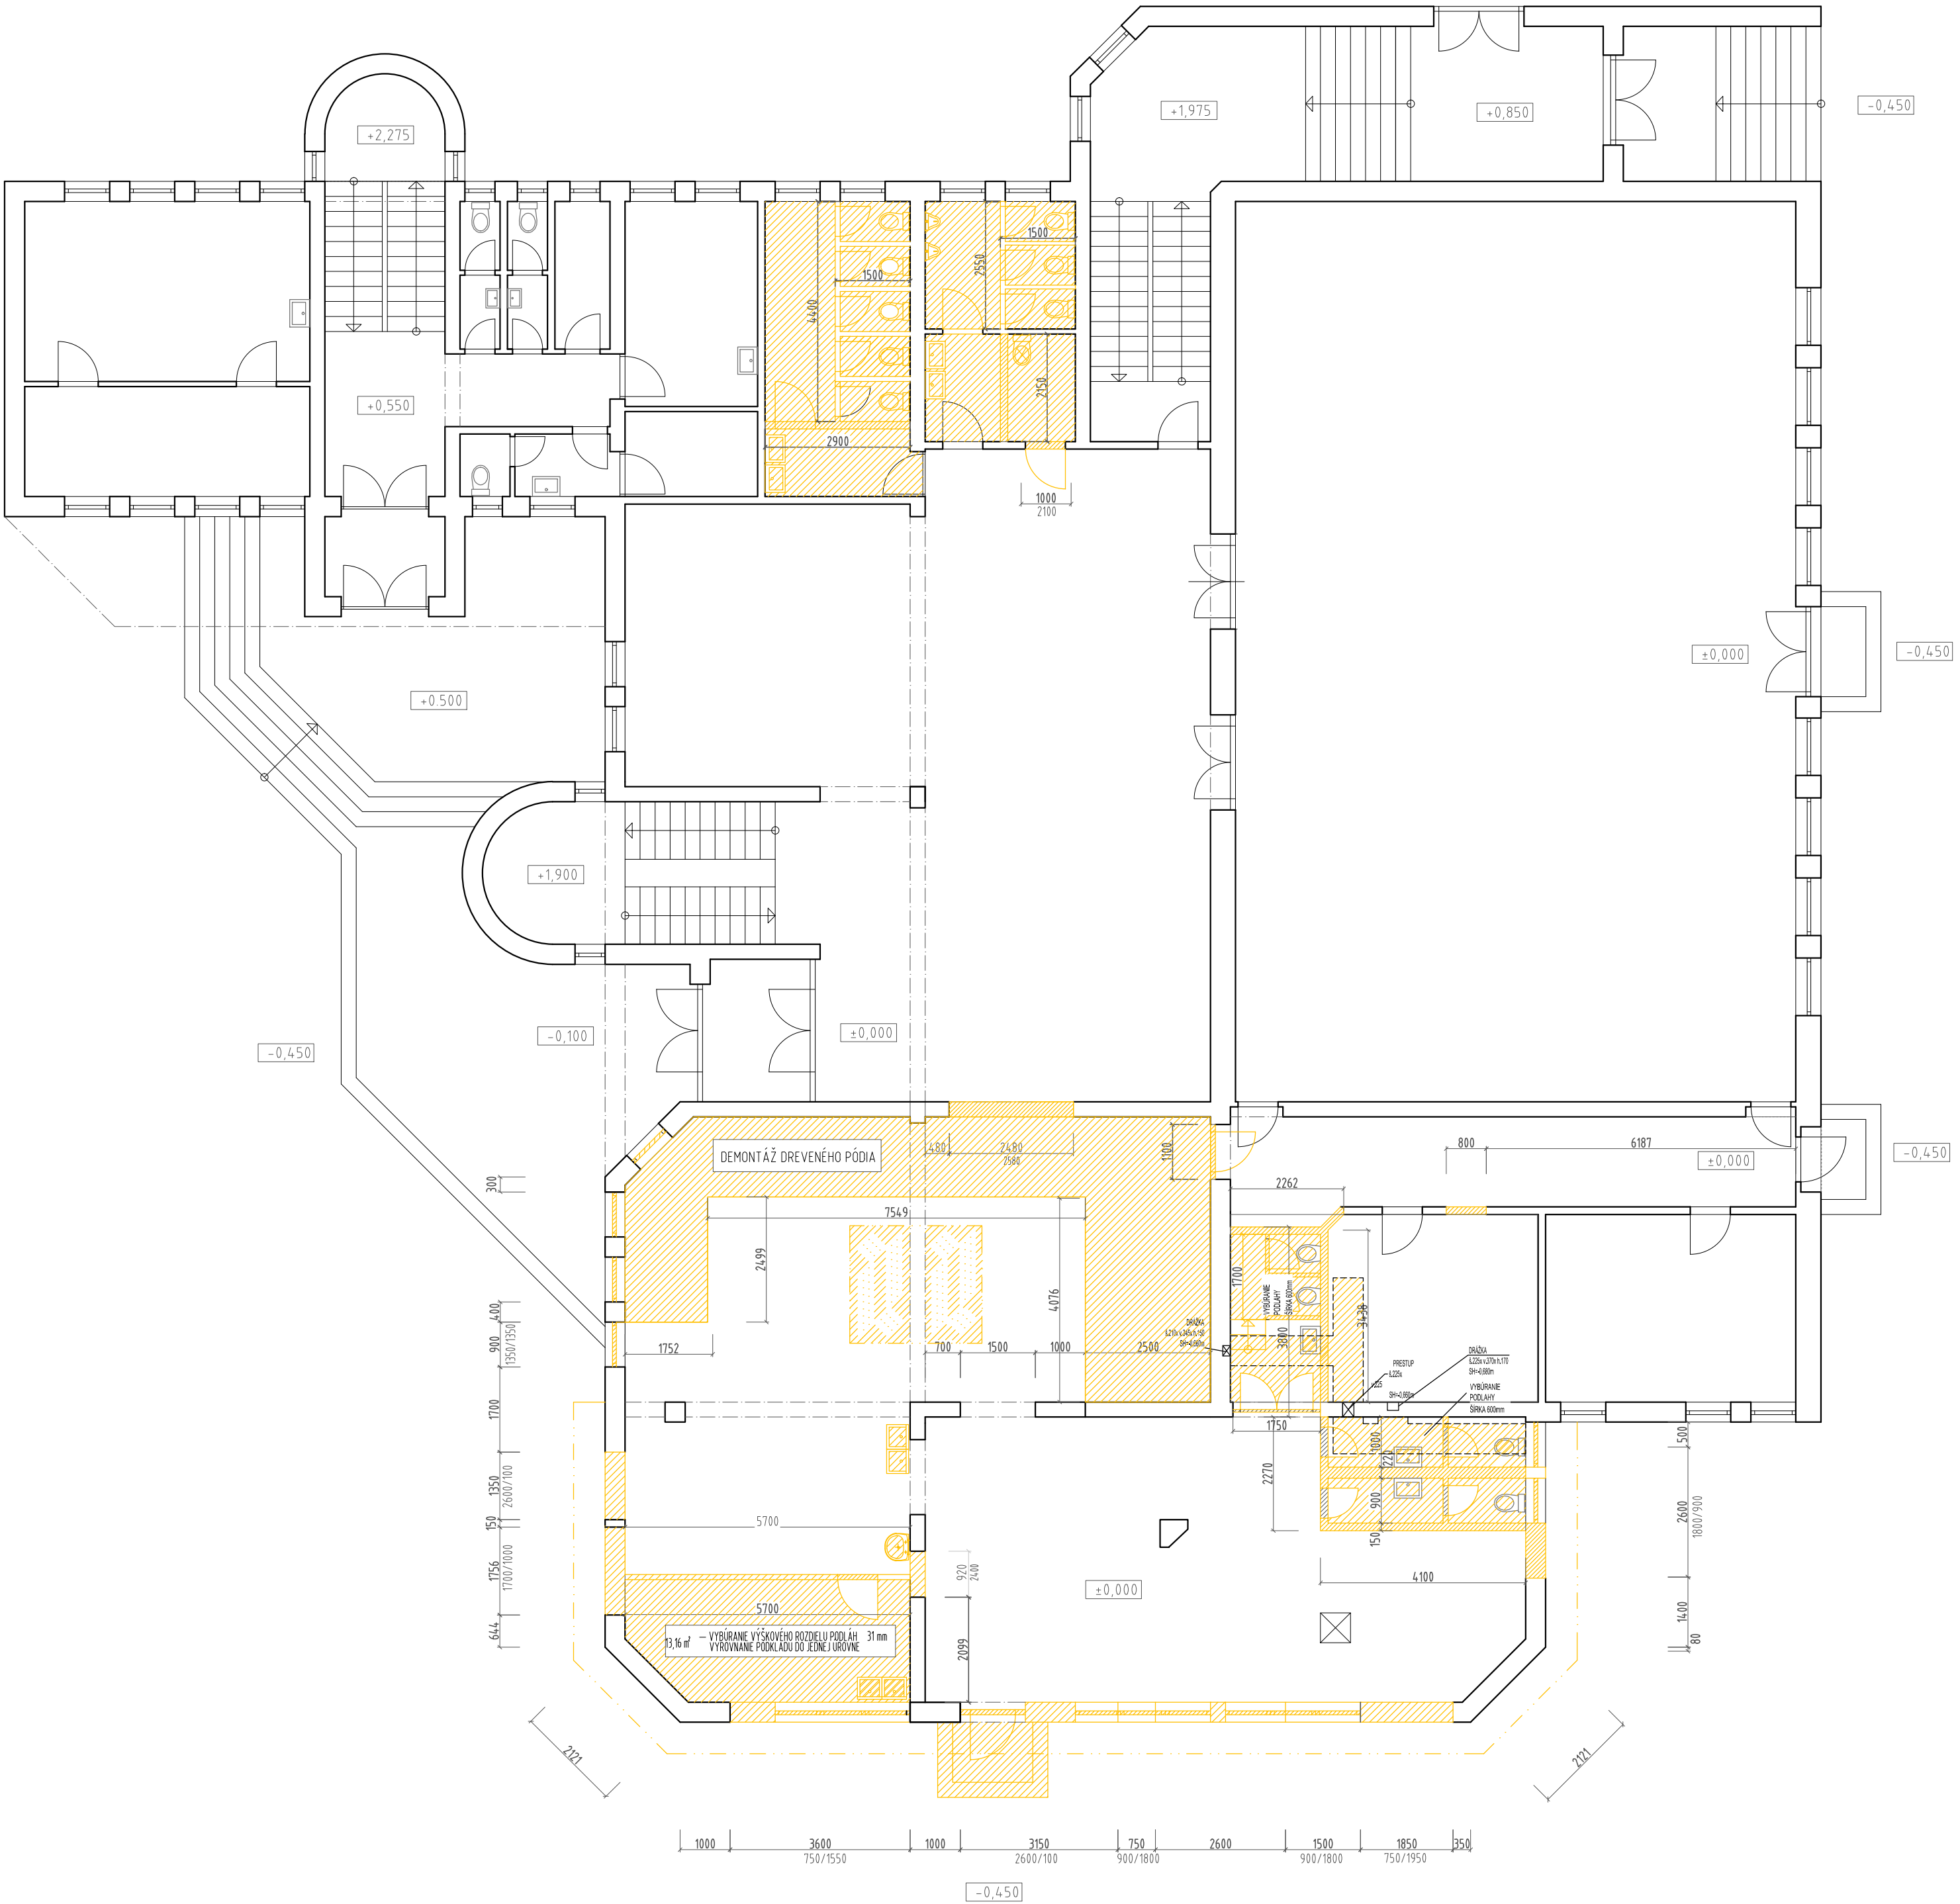

SADA Č.:	ZODP. PROJEKTANT: ING. ARCH. MARIÁN KURUC	PROJEKTOVÁ KANCELÁRIA SHfinal.s.r.o. e-mail: shfinal@shfinal.sk
	ARCHITEKTÚRA: ING. ARCH. M. KURUC, ING. ARCH. P. KŇÁŽEK, ING. ARCH. I. ČITÁRY ml.	
	H.I.P.: ING. ARCH. MARIÁN KURUC	
	VYPRACOVAL: ING. PAVOL PEČIAR	
VÝKRES Č. 19	INVESTOR: UKF TRIEDA ANDREJA HLINKU 1, 949 74 NITRA	DÁTUM: 12/2016
	PORADENSKÉ CENTRUM UKF V NITRE -ÚPRAVA	STUPEŇ: J.P
		Č. ZAK.:
		MÉRITKO: M=1:100
	OBSAH: BURACIE PRÁCE	FORMAT: 8x A4
		ČASŤ: ARCH.